



CIVIL CONSTRUCTION
DRAWINGS

SITE NAME: COHOCTON SOLAR
FARM, LLC

11190 NY 371
COHOCTON, NY

C&S PROJECT: AB7.009.001


JULY 2023



TO THE BEST OF OUR KNOWLEDGE, INFORMATION AND BELIEF
THE PLANS AND SPECIFICATIONS FOR THIS PROJECT ARE IN
COMPLIANCE WITH THE NEW YORK STATE ENERGY
CONSERVATION CONSTRUCTION CODE AND THE BUILDING
CODE OF NEW YORK STATE


NO ALTERATION PERMITTED HEREON EXCEPT AS PROVIDED
UNDER SECTION 7209 SUBDIVISION 2 OF THE NEW YORK
STATE EDUCATION LAW

G-001

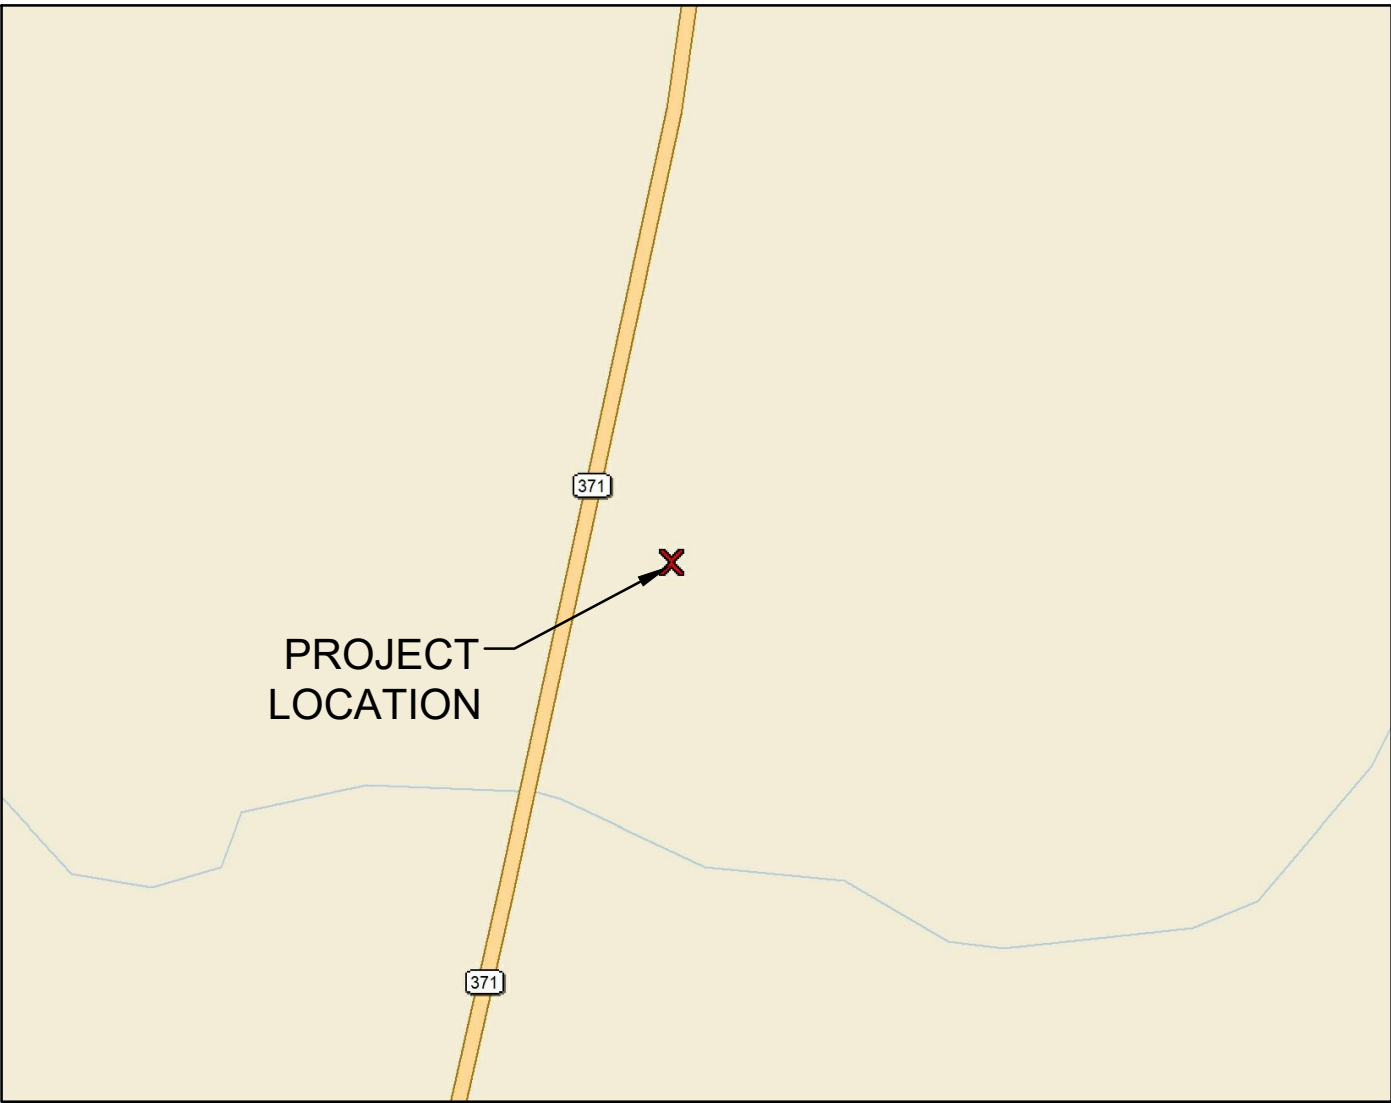

LOCATION MAP

DIRECTIONS TO SITE: (FROM SYRACUSE INTERNATIONAL AIRPORT) TRAVEL ON I-90
WEST TO EXIT 42. TURN RIGHT ONTO SR14 TOWARDS SR96 WEST. FOLLOW SR96 WEST
TO A LEFT ONTO CR6. FOLLOW CR6 TO A RIGHT ONTO US20 THEN A LEFT ONTO SR245.
FOLLOW SR245 TO A LEFT ONTO SR21. FOLLOW SR21 AND CONTINUE STRAIGHT ONTO
SR371. SITE IS ON THE LEFT.

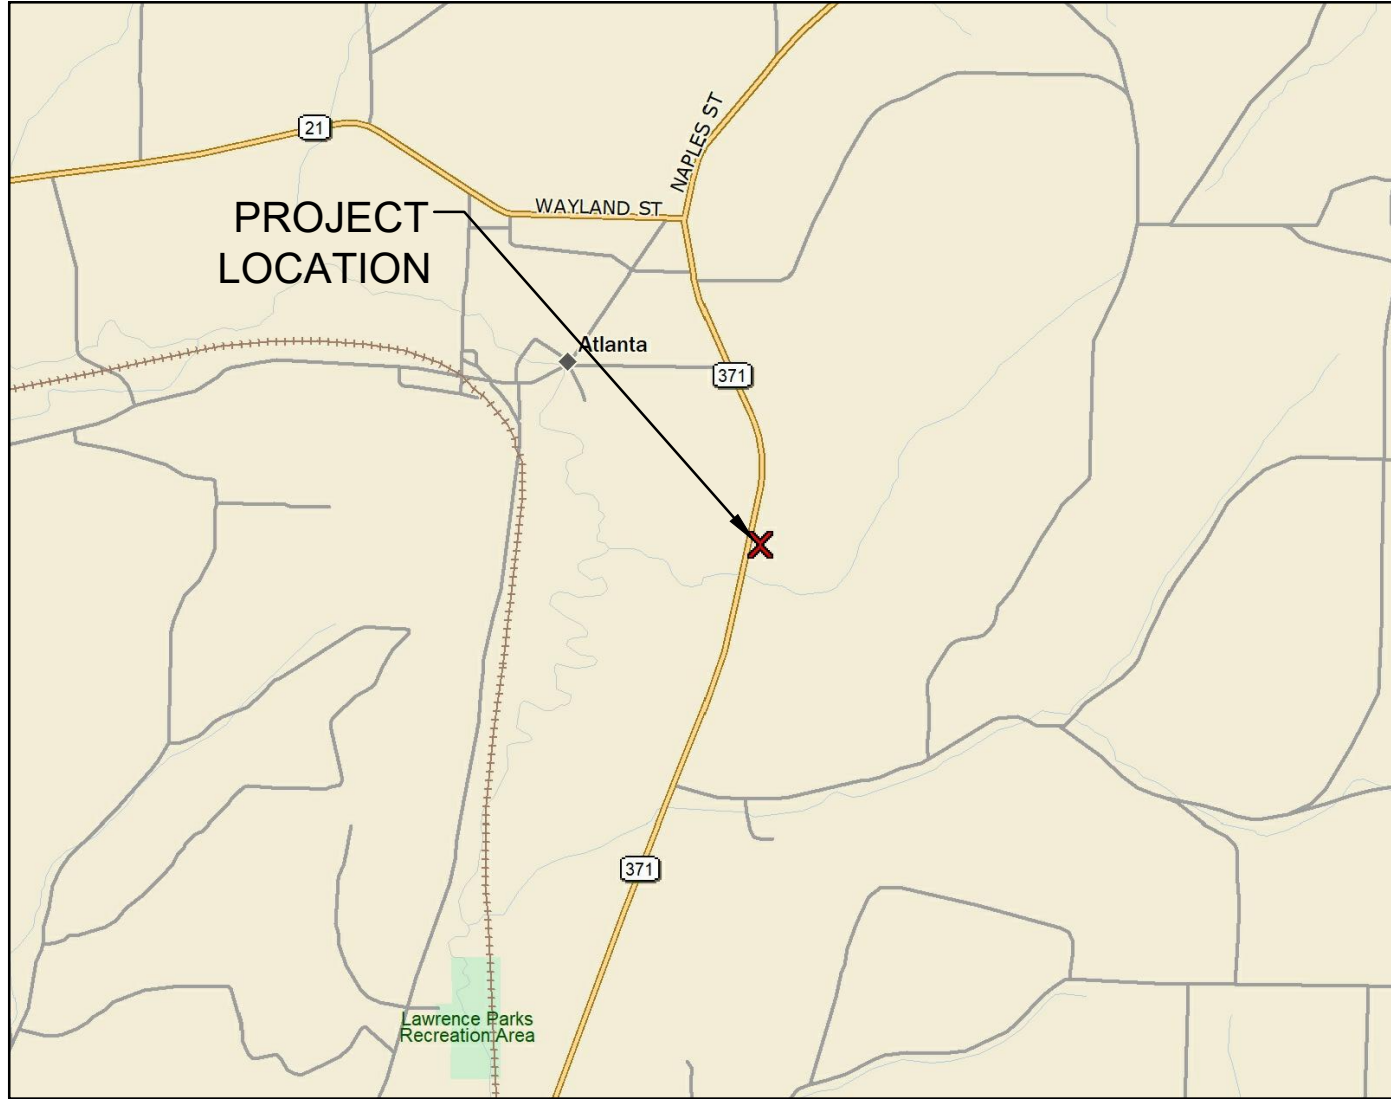

VICINITY MAP

PROJECT INFORMATION

PROPERTY OWNER:	OVAN CAPITAL LLC 353 FOREST LANE SMITHTOWN, NY 11787
SITE NAME:	COHOCTON SOLAR FARM, LLC
SITE ADDRESS:	11190 NY 371 COHOCTON, NY
TAX MAP #:	030.00-01-005.200
ZONING JURISDICTION:	TOWN OF COHOCTON
ZONING DISTRICT:	AGRICULTURAL RESIDENTIAL (AG-R)
COUNTY:	STEUBEN COUNTY

PROJECT DIRECTORY

APPLICANT:	PFISTER-COHOCTON SOLAR FARM, LLC 57 GOFFLE ROAD HAWTHORNE, NJ 07506
CONTACT: PHONE: EMAIL:	DOUG BAGWILL 201-655-2959 dbagwill@pfisterenergy.com
CIVIL ENGINEERING FIRM:	C&S ENGINEERS INC. 499 COL. EILEEN COLLINS BLVD. SYRACUSE, NY 13212
CONTACT: PHONE:	ERIC N. KENNA P.E. (315) 455-2000
POWER COMPANY: PHONE:	NATIONAL GRID 1 (800) 892-2345

GENERAL NOTES

THE FACILITY IS UNMANNED AND NOT FOR HUMAN HABITATION. A
TECHNICIAN WILL VISIT THE SITE AS REQUIRED FOR ROUTINE
MAINTENANCE. THE PROJECT WILL NOT RESULT IN ANY
SIGNIFICANT DISTURBANCE OR EFFECT ON DRAINAGE; NO
SANITARY SEWER SERVICE, POTABLE WATER, OR TRASH DISPOSAL
IS REQUIRED AND NO COMMERCIAL SIGNAGE IS PROPOSED.



811

- ☐ Call Before You Dig
- ☐ Wait The Required Time
- ☐ Confirm Utility Response
- ☐ Respect the Marks
- ☐ Dig With Care

DRAWING LIST

SHEET NO.	SHEET NAME	REV	DATE
GENERAL			
G-001	TITLE SHEET	2	11-8-23
CIVIL			
C-101	AERIAL SITE PLAN	2	11-8-23
C-102	OVERALL SITE PLAN	2	11-8-23
C-103	SITE GRADING PLAN	2	11-8-23
C-104	ROAD GRADING PLAN	2	11-8-23
C-105	BASIN GRADING PLANS	2	11-8-23
C-106	PLANS	2	11-8-23
C-107	PROFILES	2	11-8-23
C-108	PROFILES	2	11-8-23
C-109	EROSION AND SEDIMENT CONTROL PLAN	2	11-8-23
C-501	SITE DETAILS	2	11-8-23
C-502	FENCE DETAILS	2	11-8-23
C-503	DETAILS	2	11-8-23
C-504	EROSION AND SEDIMENT CONTROL DETAILS	2	11-8-23
C-505	EROSION AND SEDIMENT CONTROL DETAILS	2	11-8-23



TJA-NY-COHOCTON SOLAR FARM, LLC


**11190 NY 371
COHOCTON, NY**

LAT: 42.54452 LONG: -77.46018

MARK	DATE	DESCRIPTION
REVISIONS		
PROJECT NO:	AB7.009.001	
DATE:	JULY 2023	
DRAWN BY:	M. BUCKINGHAM	
DESIGNED BY:	E.N. KENNA P.E.	
CHECKED BY:	J.L. ROBBINS P.E.	
NO ALTERATION PERMITTED HEREON EXCEPT AS PROVIDED UNDER SECTION 7209 SUBDIVISION 2 OF THE NEW YORK EDUCATION LAW		

AERIAL SITE PLAN

C-101

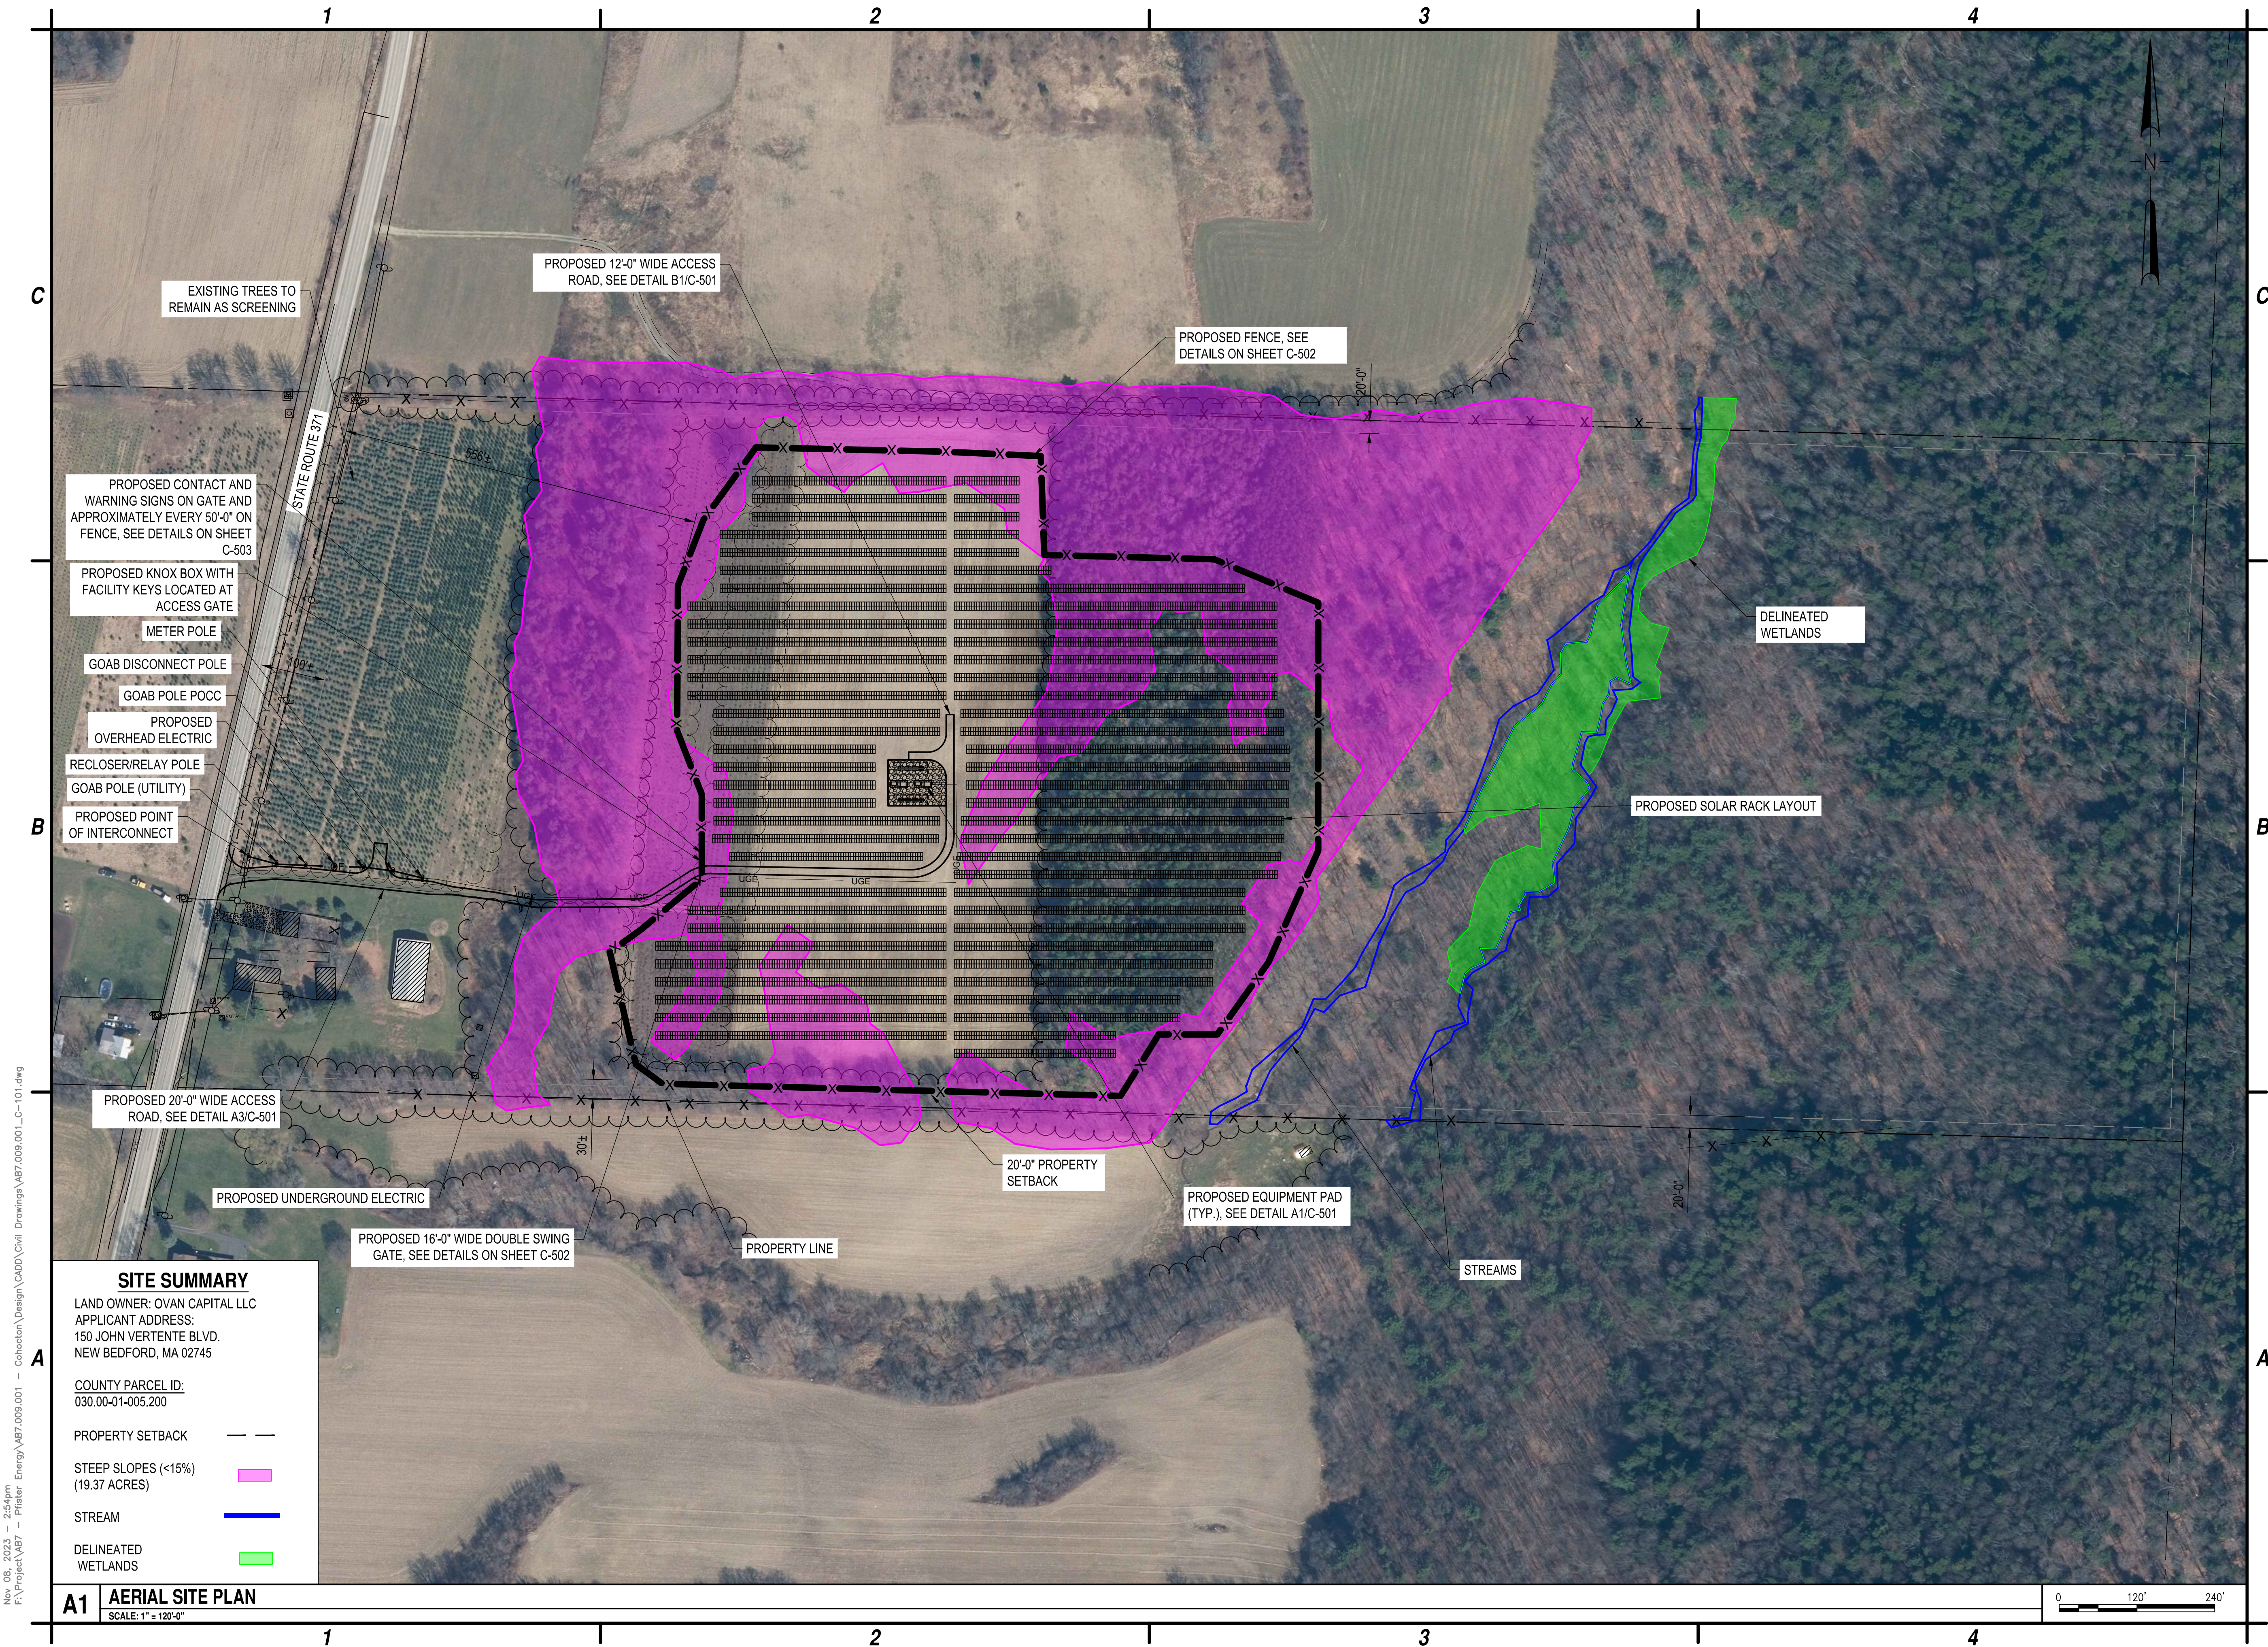

Nov 08, 2023 - 2:57pm F:\Project\A87 - Pfister Energy\A87.009.001 - Cohocton\Design\CADD\Civil Drawings\A87.009.001_C-102.dwg



SITE SUMMARY

LAND OWNER: OVAN CAPITAL LLC
APPLICANT ADDRESS:
150 JOHN VERTENTE BLVD.
NEW BEDFORD, MA 02745

COUNTY PARCEL ID:
030.00-01-005.200

- PROPERTY SETBACK - - - - -
- STEEP SLOPES (<15%)
(19.37 ACRES) [Pink Shaded Area]
- STREAM [Blue Line]
- DELINEATED WETLANDS [Green Shaded Area]

A1 OVERALL SITE PLAN
SCALE: 1" = 120'-0"



C&S Engineers, Inc.
499 Col. Eileen Collins Blvd.
Syracuse, New York 13212
Phone: 315-455-2000
Fax: 315-455-9667
www.cscos.com



TJA-NY-COHOCTON SOLAR FARM, LLC

**11190 NY 371
COHOCTON, NY**

LAT: 42.54452 LONG: -77.46018

2	11-8-23	SITE LAYOUT
1	6-24-22	ISSUED FOR PERMITTING
MARK	DATE	DESCRIPTION
REVISIONS		
PROJECT NO: AB7.009.001		
DATE: JULY 2023		
DRAWN BY: M. BUCKINGHAM		
DESIGNED BY: E.N. KENNA P.E.		
CHECKED BY: J.L. ROBBINS P.E.		
NO ALTERATION PERMITTED HEREON EXCEPT AS PROVIDED UNDER SECTION 7209 SUBDIVISION 2 OF THE NEW YORK EDUCATION LAW		

OVERALL SITE PLAN

C-102

Nov 08, 2023 - 3:00pm F:\Project\A87 - Pfister Energy\A87.009.001 - Cohocton\Design\CADD\Civil Drawings\A87.009.001_C-103.dwg



SITE SUMMARY

LAND OWNER: OVAN CAPITAL LLC
APPLICANT ADDRESS:
150 JOHN VERTENTE BLVD.
NEW BEDFORD, MA 02745

COUNTY PARCEL ID:
030.00-01-005.200

PROPERTY SETBACK
STREAM
DELINEATED WETLANDS

A1 SITE GRADING PLAN
SCALE: 1" = 120'-0"

0 120' 240'



C&S Engineers, Inc.
499 Col. Eileen Collins Blvd.
Syracuse, New York 13212
Phone: 315-455-2000
Fax: 315-455-9667
www.cscos.com



TJA-NY-COHOCTON SOLAR FARM, LLC

11190 NY 371
COHOCTON, NY


LAT: 42.54452 LONG: -77.46018

2	11-8-23	SITE LAYOUT
1	6-24-22	ISSUED FOR PERMITTING
MARK	DATE	DESCRIPTION
REVISIONS		
PROJECT NO: AB7.009.001		
DATE: JULY 2023		
DRAWN BY: M. BUCKINGHAM		
DESIGNED BY: E.N. KENNA P.E.		
CHECKED BY: J.L. ROBBINS P.E.		
NO ALTERATION PERMITTED HEREON EXCEPT AS PROVIDED UNDER SECTION 7209 SUBDIVISION 2 OF THE NEW YORK EDUCATION LAW		

SITE GRADING PLAN

C-103

Nov 08, 2023 -- 3:07pm F:\Project\AB7 -- Pfister Energy\AB7.009.001 -- Cohocton\Design\CADD\Civil Drawings\AB7.009.001_C-105.dwg

 

C&S Engineers, Inc.
499 Col. Eileen Collins Blvd.
Syracuse, New York 13212
Phone: 315-455-2000
Fax: 315-455-9667
www.cscos.com



TJA-NY-COHOCTON SOLAR FARM, LLC
11190 NY 371
COHOCTON, NY
LAT: 42.54452 LONG: -77.46018


2	11-8-23	SITE LAYOUT
1	6-24-22	ISSUED FOR PERMITTING
MARK	DATE	DESCRIPTION
REVISIONS		
PROJECT NO: AB7.009.001		
DATE: JULY 2023		
DRAWN BY: M. BUCKINGHAM		
DESIGNED BY: E.N. KENNA P.E.		
CHECKED BY: J.L. ROBBINS P.E.		
NO ALTERATION PERMITTED HEREON EXCEPT AS PROVIDED UNDER SECTION 7209 SUBDIVISION 2 OF THE NEW YORK EDUCATION LAW		

BASIN GRADING PLAN


C-105

Nov 08, 2023 3:19pm F:\Project\A87 - Cohocton Solar Farm\Drawings\A87_009.001_C-106.dwg


C1 MAIN ACCESS ROAD PLAN
SCALE: 1" = 20'-0"

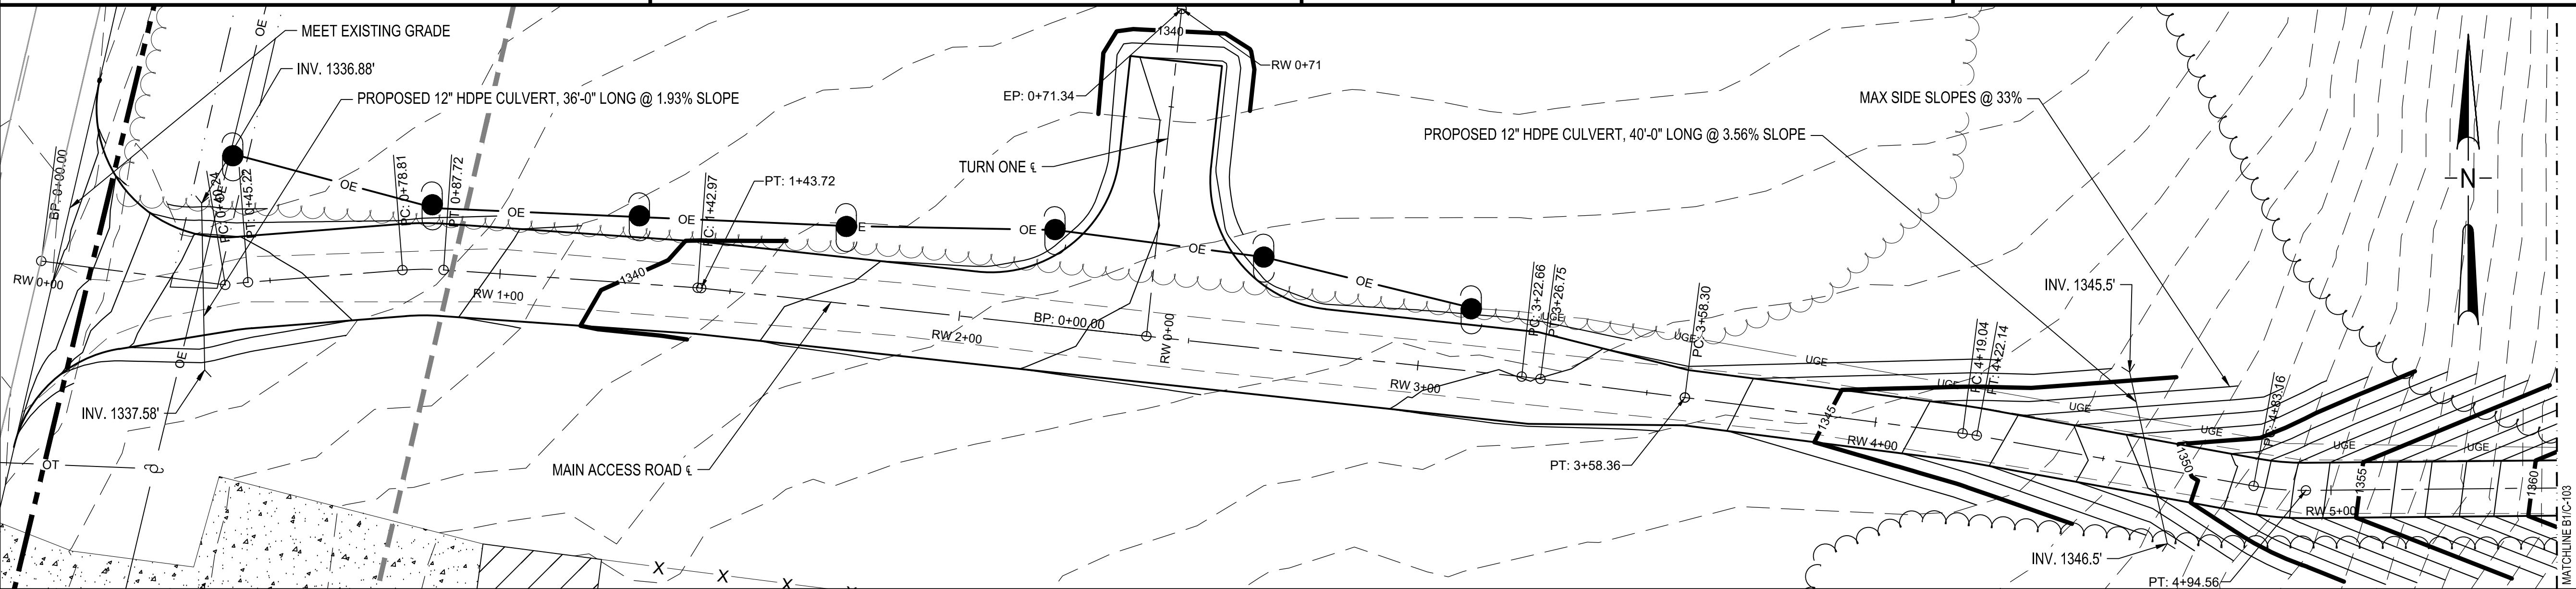

MAIN ACCESS ROAD PROFILE

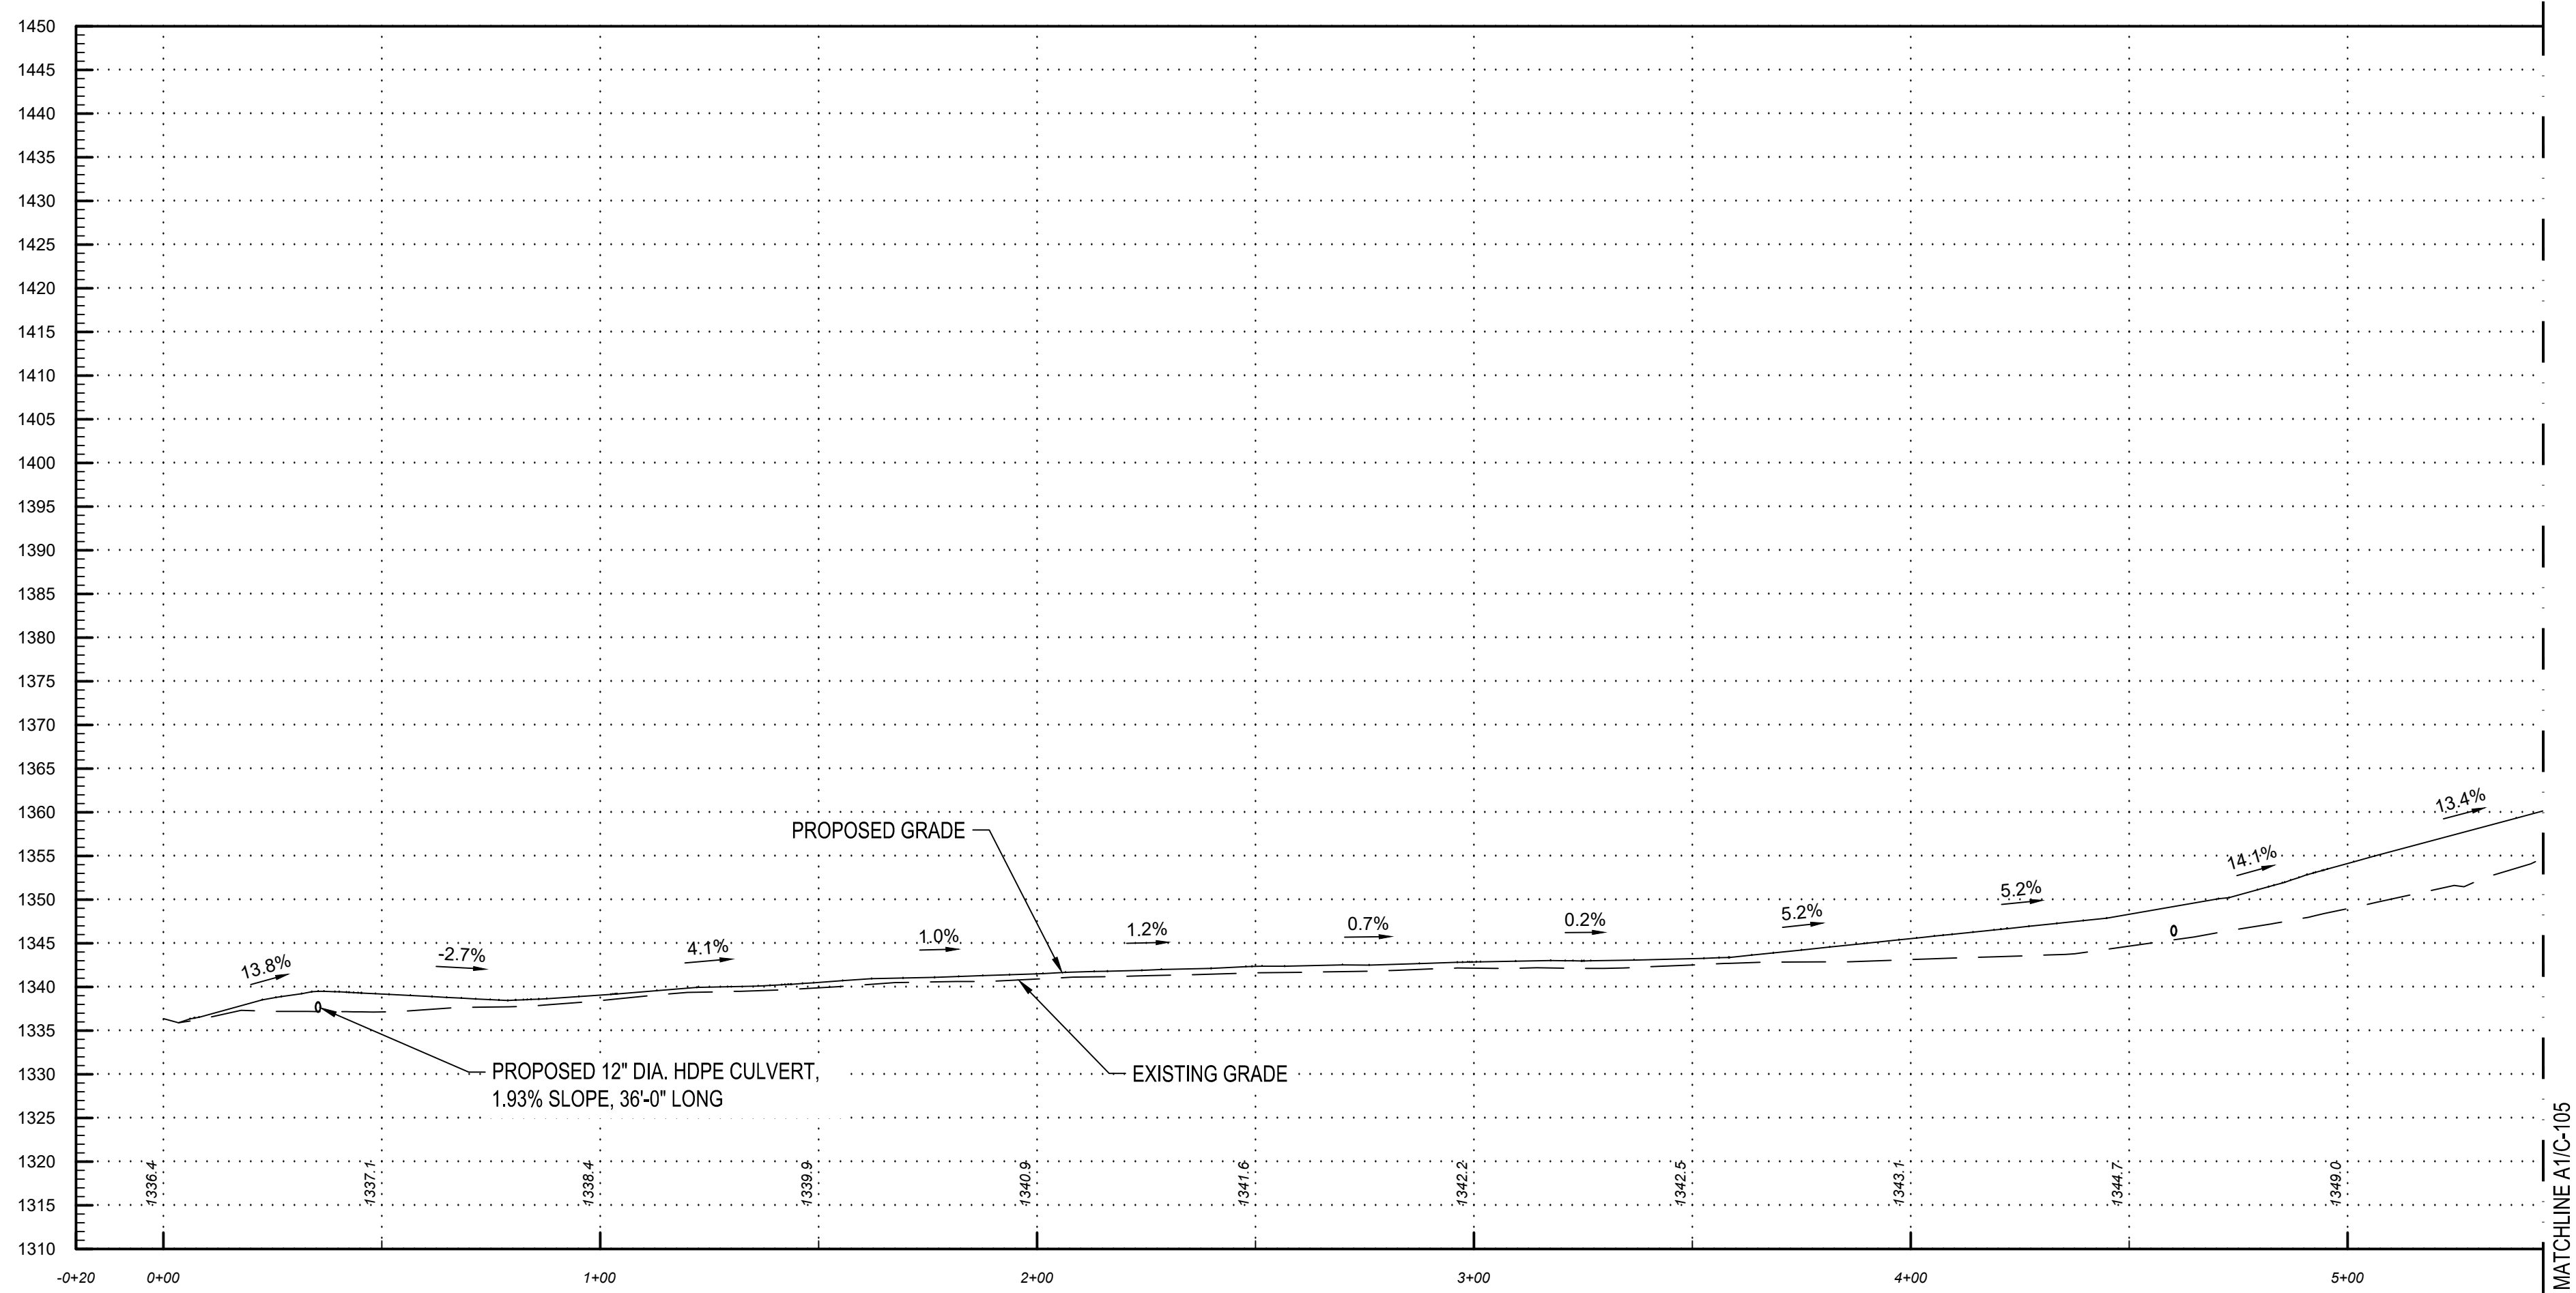

TURN ONE PROFILE

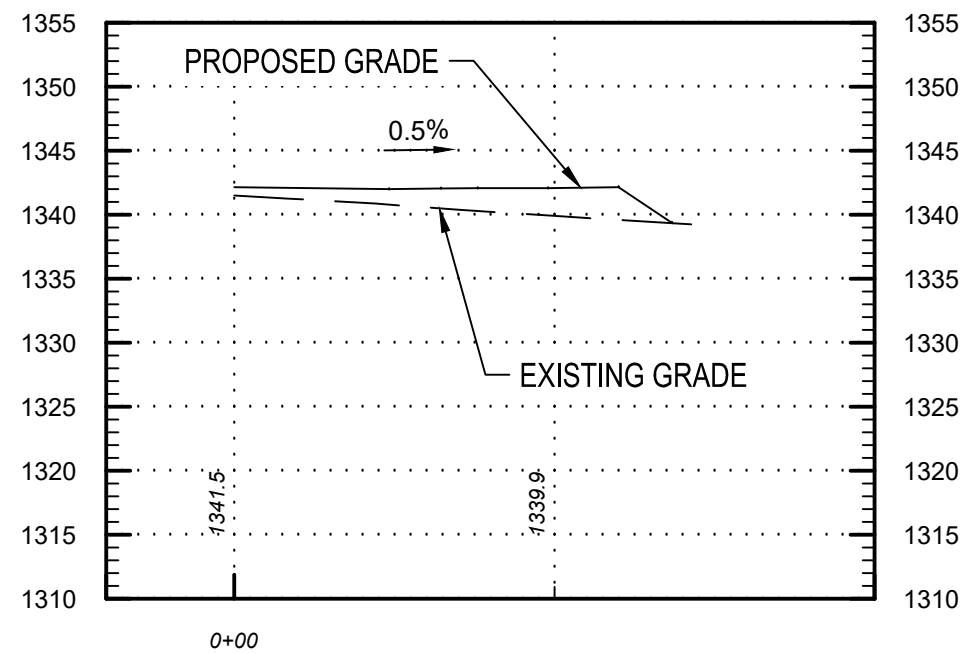

A1 MAIN ACCESS ROAD PROFILE
HORIZONTAL SCALE: 1" = 30'-0" VERTICAL SCALE: 1" = 15'-0"

A4 TURN ONE PROFILE
HORIZONTAL SCALE: 1" = 30'-0" VERTICAL SCALE: 1" = 15'-0"



C&S Engineers, Inc.
499 Col. Eileen Collins Blvd.
Syracuse, New York 13212
Phone: 315-455-2000
Fax: 315-455-9667
www.cscos.com



TJA-NY-COHOCTON SOLAR FARM, LLC

11190 NY 371
COHOCTON, NY


LAT: 42.54452 LONG: -77.46018

MARK	DATE	DESCRIPTION
1	6-24-22	ISSUED FOR PERMITTING
REVISIONS		
PROJECT NO: U41.062.001		
DATE: APRIL 2022		
DRAWN BY: M. BUCKINGHAM		
DESIGNED BY: E.N. KENNA P.E.		
CHECKED BY: J.L. ROBBINS P.E.		
NO ALTERATION PERMITTED HEREON EXCEPT AS PROVIDED UNDER SECTION 7209 SUBDIVISION 2 OF THE NEW YORK EDUCATION LAW		

PLAN AND
PROFILES


C-106

Nov 08, 2023 - 3:28pm
F:\Project\A87 - Prister Energy\A87_009.001 - Cohocton\Design\CADD\Civil Drawings\A87_009.001_C-107.dwg

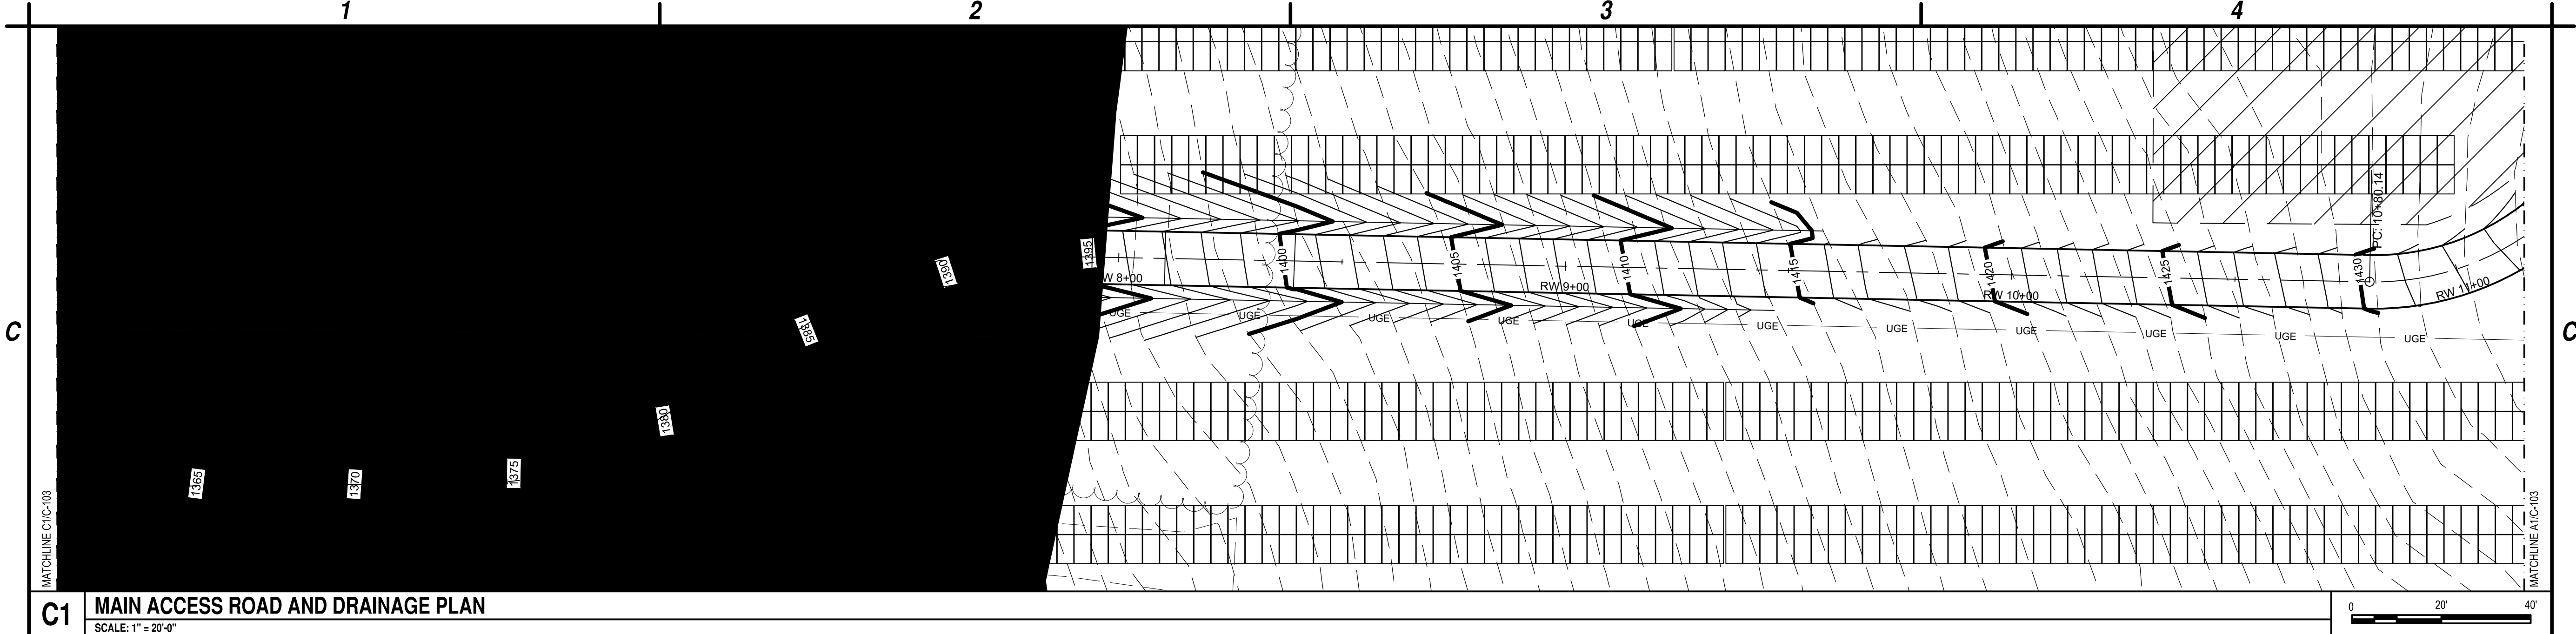

C1 MAIN ACCESS ROAD AND DRAINAGE PLAN
SCALE: 1" = 20'-0"

MAIN ACCESS ROAD PROFILE

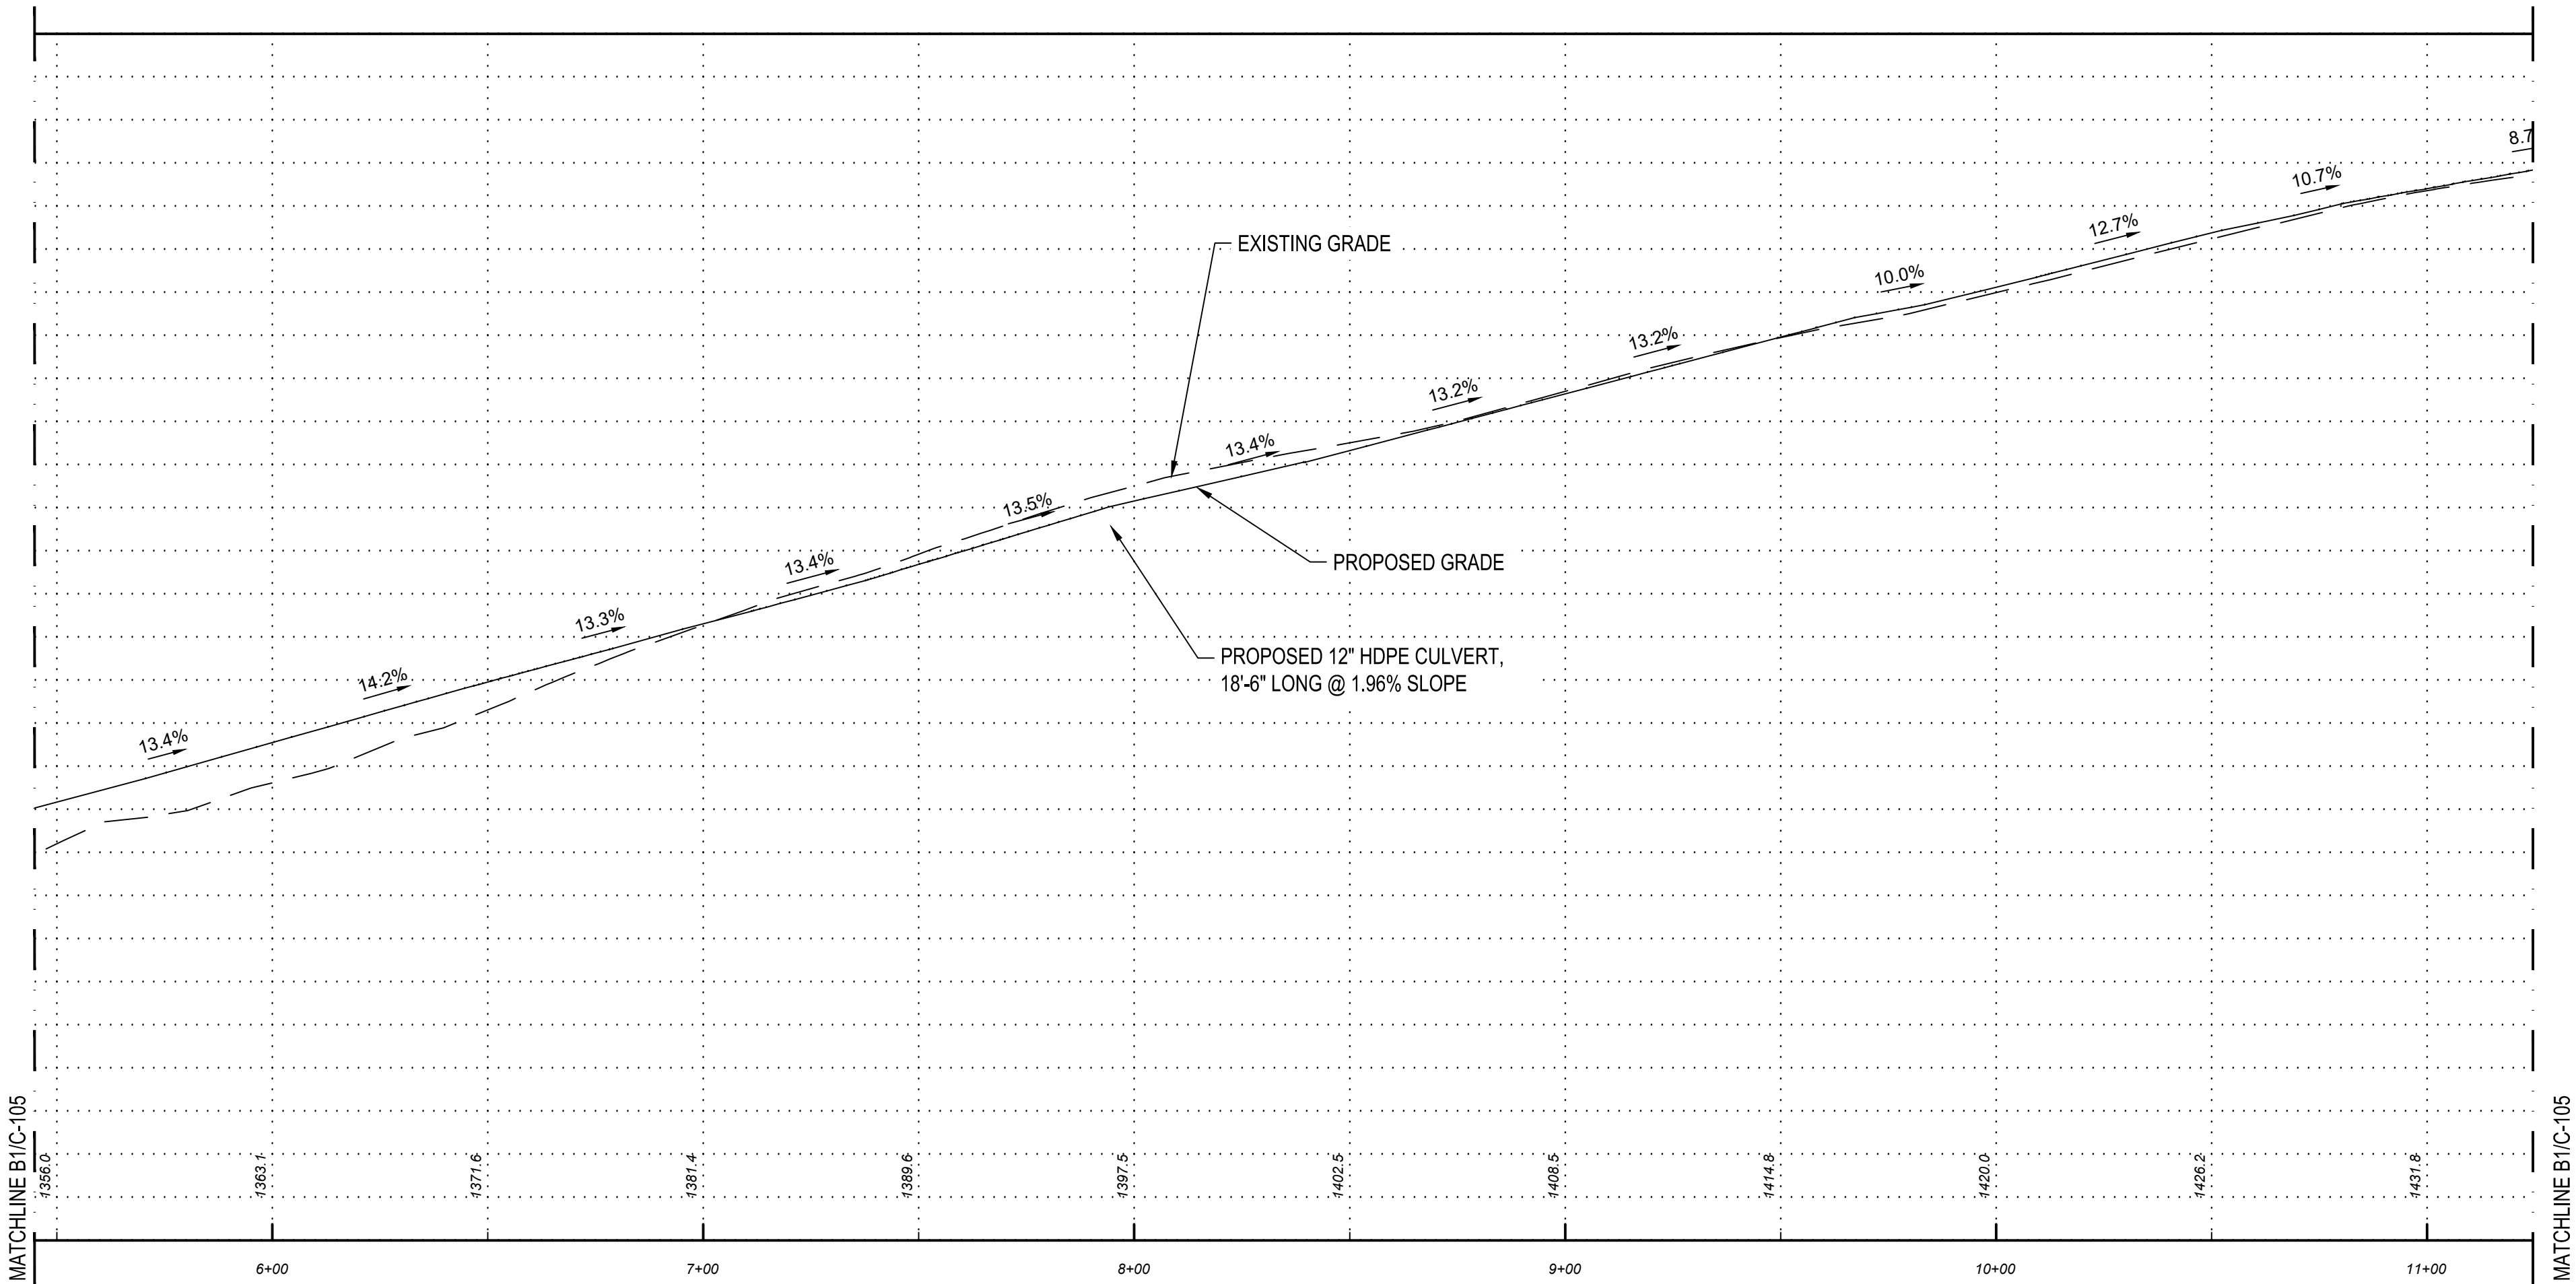

A1 MAIN ACCESS ROAD PROFILE
HORIZONTAL SCALE: 1" = 30'-0" VERTICAL SCALE: 1" = 15'-0"



C&S Engineers, Inc.
499 Col. Eileen Collins Blvd.
Syracuse, New York 13212
Phone: 315-455-2000
Fax: 315-455-9667
www.cscos.com



TJA-NY-COHOCTON SOLAR FARM, LLC

11190 NY 371
COHOCTON, NY


LAT: 42.54452 LONG: -77.46018

MARK	DATE	DESCRIPTION
1	6-24-22	ISSUED FOR PERMITTING
REVISIONS		
PROJECT NO: U41.062.001		
DATE: APRIL 2022		
DRAWN BY: M. BUCKINGHAM		
DESIGNED BY: E.N. KENNA P.E.		
CHECKED BY: J.L. ROBBINS P.E.		
NO ALTERATION PERMITTED HEREON EXCEPT AS PROVIDED UNDER SECTION 7209 SUBDIVISION 2 OF THE NEW YORK EDUCATION LAW		

PLAN AND
PROFILE

C-107



Nov 08, 2023 - 3:39pm
F:\Project\A87 - Prister Energy\A87 - Cohocton\Design\CADD\Civil Drawings\A87.009.001_C-108.dwg

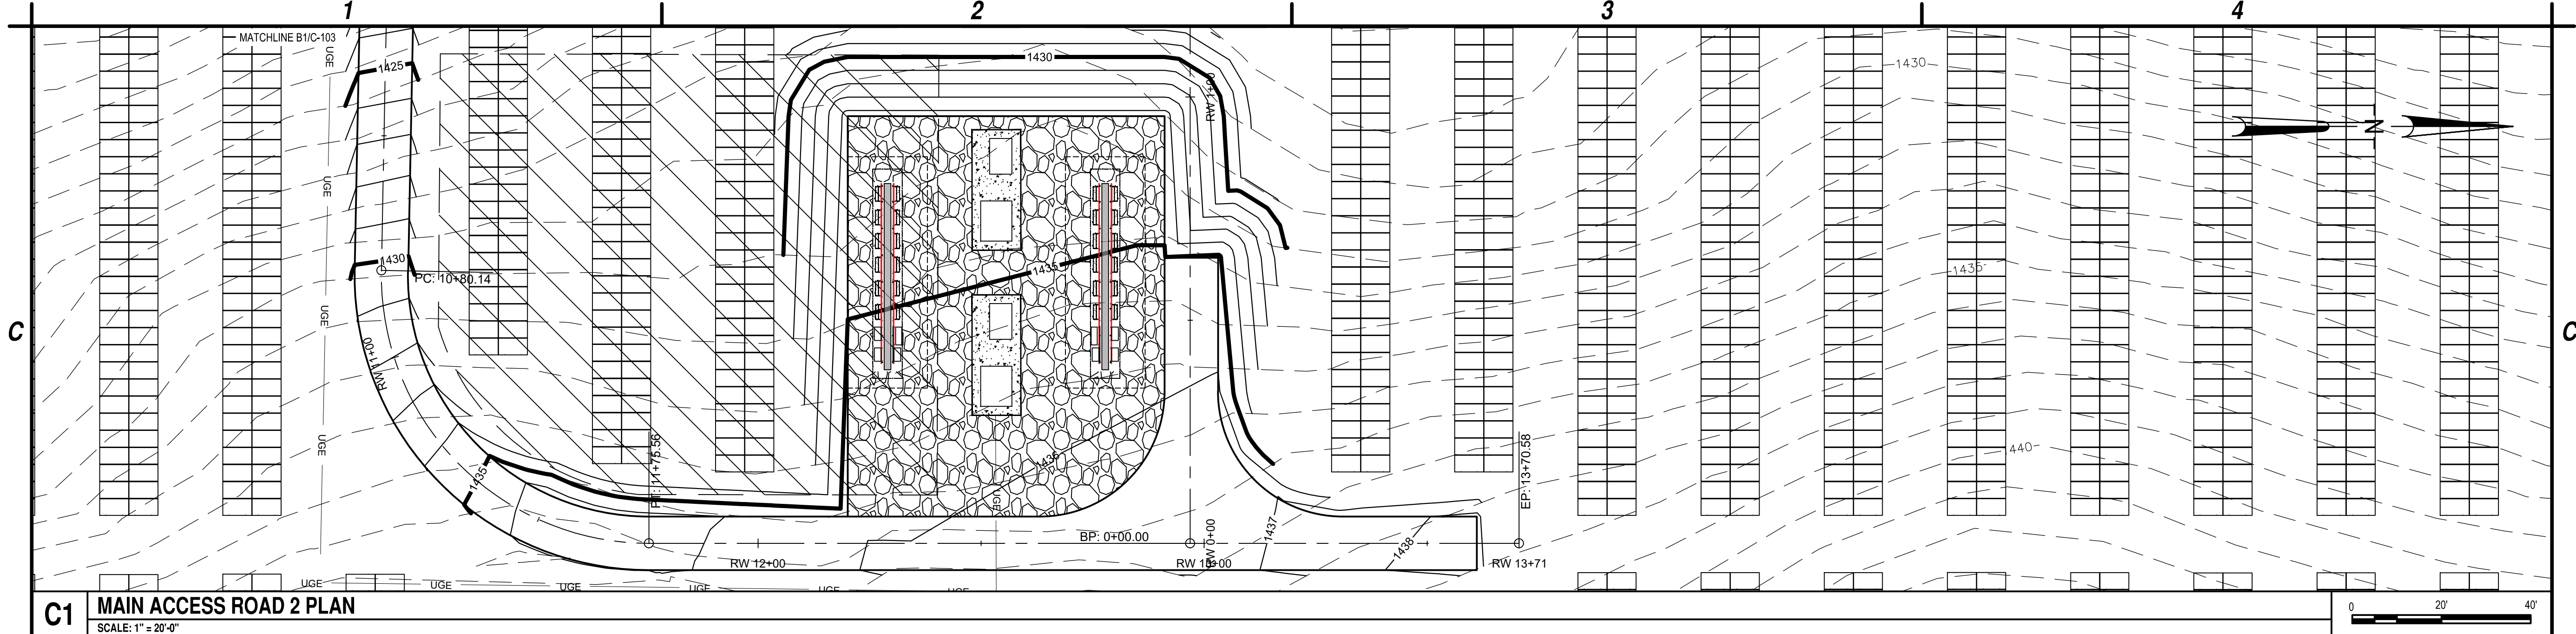

B

A


A1 MAIN ACCESS ROAD PROFILE
HORIZONTAL SCALE: 1" = 30'-0" VERTICAL SCALE: 1" = 15'-0"

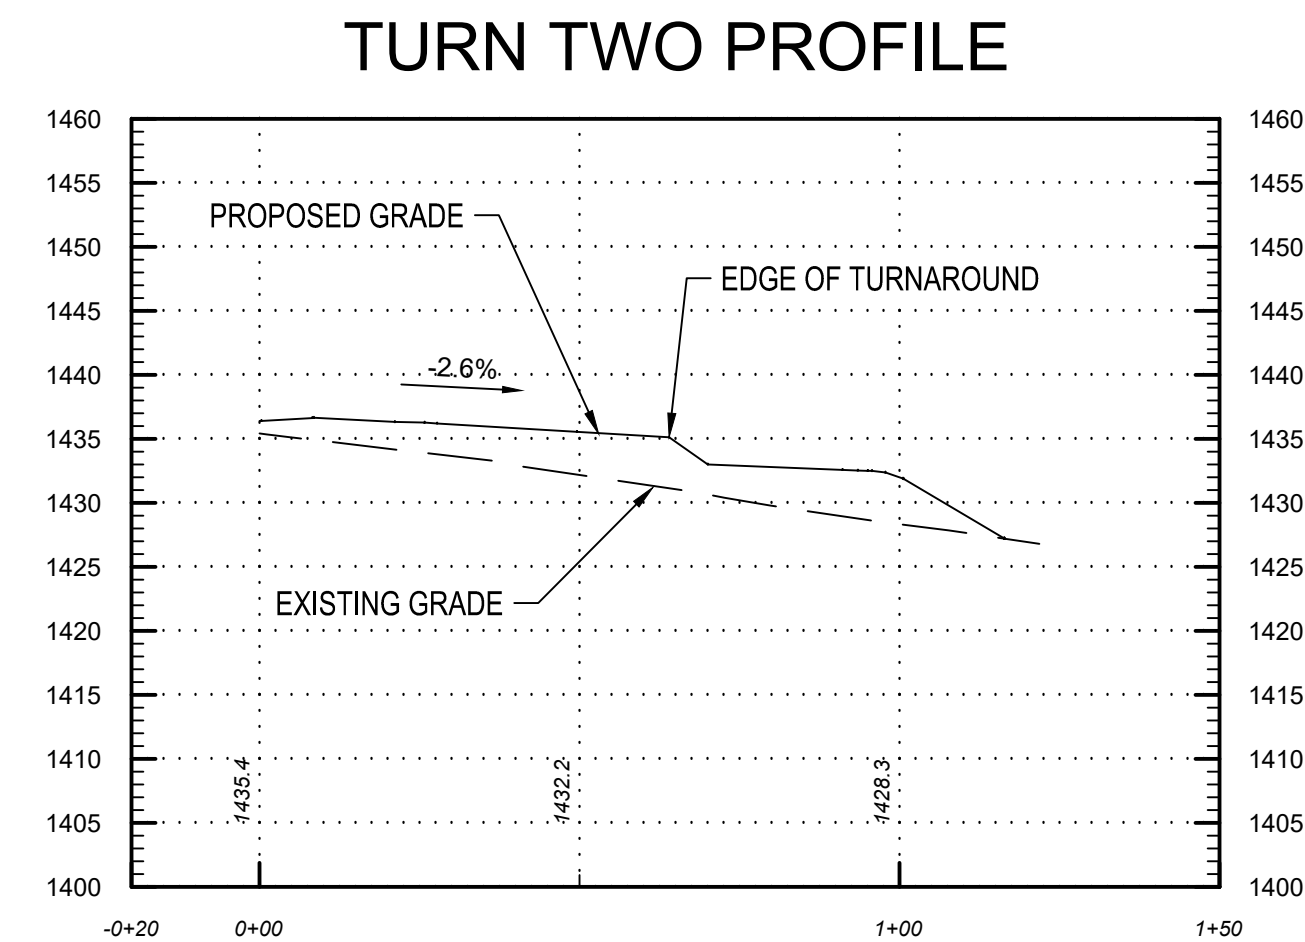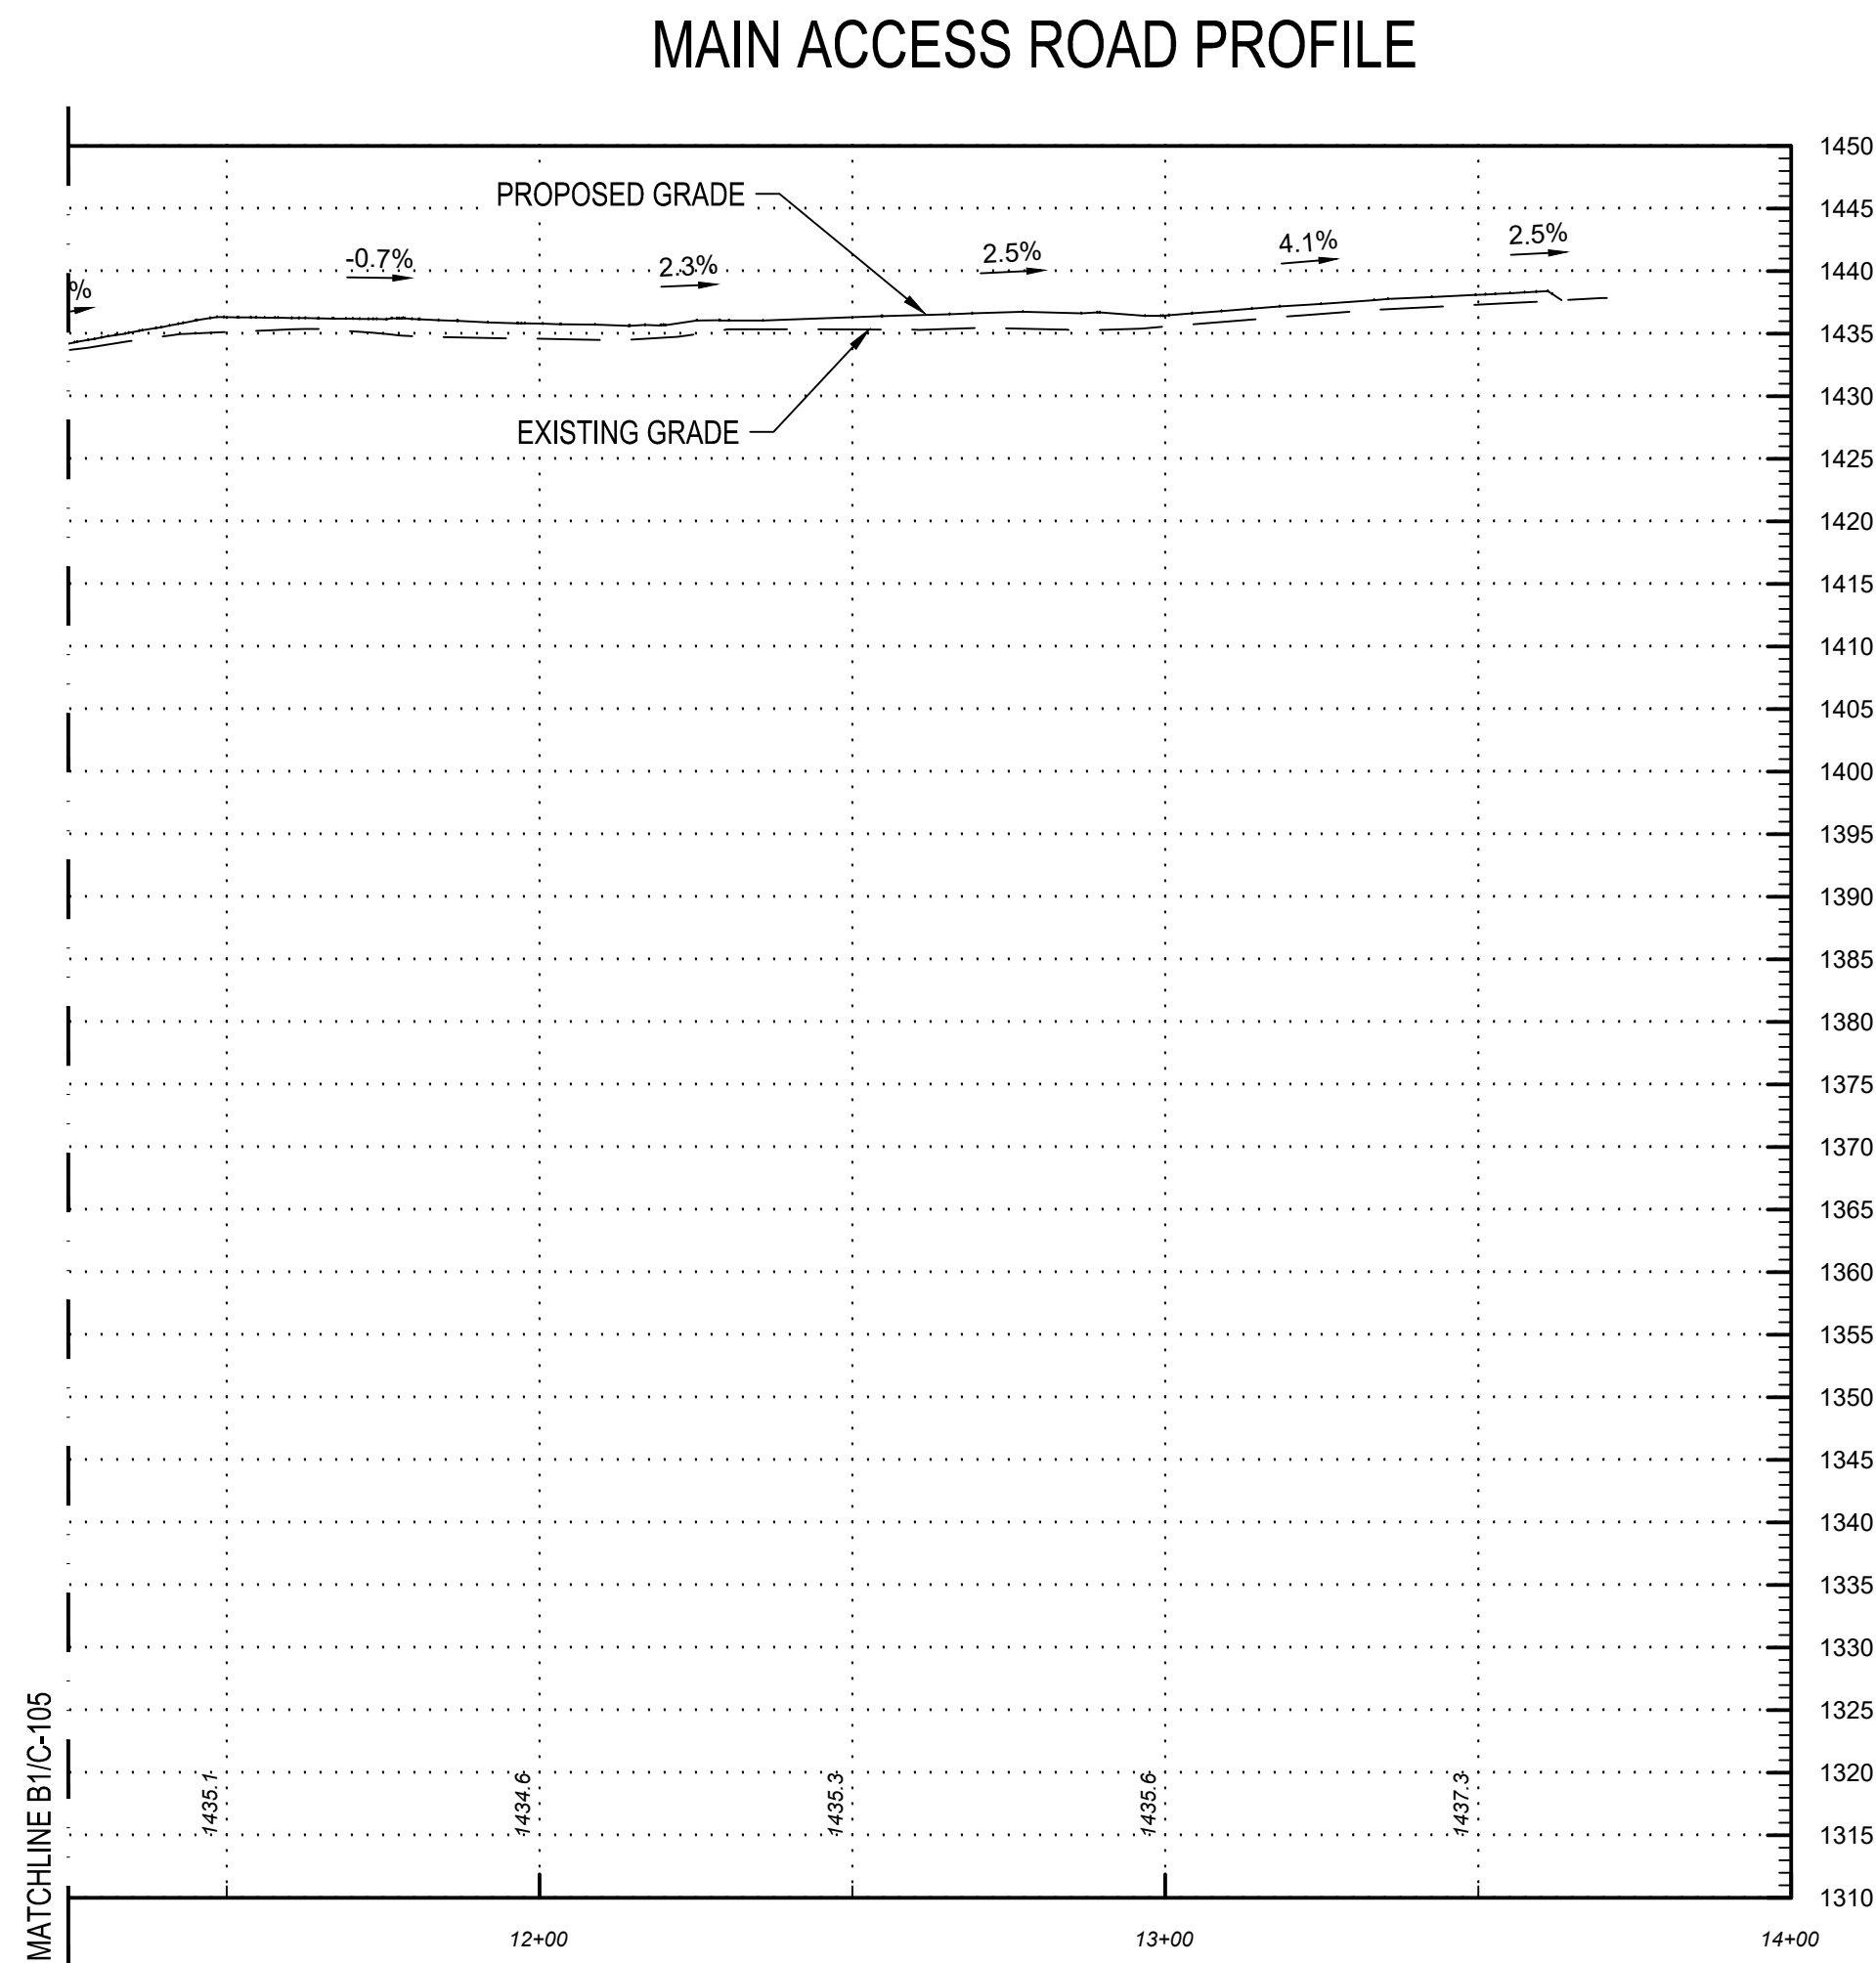

A4 TURN TWO PROFILE
HORIZONTAL SCALE: 1" = 30'-0" VERTICAL SCALE: 1" = 15'-0"



C&S Engineers, Inc.
499 Col. Eileen Collins Blvd.
Syracuse, New York 13212
Phone: 315-455-2000
Fax: 315-455-9667
www.cscos.com

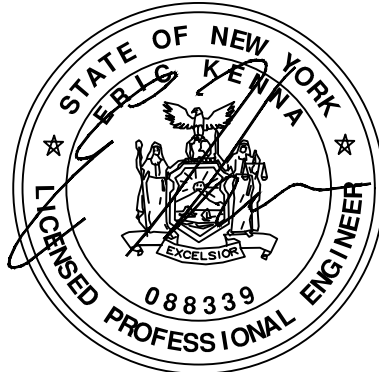


TJA-NY-COHOCTON SOLAR FARM, LLC
11190 NY 371
COHOCTON, NY
LAT: 42.54452 LONG: -77.46018

MARK	DATE	DESCRIPTION
1	6-24-22	ISSUED FOR PERMITTING
REVISIONS		
PROJECT NO: U41.062.001		
DATE: APRIL 2022		
DRAWN BY: M. BUCKINGHAM		
DESIGNED BY: E.N. KENNA P.E.		
CHECKED BY: J.L. ROBBINS P.E.		
NO ALTERATION PERMITTED HEREON EXCEPT AS PROVIDED UNDER SECTION 7209 SUBDIVISION 2 OF THE NEW YORK EDUCATION LAW		

PLAN AND PROFILES

C-108

Nov 08, 2023 3:41pm F:\Project\A67 - Pfister Energy\A67.009.001 - Cohocton\Design\CADD\Civil Drawings\A67.009.001_C-109 Erosion & Sediment Control Plan.dwg

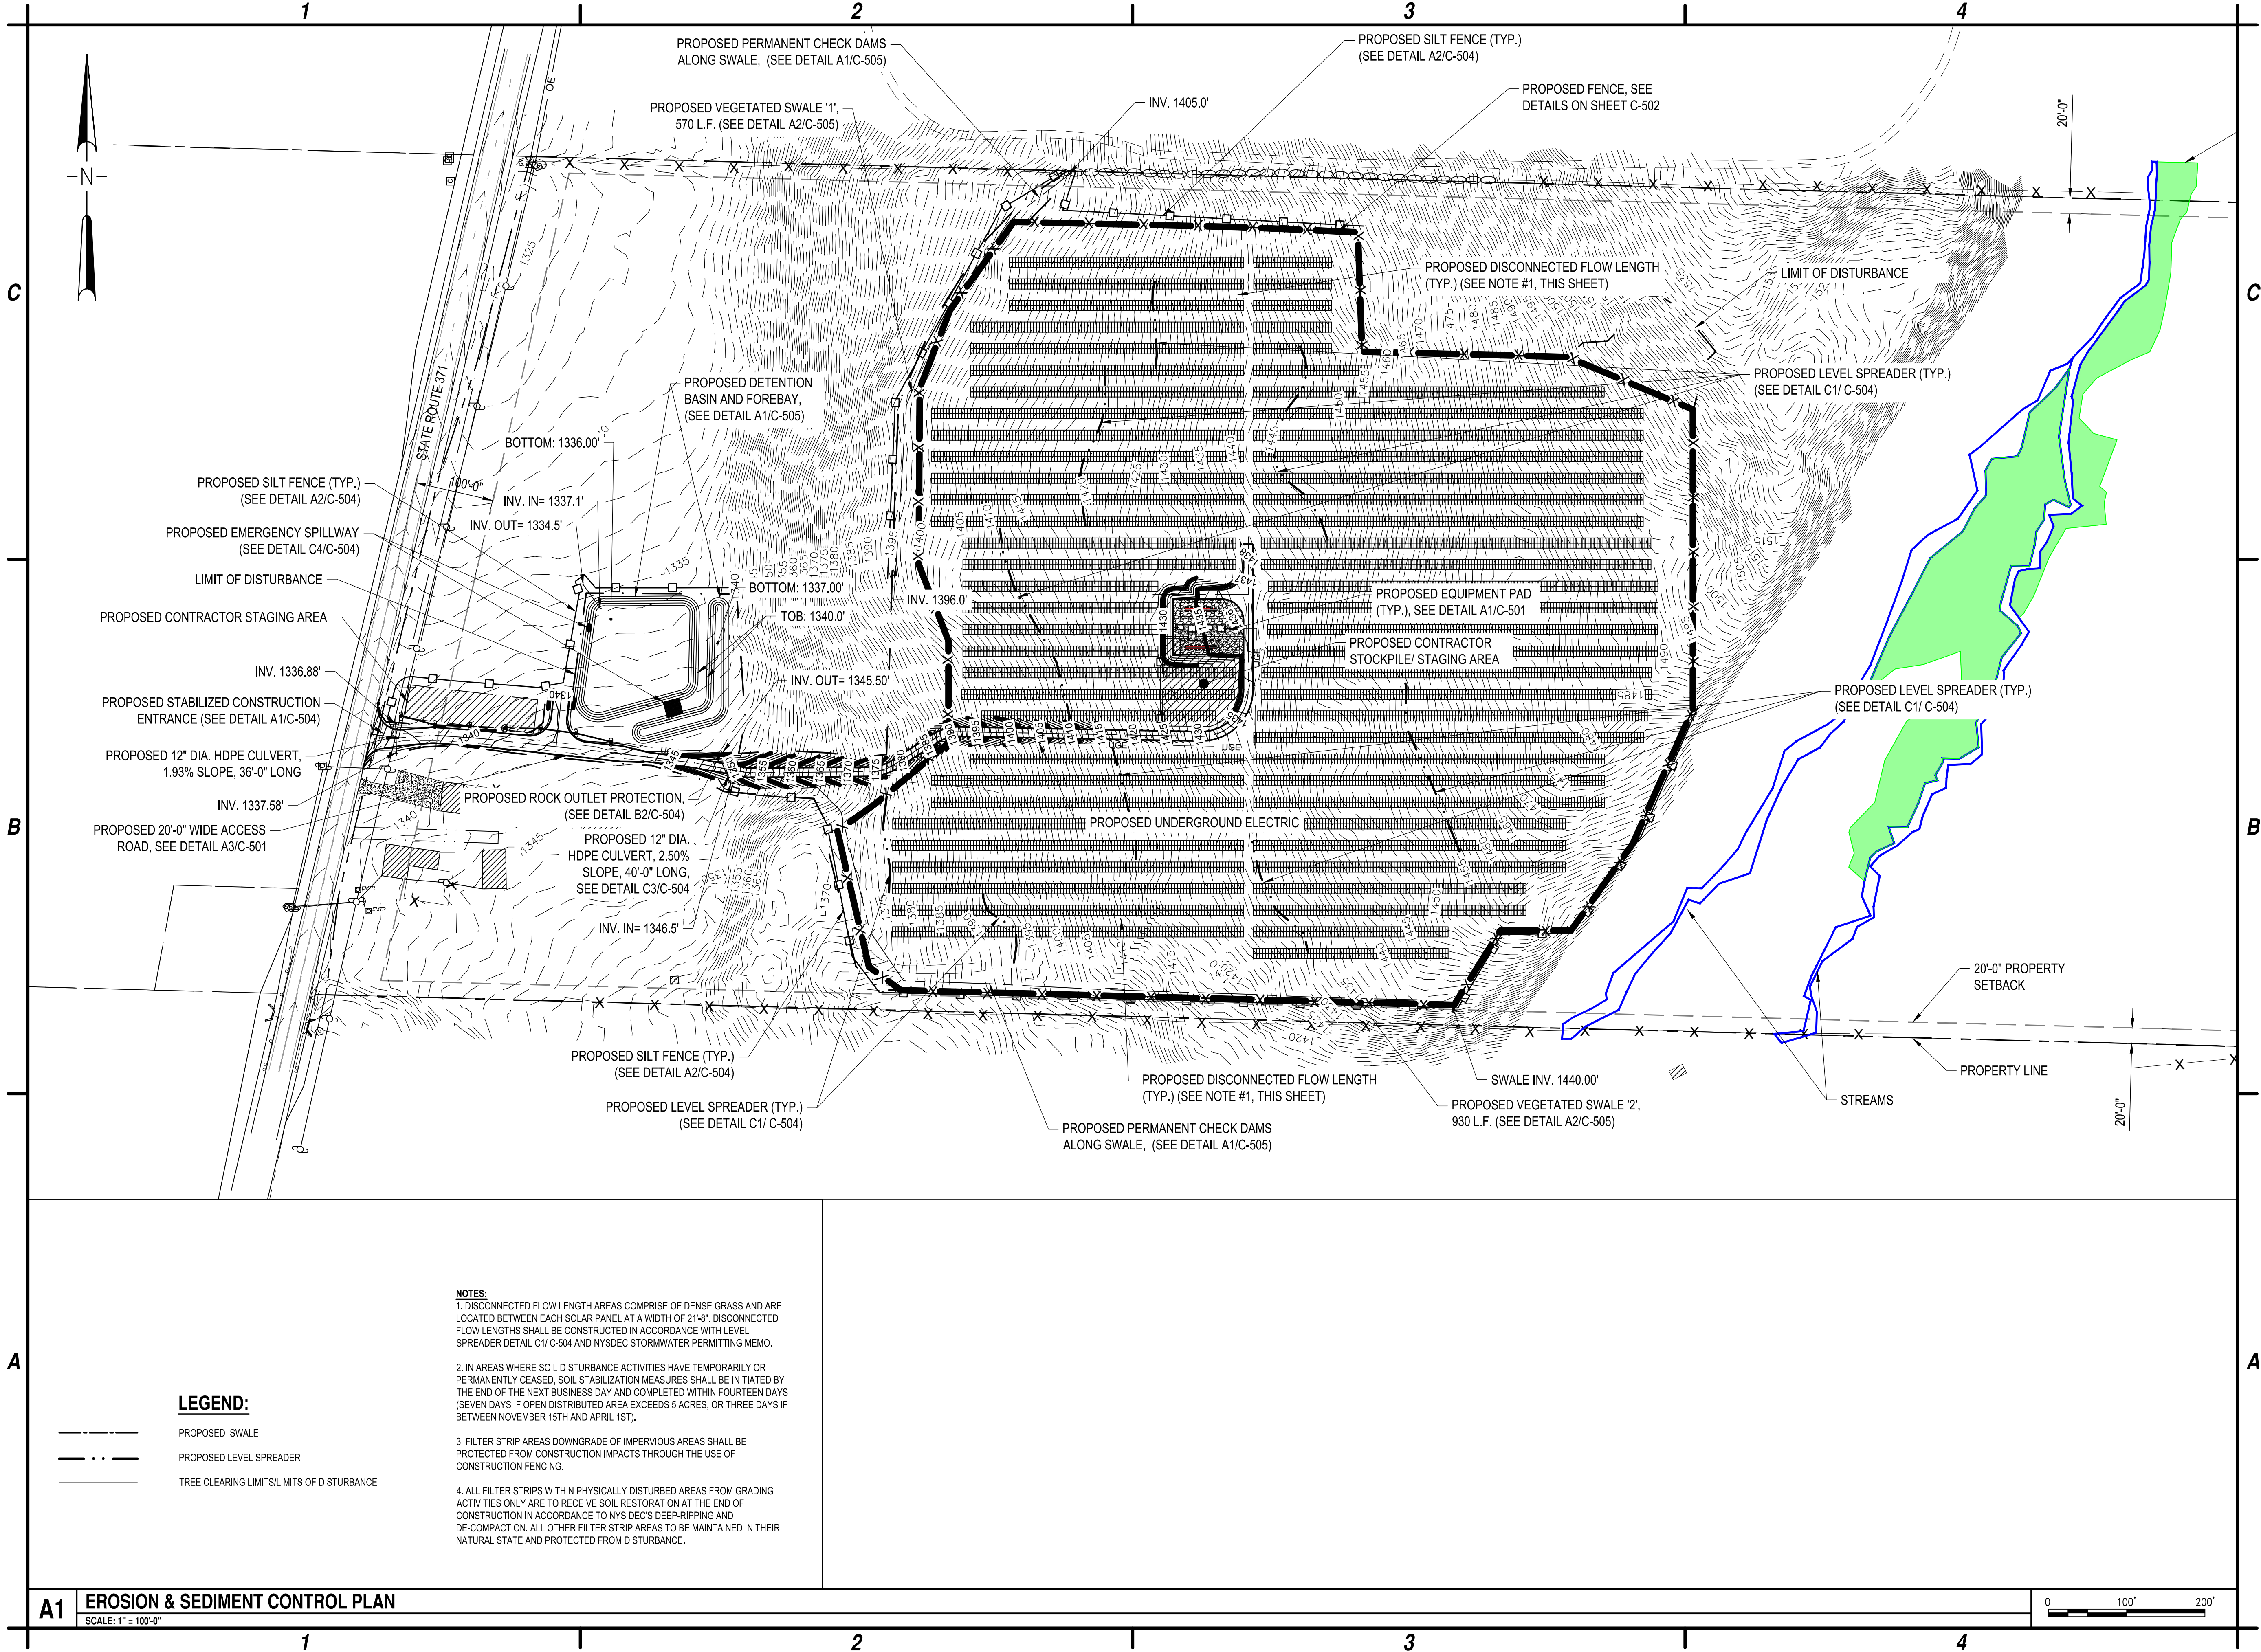

- NOTES:**
1. DISCONNECTED FLOW LENGTH AREAS COMPRISE OF DENSE GRASS AND ARE LOCATED BETWEEN EACH SOLAR PANEL AT A WIDTH OF 2'-18". DISCONNECTED FLOW LENGTHS SHALL BE CONSTRUCTED IN ACCORDANCE WITH LEVEL SPREADER DETAIL C1/ C-504 AND NYSDEC STORMWATER PERMITTING MEMO.
 2. IN AREAS WHERE SOIL DISTURBANCE ACTIVITIES HAVE TEMPORARILY OR PERMANENTLY CEASED, SOIL STABILIZATION MEASURES SHALL BE INITIATED BY THE END OF THE NEXT BUSINESS DAY AND COMPLETED WITHIN FOURTEEN DAYS (SEVEN DAYS IF OPEN DISTRIBUTED AREA EXCEEDS 5 ACRES, OR THREE DAYS IF BETWEEN NOVEMBER 1STH AND APRIL 1ST).
 3. FILTER STRIP AREAS DOWNGRADE OF IMPERVIOUS AREAS SHALL BE PROTECTED FROM CONSTRUCTION IMPACTS THROUGH THE USE OF CONSTRUCTION FENCING.
 4. ALL FILTER STRIPS WITHIN PHYSICALLY DISTURBED AREAS FROM GRADING ACTIVITIES ONLY ARE TO RECEIVE SOIL RESTORATION AT THE END OF CONSTRUCTION IN ACCORDANCE TO NYS DEC'S DEEP-RIPPING AND DE-COMPACTION. ALL OTHER FILTER STRIP AREAS TO BE MAINTAINED IN THEIR NATURAL STATE AND PROTECTED FROM DISTURBANCE.

LEGEND:


- PROPOSED SWALE
- PROPOSED LEVEL SPREADER
- TREE CLEARING LIMITS/LIMITS OF DISTURBANCE

A1 EROSION & SEDIMENT CONTROL PLAN

SCALE: 1" = 100'-0"



C&S Engineers, Inc.
499 Col. Eileen Collins Blvd.
Syracuse, New York 13212
Phone: 315-455-2000
Fax: 315-455-9667
www.cscos.com

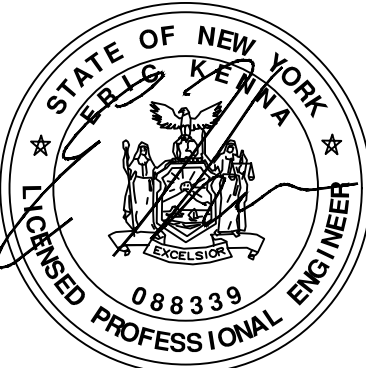

TJA-NY-COHOCTON SOLAR FARM, LLC

11190 NY 371

COHOCTON, NY



LAT: 42.54452 LONG: -77.46018

2	11-8-23	SITE LAYOUT
1	6-24-22	ISSUED FOR PERMITTING
MARK	DATE	DESCRIPTION
REVISIONS		
PROJECT NO: AB7.009.001		
DATE: JULY 2023		
DRAWN BY: M. BUCKINGHAM		
DESIGNED BY: E.N. KENNA P.E.		
CHECKED BY: J.L. ROBBINS P.E.		
NO ALTERATION PERMITTED HEREON EXCEPT AS PROVIDED UNDER SECTION 7209 SUBDIVISION 2 OF THE NEW YORK EDUCATION LAW		


EROSION & SEDIMENT CONTROL PLAN

C-109

Nov 08, 2023 - 3:42pm F:\Project\A67 - Pfister Energy\A67.009.001 - Cohocton\Design\CADD\Civil Drawings\A67.009.001_C-501.dwg

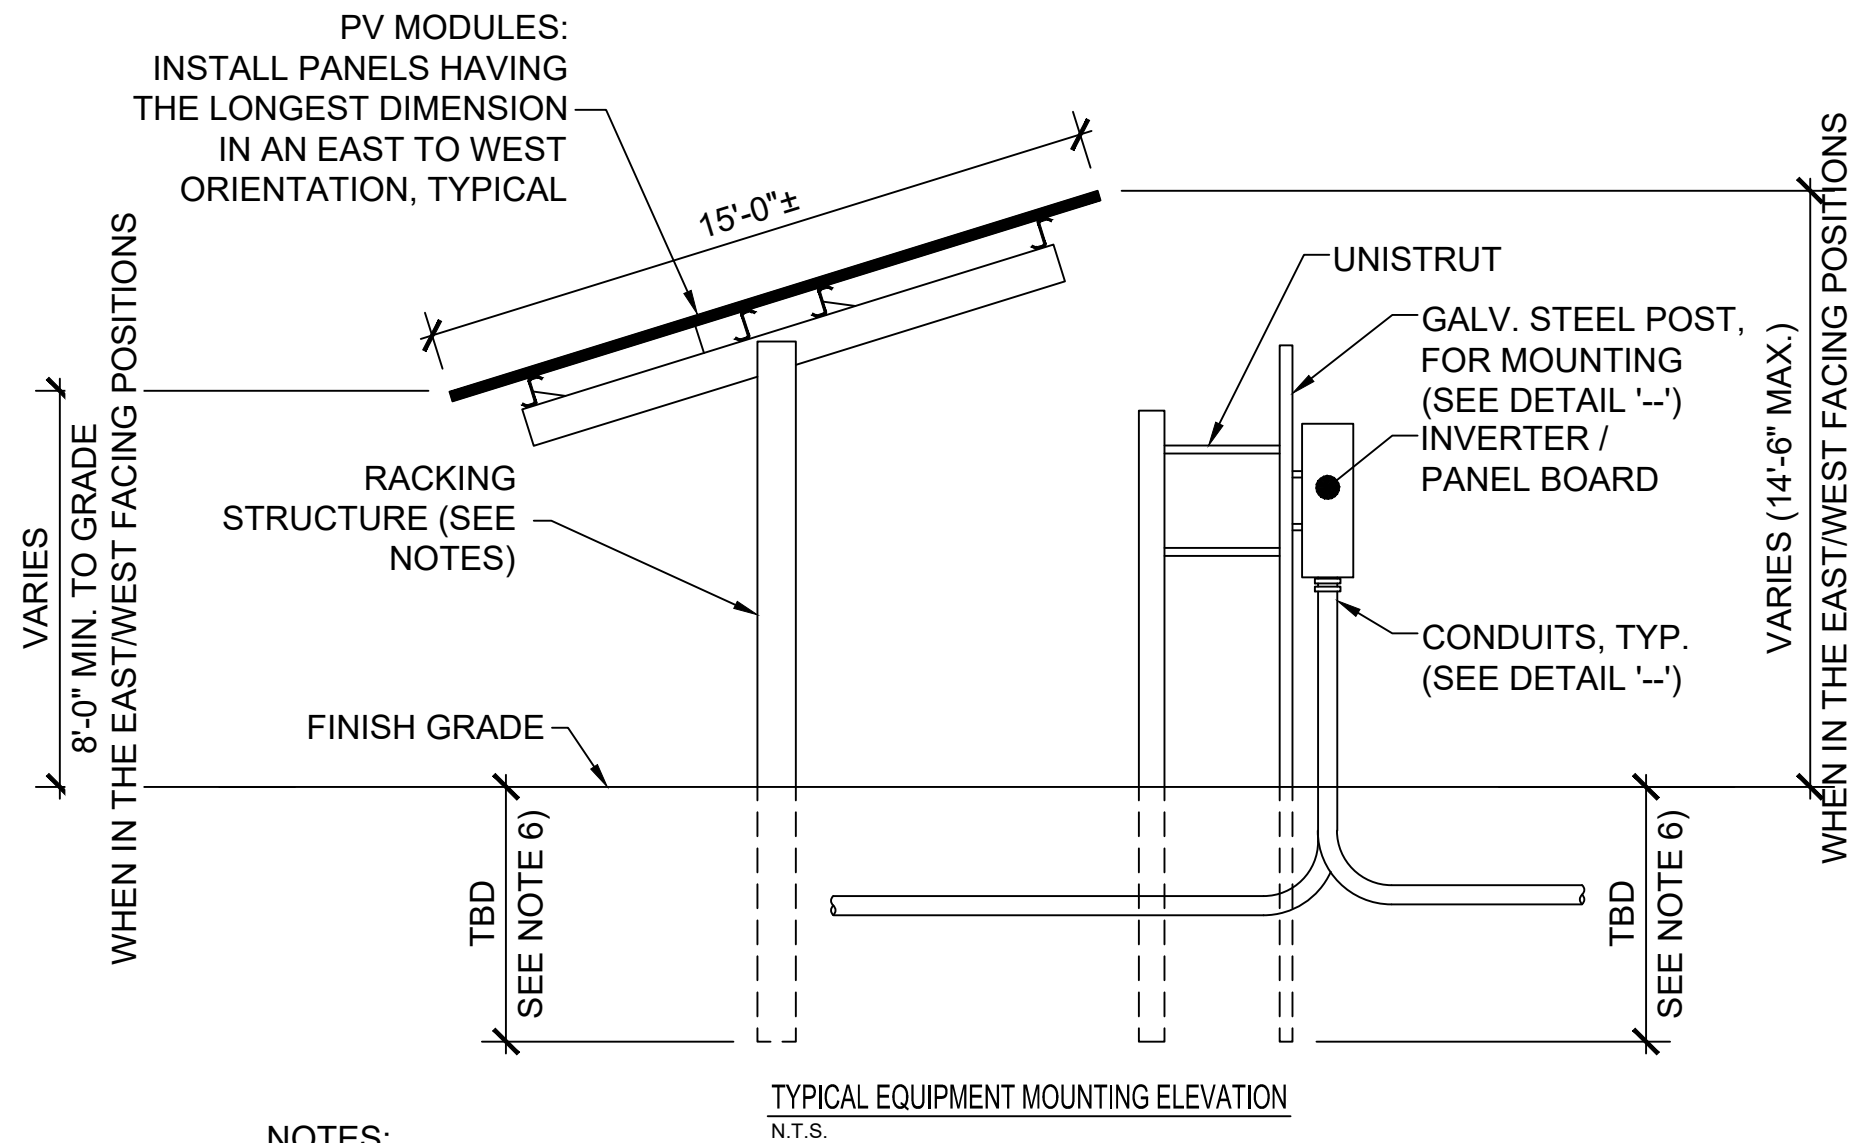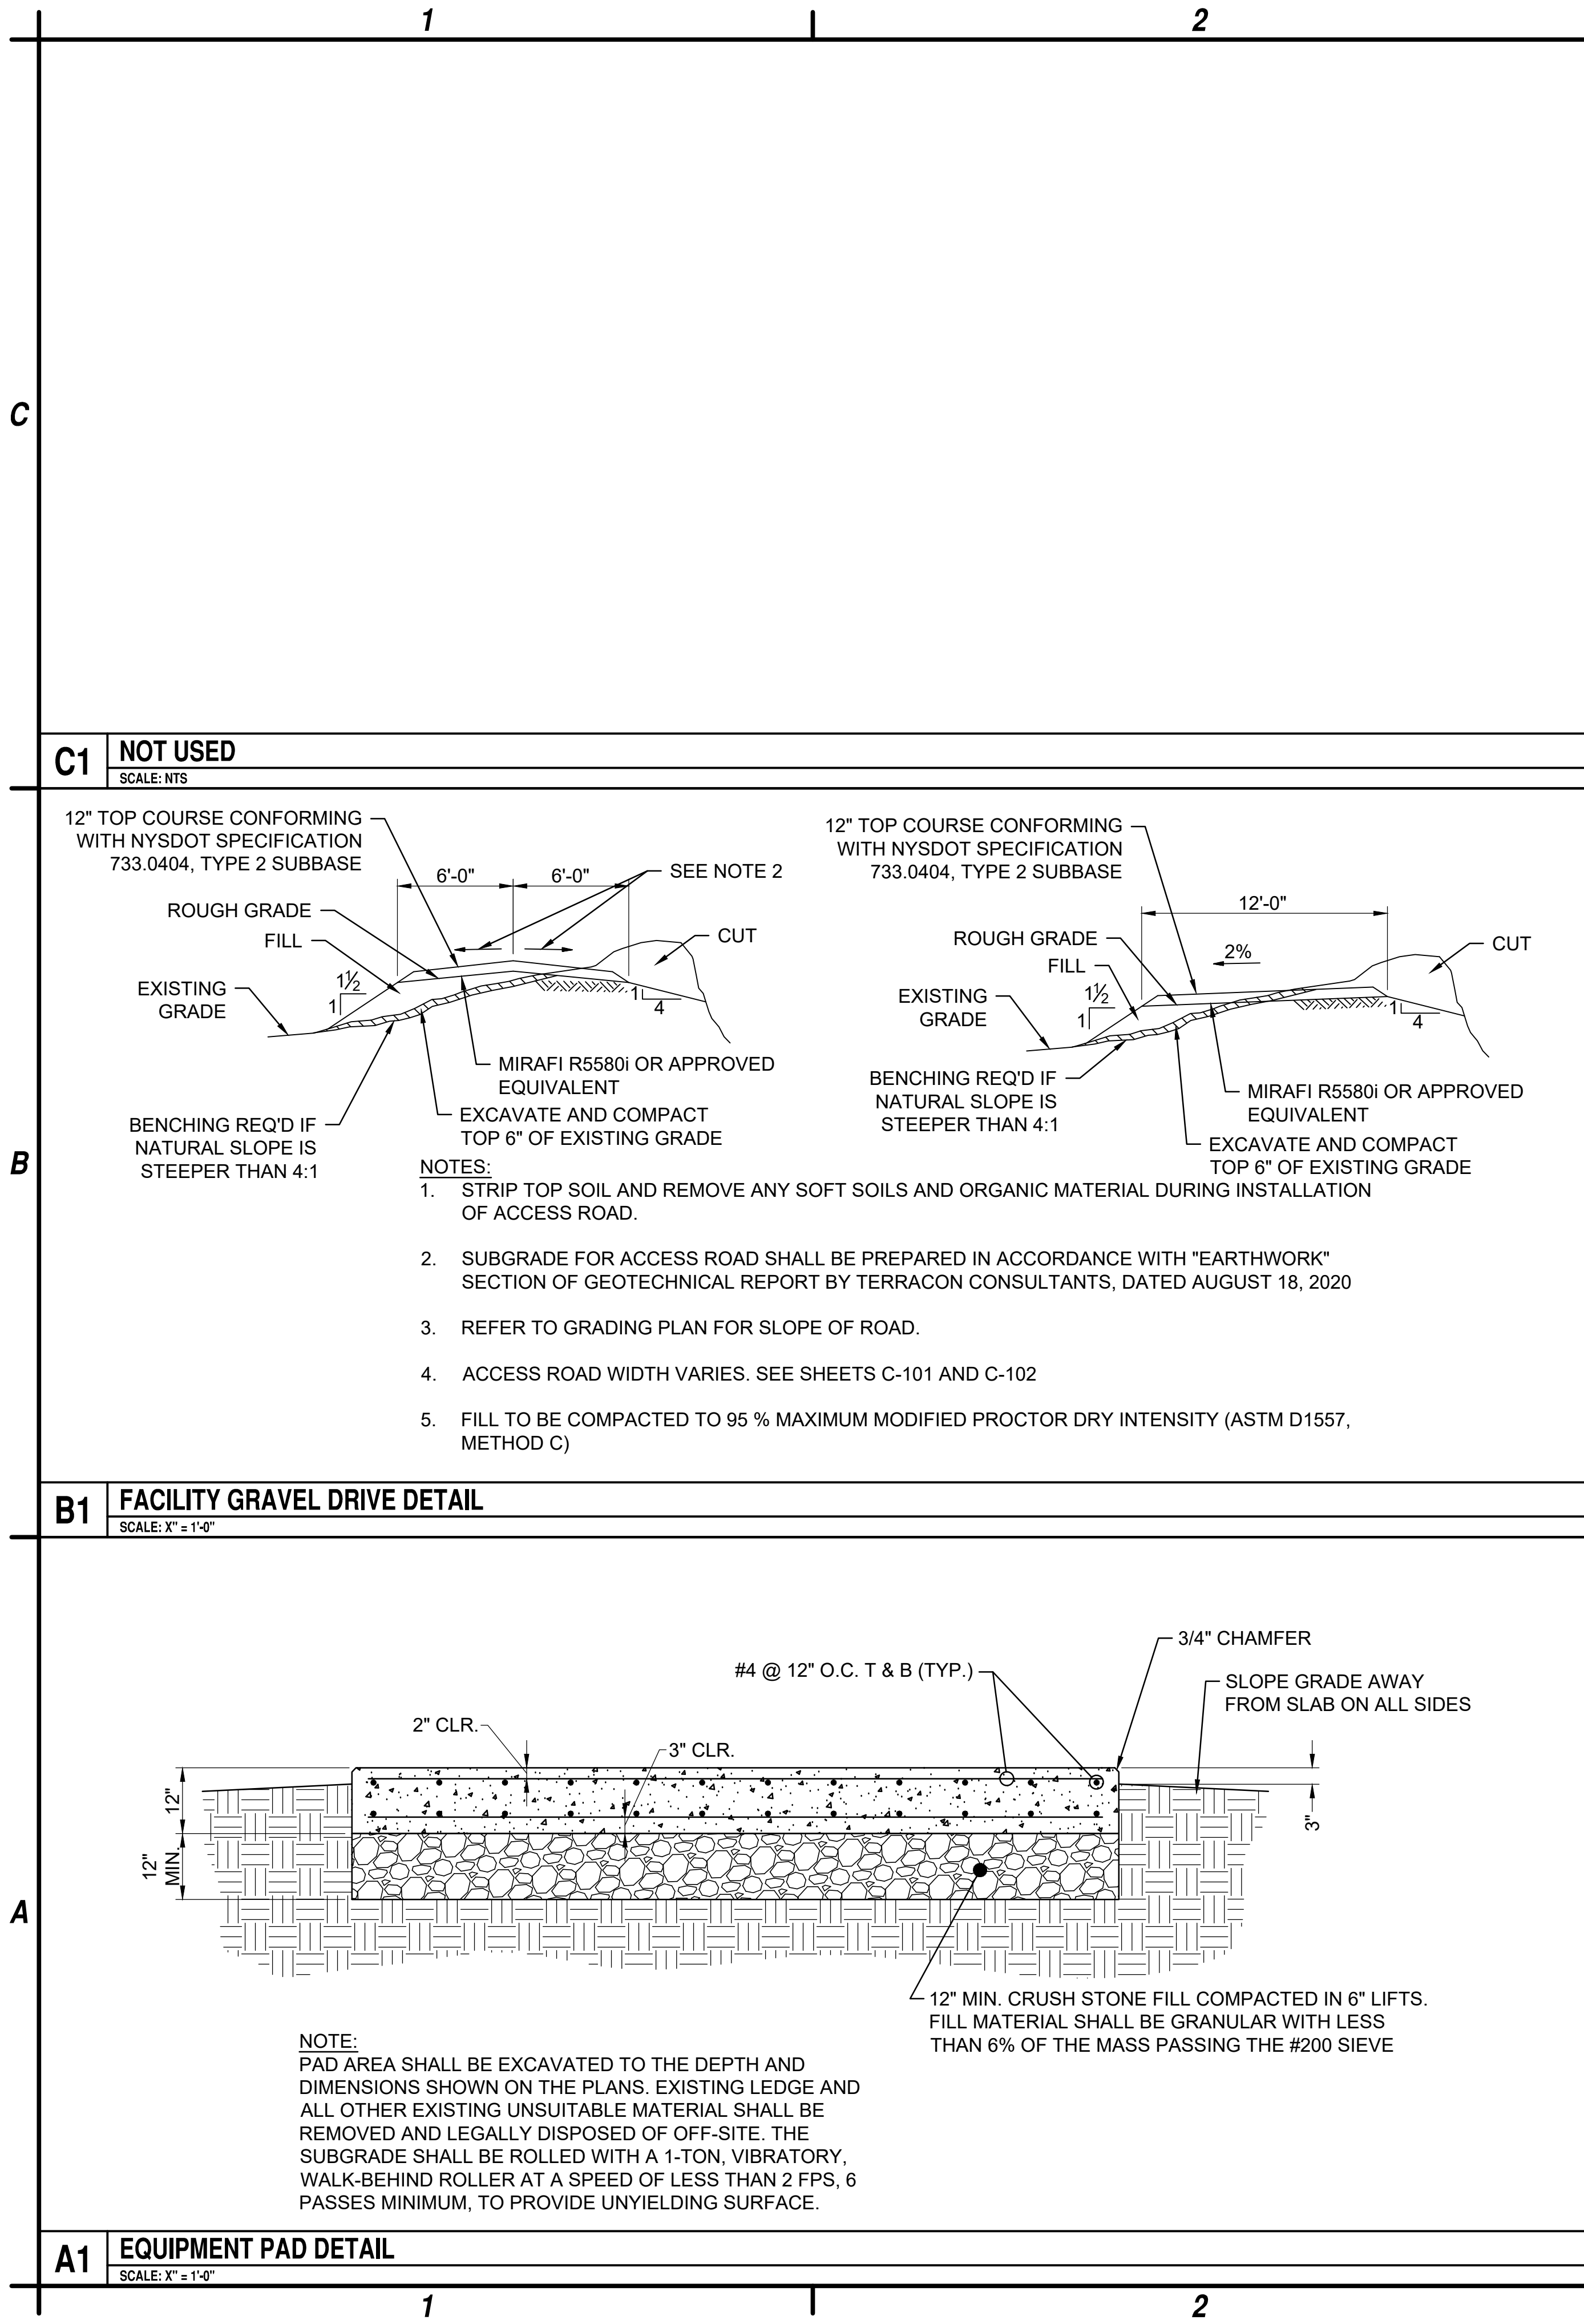

- NOTES:
- 1) ACTUAL HEIGHT OF THE RACKING SYSTEM AND OR DEPTH OF FOUNDATIONS ARE NOT PROVIDED. REFERENCE THE RACKING SYSTEM MANUFACTURER'S PRODUCT DATA AND INSTRUCTIONS FOR INFORMATION. RACKING STRUCTURE IS SHOWN AS REPRESENTATIVE ONLY.
 - 2) EQUIPMENT SHALL BE PROVIDED / MOUNTED SUCH THAT IT DOES NOT CAUSE ANY SHADING OF THE PHOTOVOLTAIC (PV) MODULES.
 - 3) CONDUITS SHALL BE ROUTED SUCH THAT CONFLICT WITH ARRAY FOUNDATIONS IS AVOIDED.
 - 4) ENCLOSURE SHALL BE MOUNTED SUCH THAT ALL CODE REQUIRED CLEARANCES ARE MET AND COMPLIED TO. (REFERENCE NEC ARTICLE 110.32)
 - 5) REFER TO RACKING MANUFACTURER'S MANUAL FOR ADDITIONAL INFORMATION.
 - 6) EMBEDMENT DEPTH VARIES, PER GEOTECHNICAL AND STRUCTURAL CALCULATION DETERMINATION.

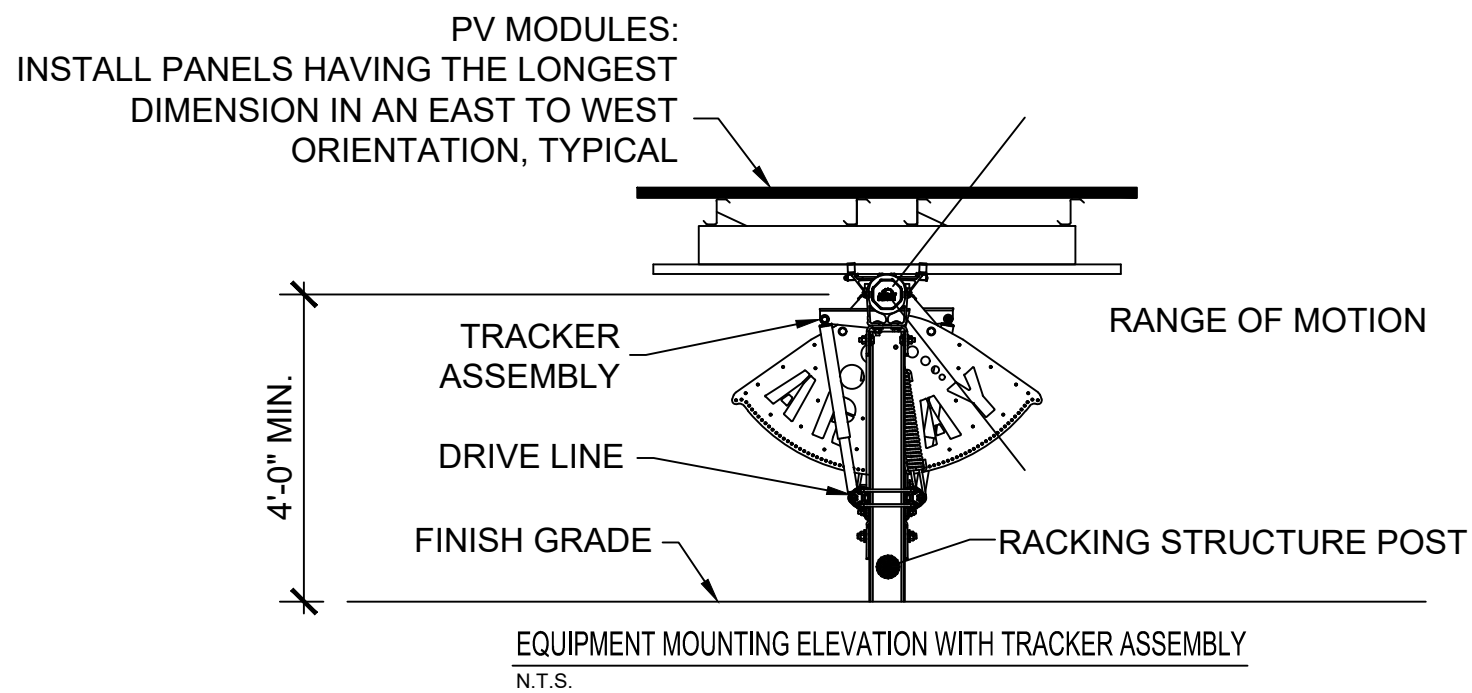

C&S Engineers, Inc.
499 Col. Eileen Collins Blvd.
Syracuse, New York 13212
Phone: 315-455-2000
Fax: 315-455-9667
www.cscos.com



TJA-NY-COHOCTON SOLAR FARM, LLC

11190 NY 371
COHOCTON, NY



LAT: 42.54452 LONG: -77.46018

2	11-8-23	SITE LAYOUT
1	6-24-22	ISSUED FOR PERMITTING
MARK	DATE	DESCRIPTION
REVISIONS		
PROJECT NO: AB7.009.001		
DATE: JULY 2023		
DRAWN BY: M. BUCKINGHAM		
DESIGNED BY:		
CHECKED BY: E.N. KENNA, P.E.		
NO ALTERATION PERMITTED HEREON EXCEPT AS PROVIDED UNDER SECTION 7209 SUBDIVISION 2 OF THE NEW YORK EDUCATION LAW		

SITE DETAILS


C-501

Nov 08, 2023 - 3:42pm F:\Project\AB7 - Pfister Energy\AB7.dwg - Cohocton\Design\CADD\Civil Drawings\AB7.dwg - C-502.dwg

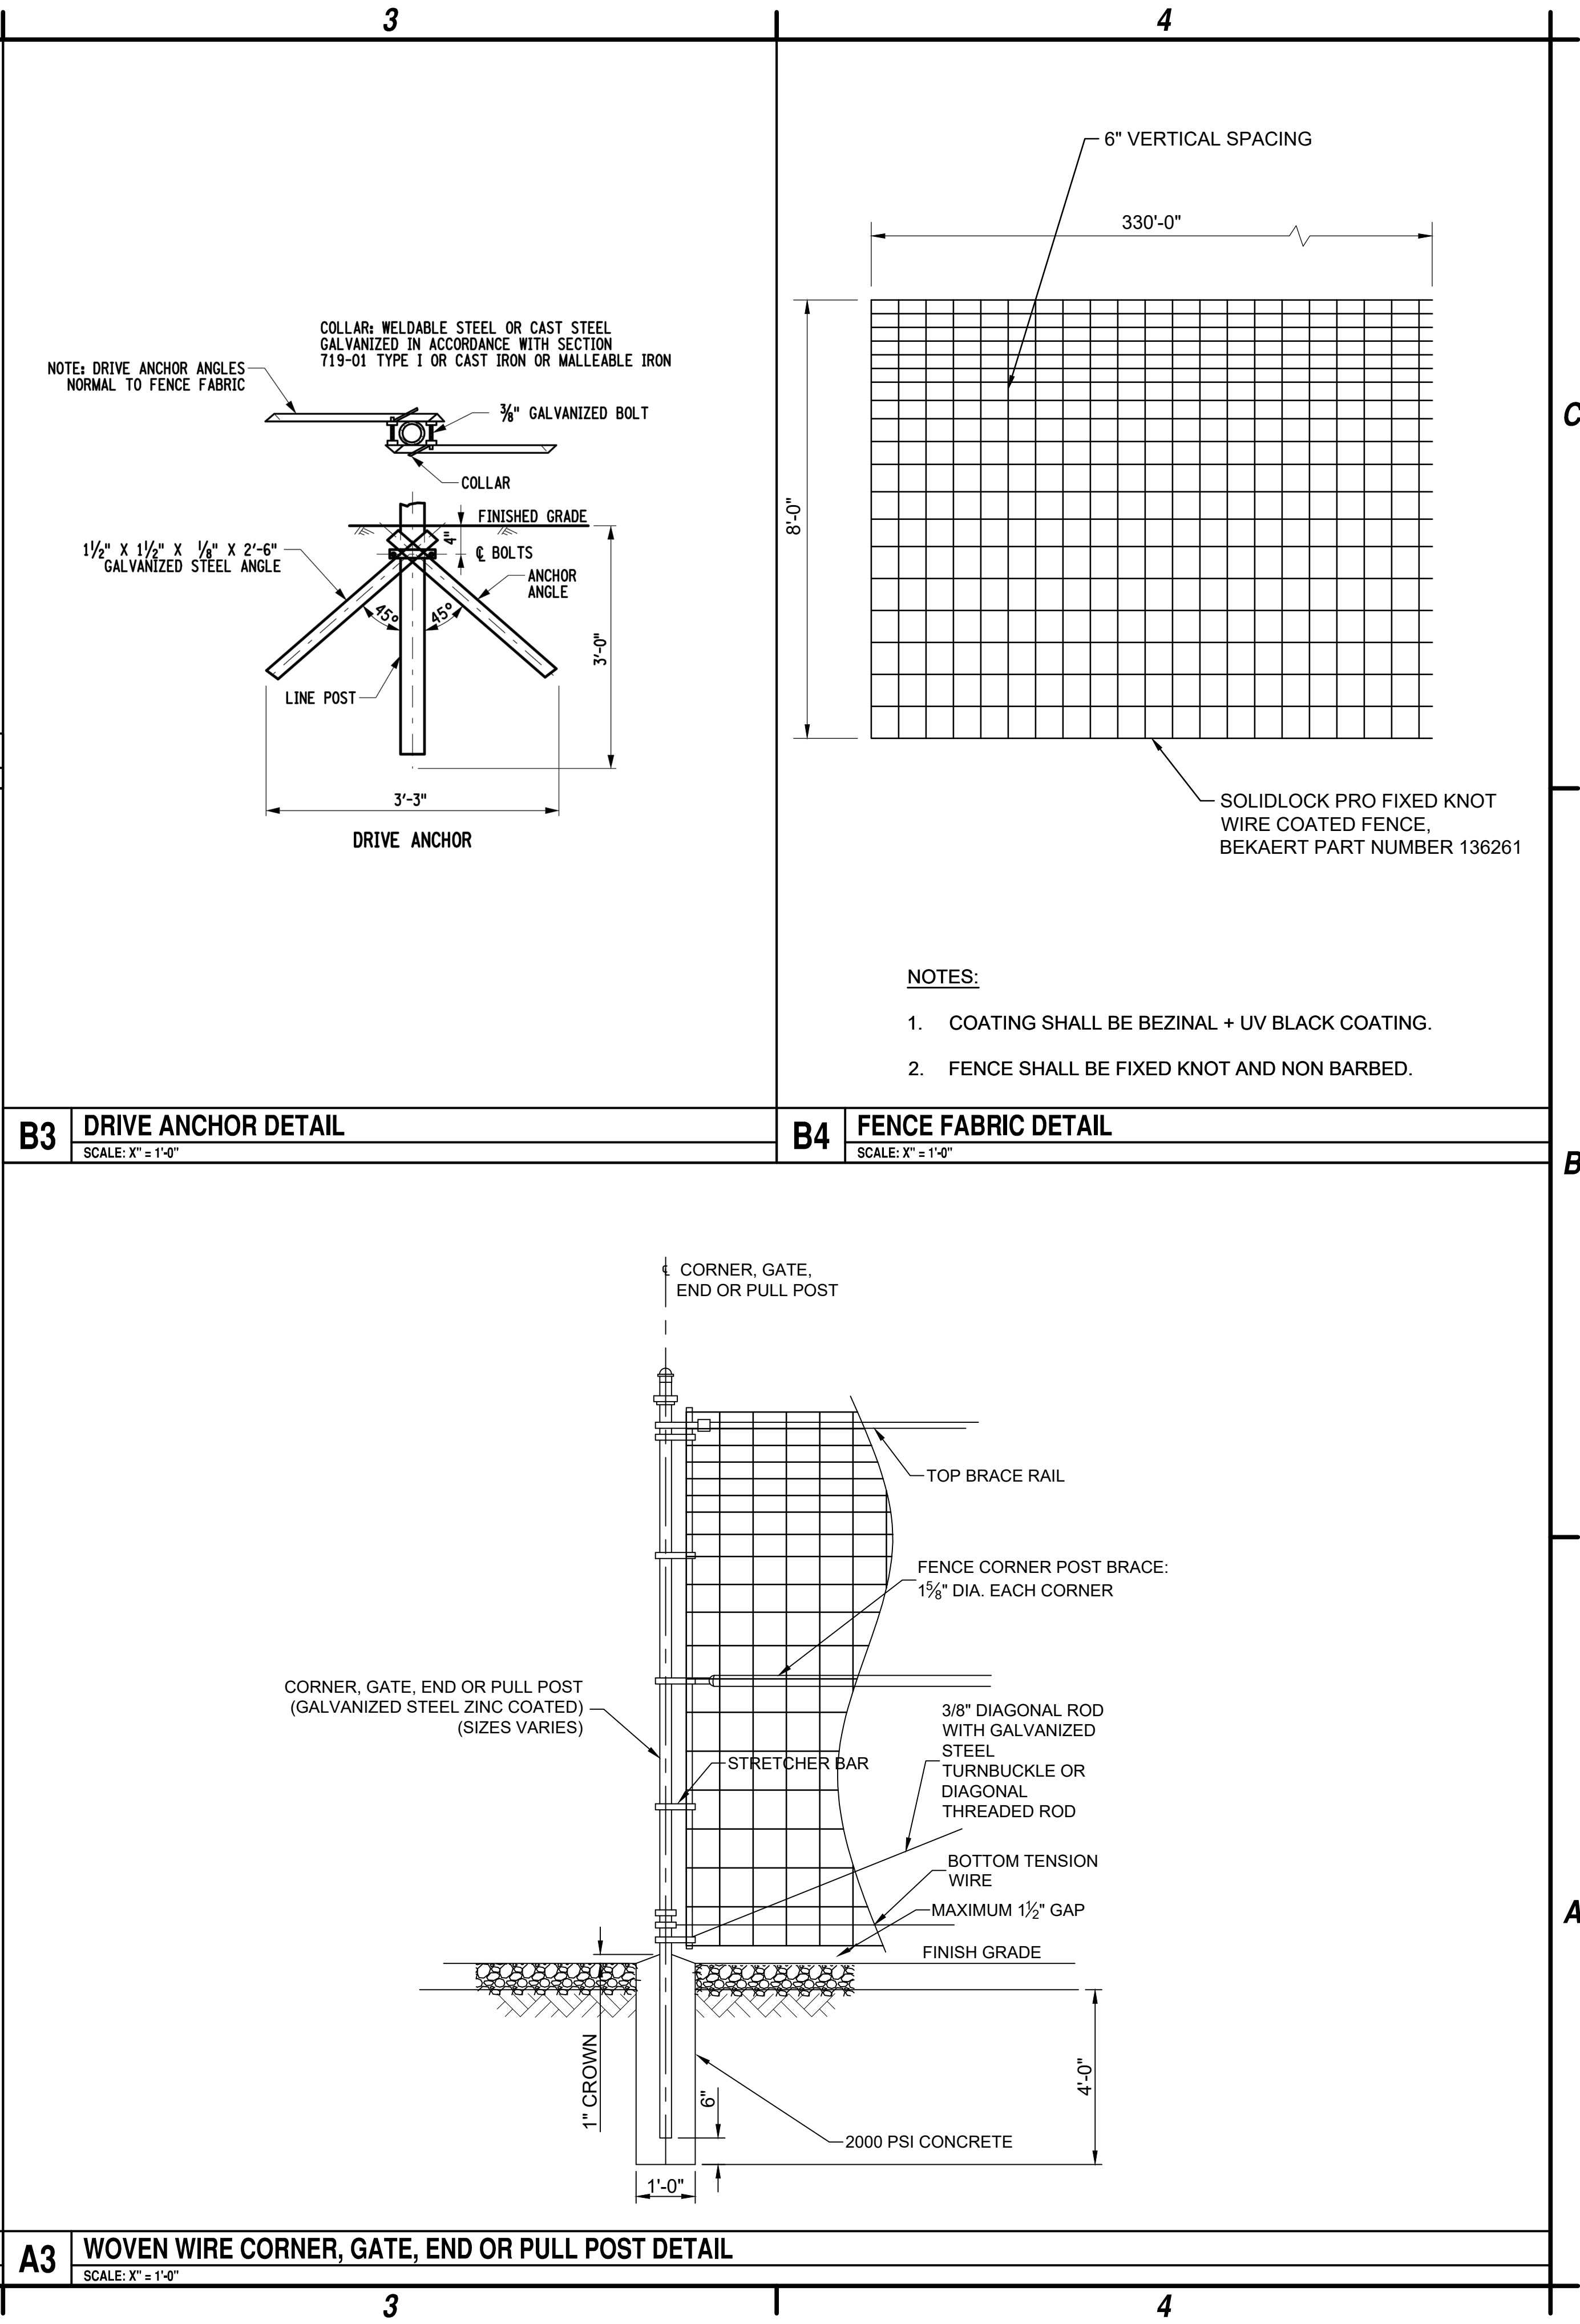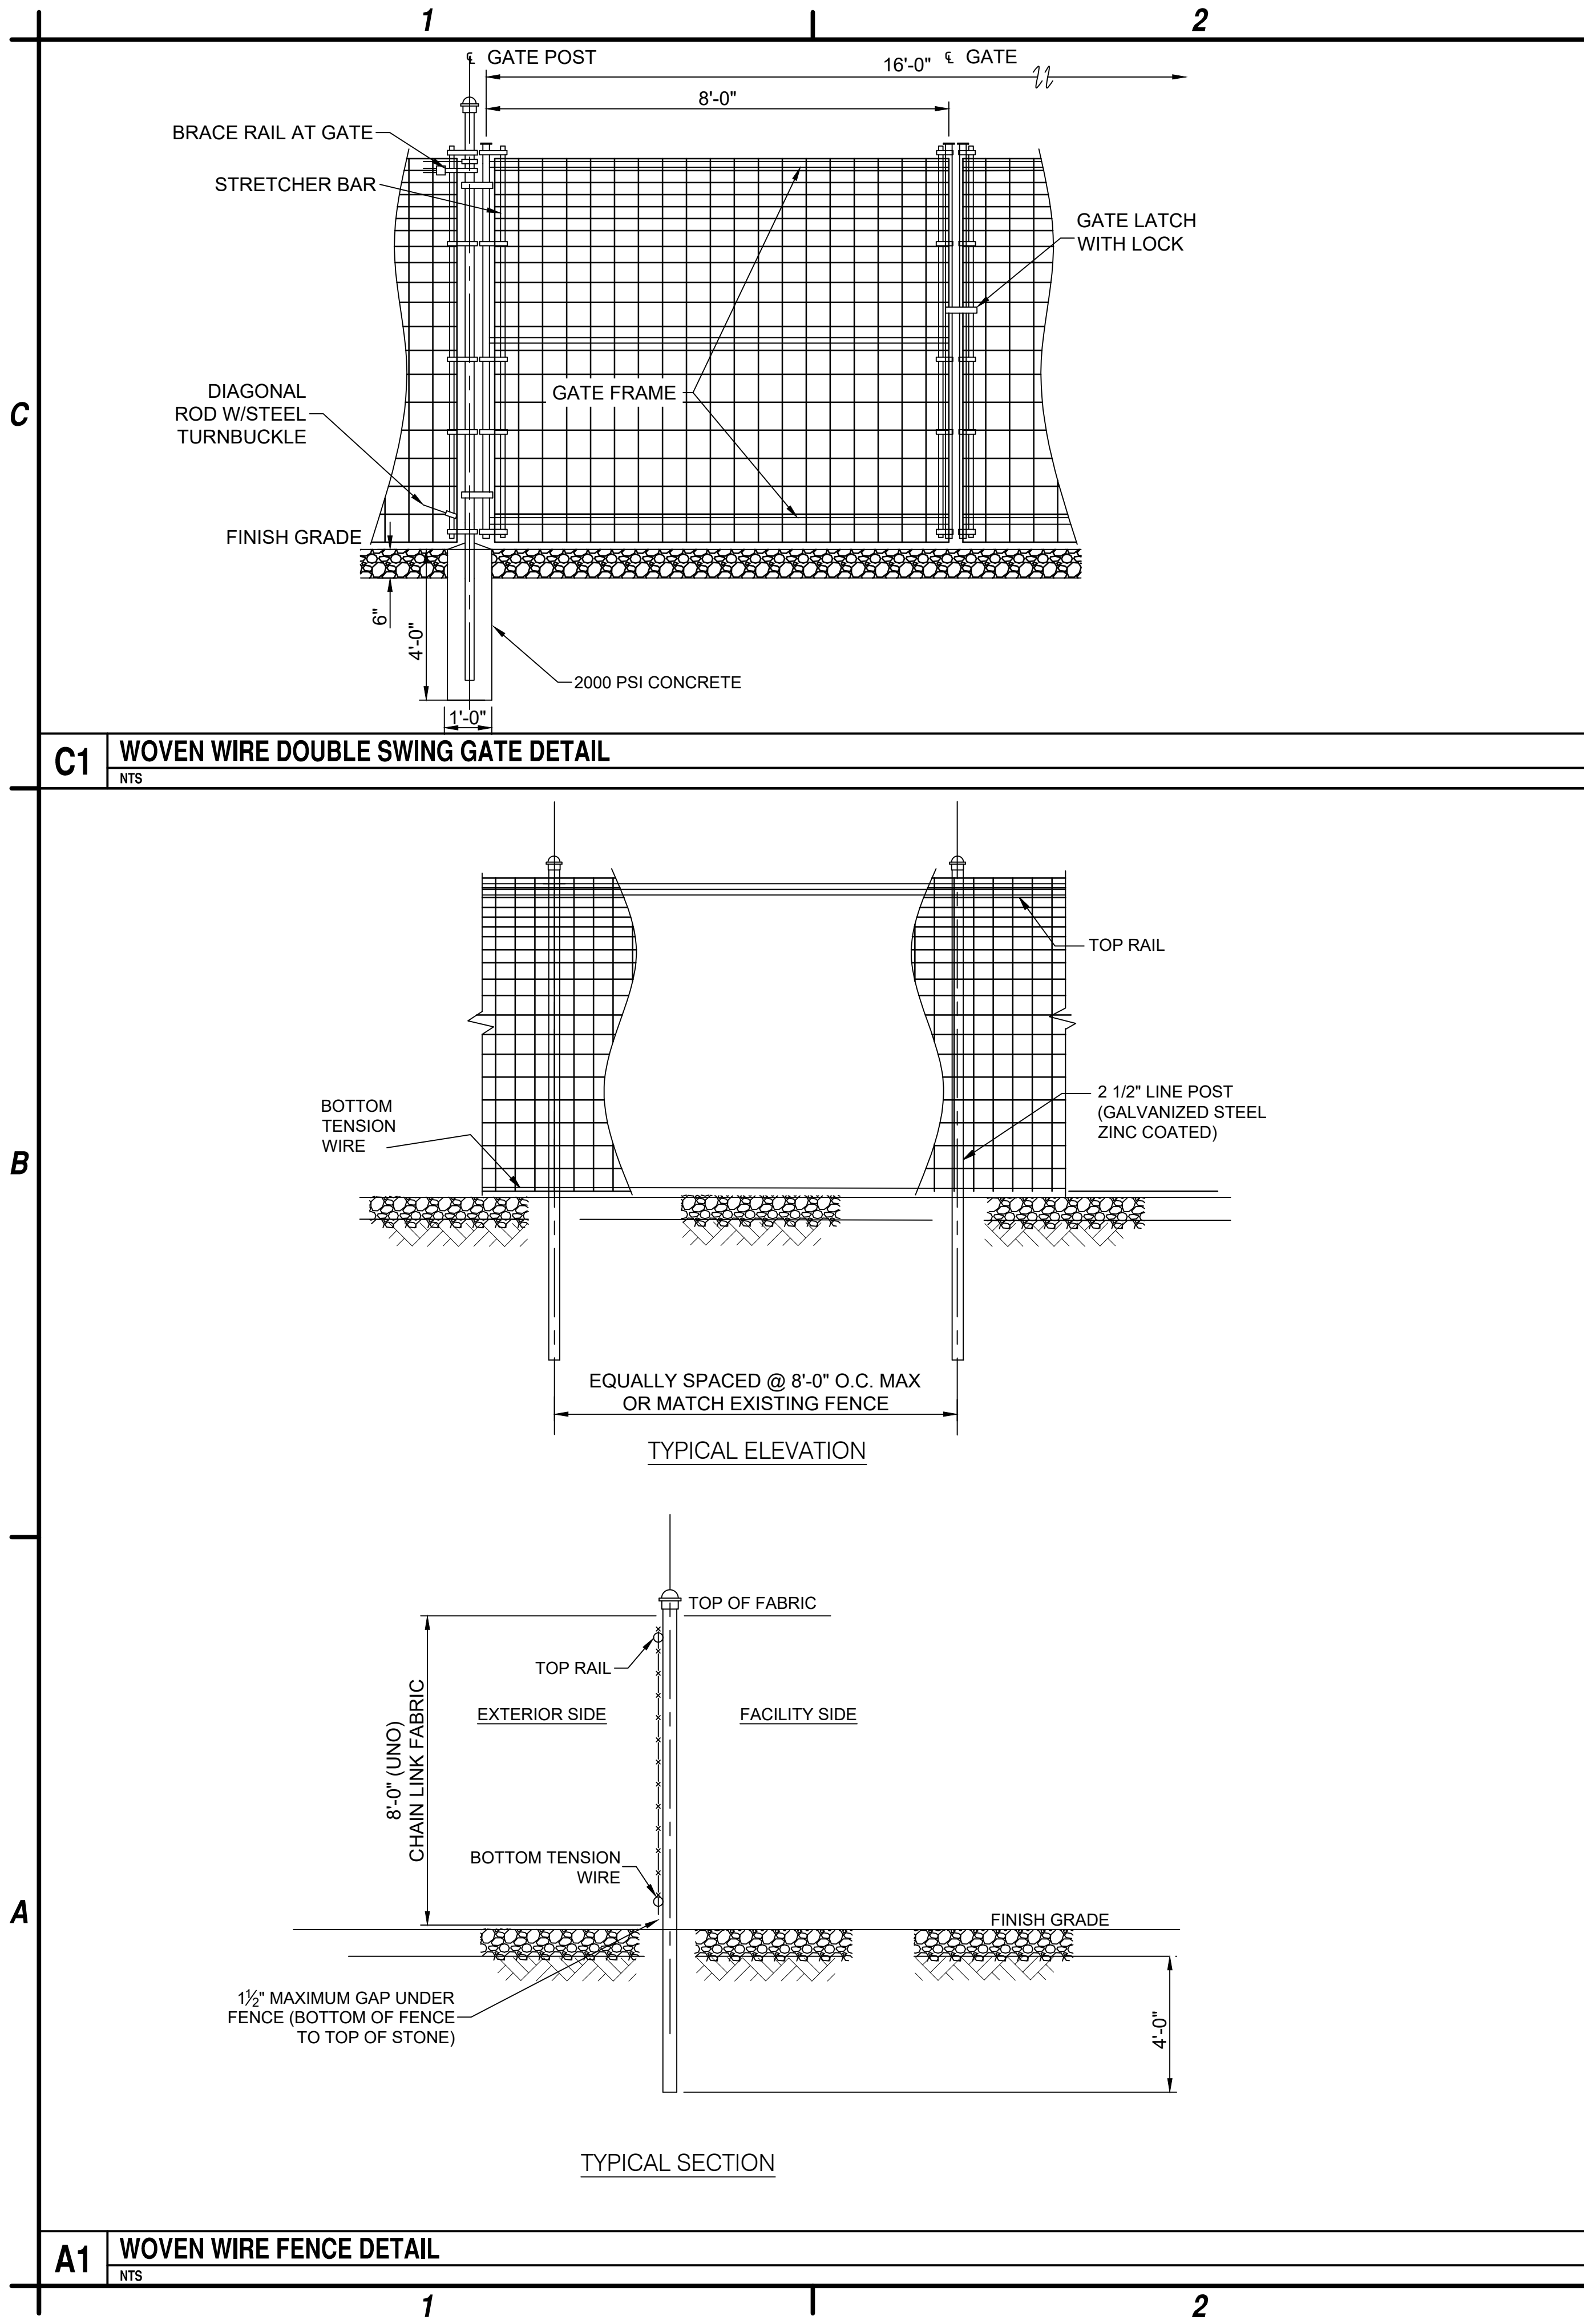

C&S
COMPANIES

C&S Engineers, Inc.
499 Col. Eileen Collins Blvd.
Syracuse, New York 13212
Phone: 315-455-2000
Fax: 315-455-9667
www.cscos.com

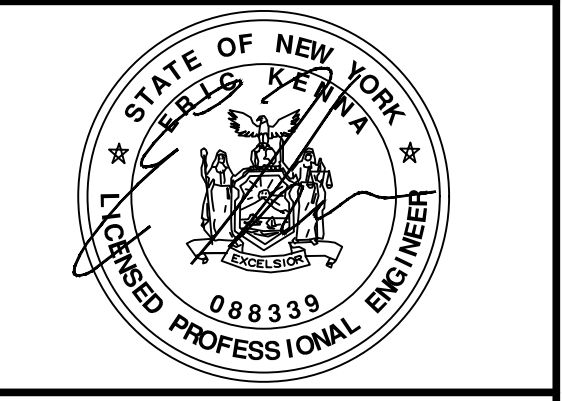


TJA-NY-COHOCTON SOLAR FARM, LLC
11190 NY 371
COHOCTON, NY
LAT: 42.54452 LONG: -77.46018

MARK	DATE	DESCRIPTION
2	11-8-23	SITE LAYOUT
1	6-24-22	ISSUED FOR PERMITTING
REVISIONS		
PROJECT NO: AB7.009.001		
DATE: JULY 2023		
DRAWN BY: M. BUCKINGHAM		
DESIGNED BY:		
CHECKED BY: E.N. KENNA, P.E.		
NO ALTERATION PERMITTED HEREON EXCEPT AS PROVIDED UNDER SECTION 7209 SUBDIVISION 2 OF THE NEW YORK EDUCATION LAW		

FENCE DETAILS

C-502

Nov 08, 2023 - 3:42pm F:\Project\AB7 - Pfister Energy\AB7.009.001 - Cohocton\Design\CADD\Civil Drawings\AB7.009.001_C-503.dwg

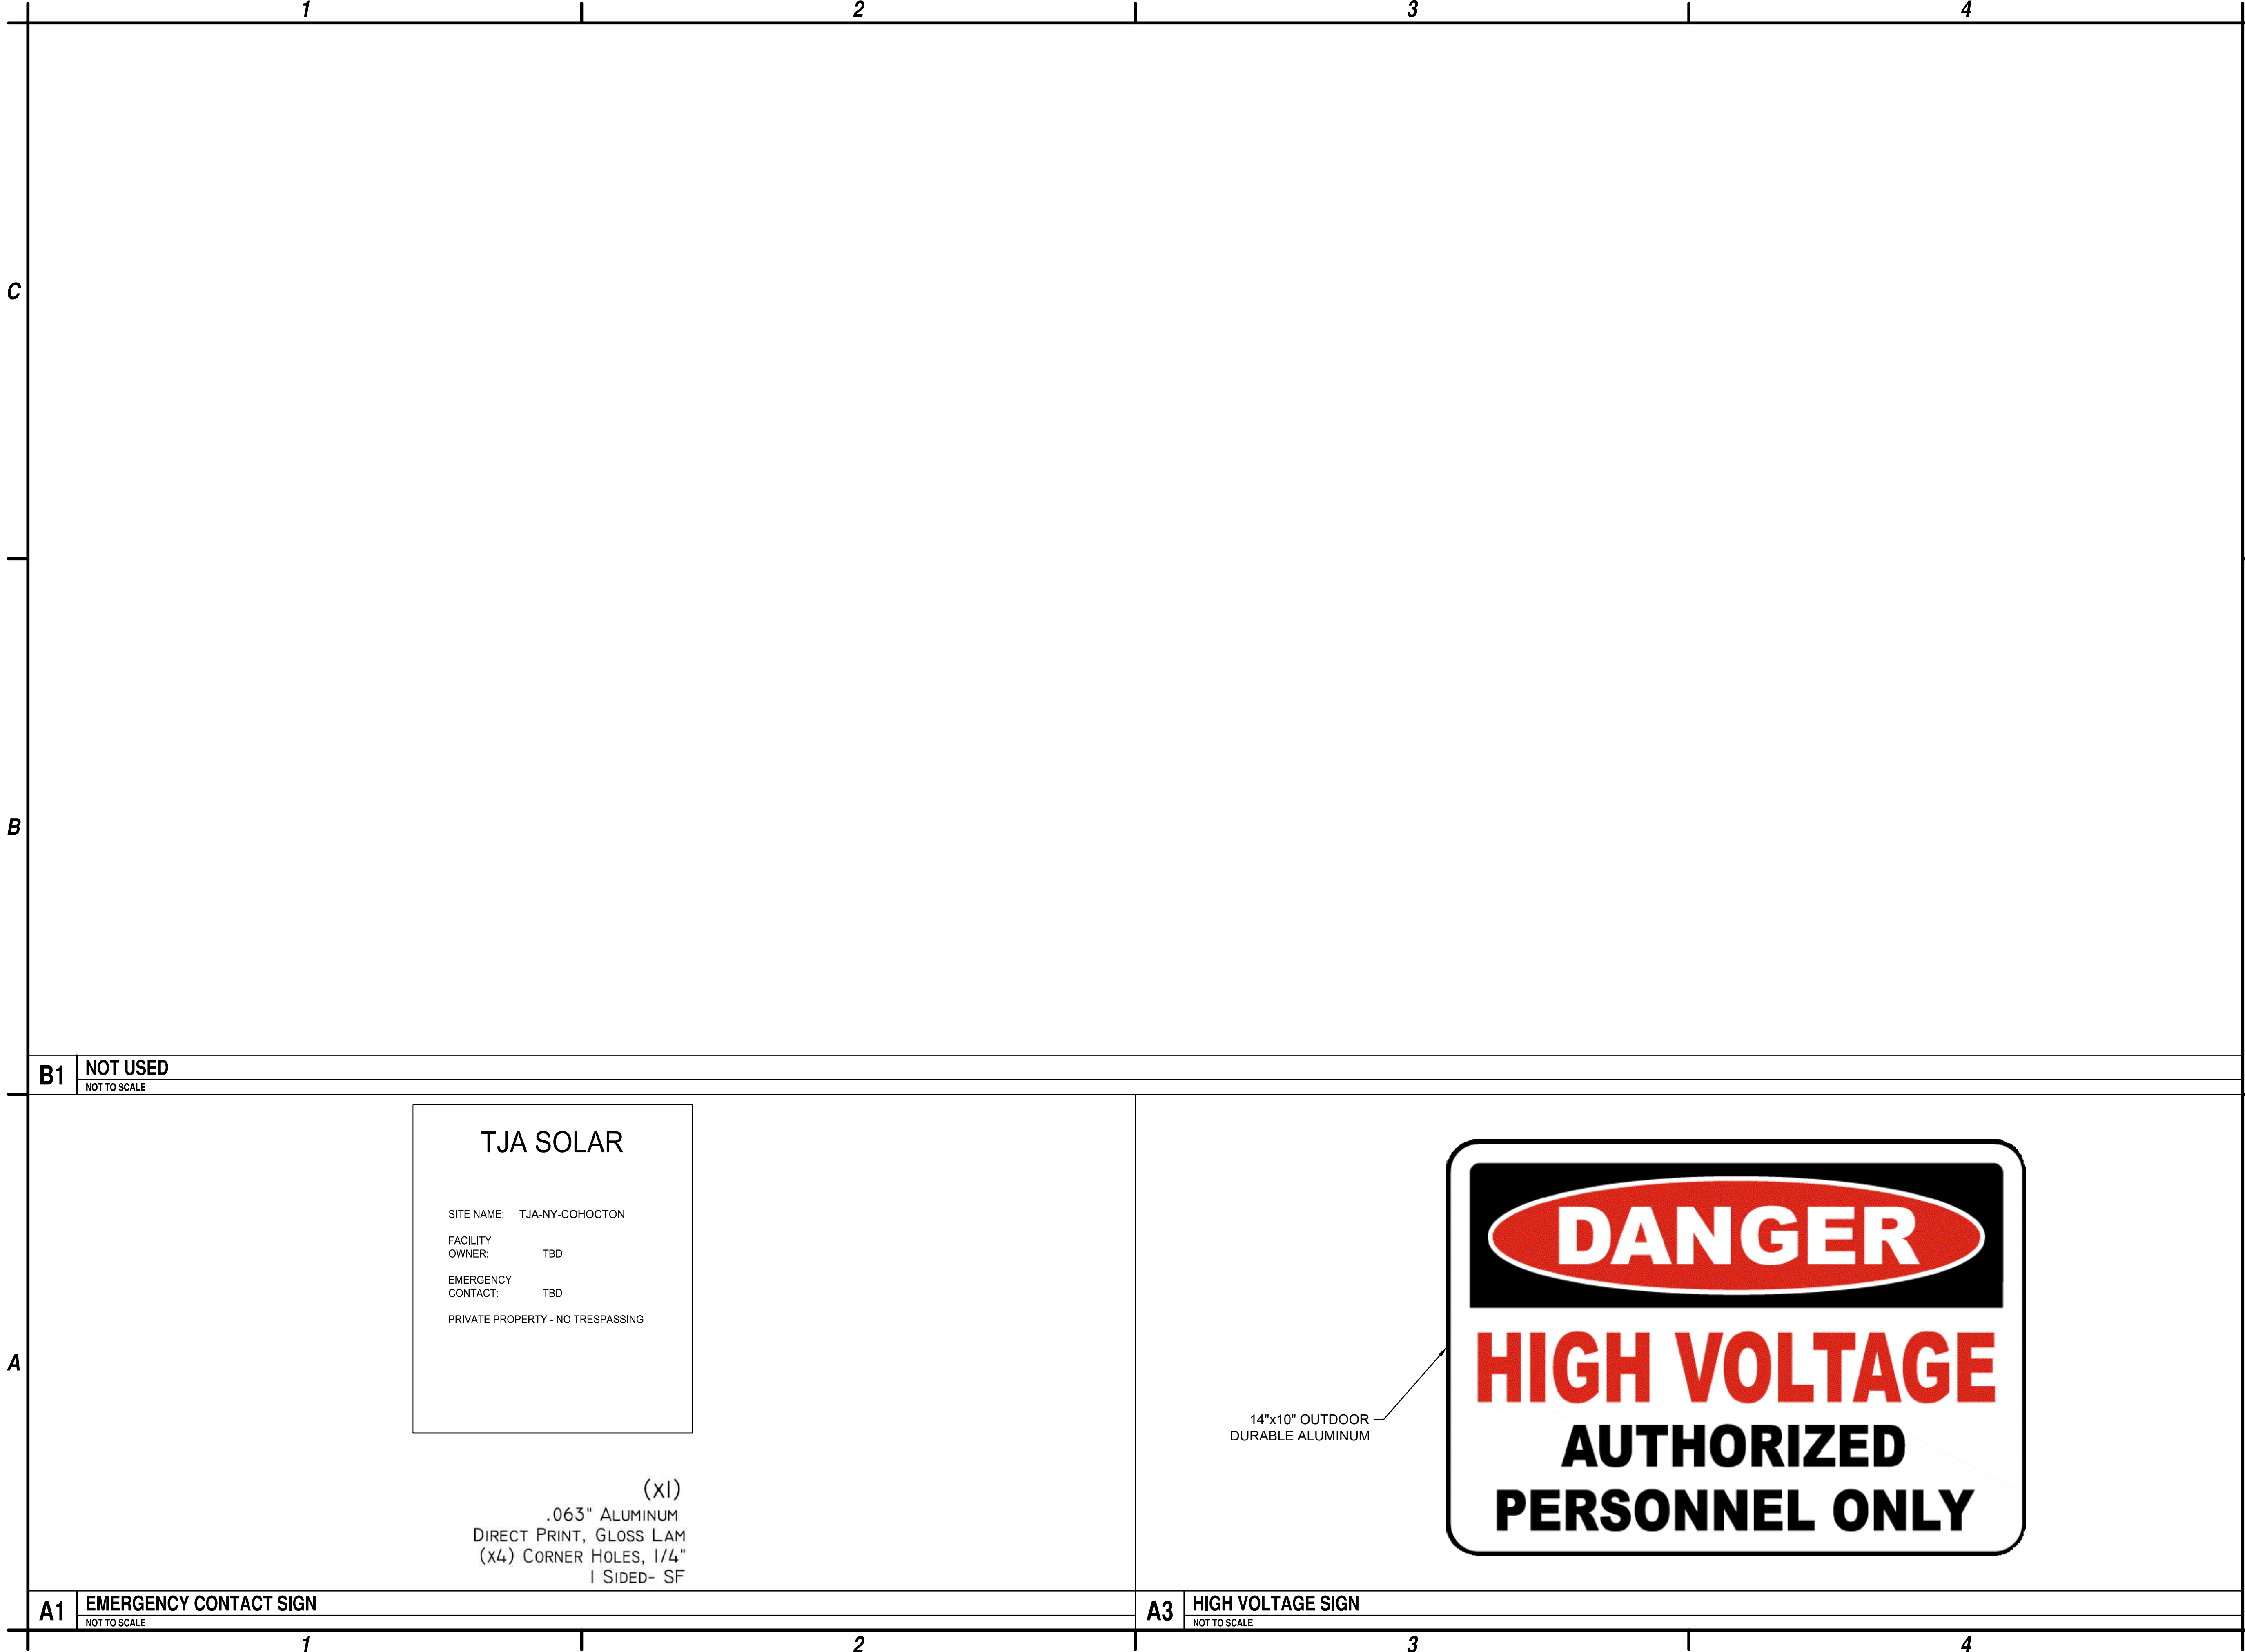

C&S Engineers, Inc.
499 Col. Eileen Collins Blvd.
Syracuse, New York 13212
Phone: 315-455-2000
Fax: 315-455-9667
www.cscos.com




TJA-NY-COHOCTON SOLAR FARM, LLC
11190 NY 371
COHOCTON, NY
LAT: 42.54452 LONG: -77.46018

2	11-8-23	SITE LAYOUT
1	6-24-22	ISSUED FOR PERMITTING
MARK	DATE	DESCRIPTION
REVISIONS		
PROJECT NO: AB7.009.001		
DATE: JULY 2023		
DRAWN BY: M. BUCKINGHAM		
DESIGNED BY: -		
CHECKED BY: E.N. KENNA, P.E.		
NO ALTERATION PERMITTED HEREON EXCEPT AS PROVIDED UNDER SECTION 7209 SUBDIVISION 2 OF THE NEW YORK EDUCATION LAW		


DETAILS

C-503


Nov 08, 2023 3:42pm F:\Project\A67 - Pfister Energy\A67.009.001 - Cohocton\Design\CADD\Civil Drawings\A67.009.001_C-504_E&S Details.dwg

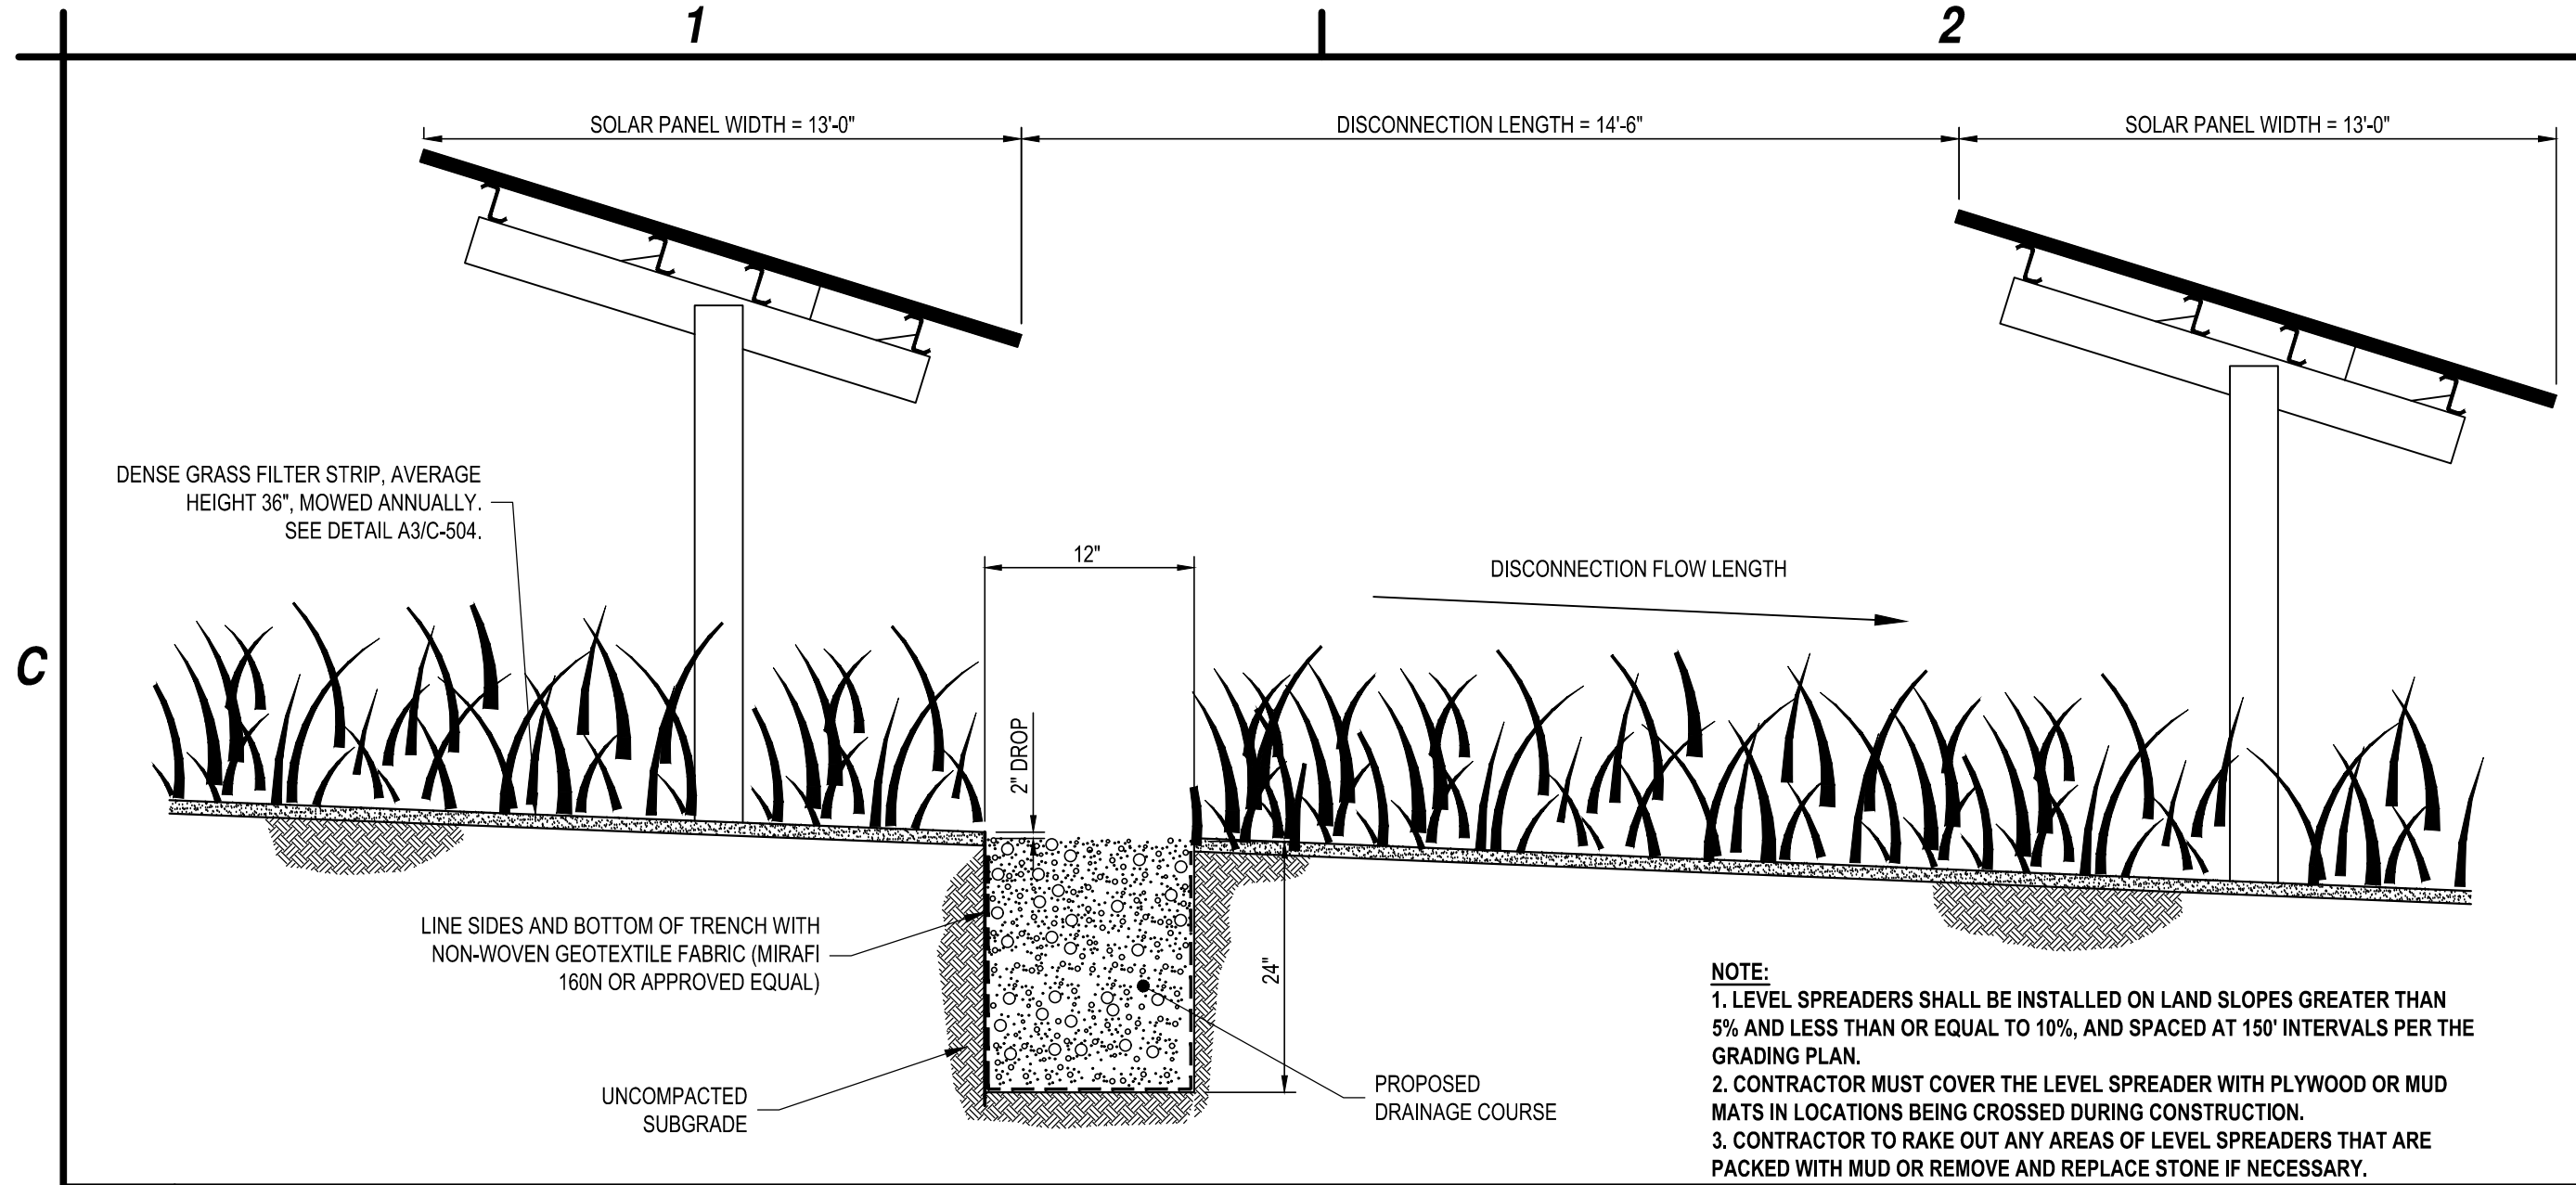

C1 LEVEL SPREADER TYPICAL DETAIL
SCALE: NOT TO SCALE


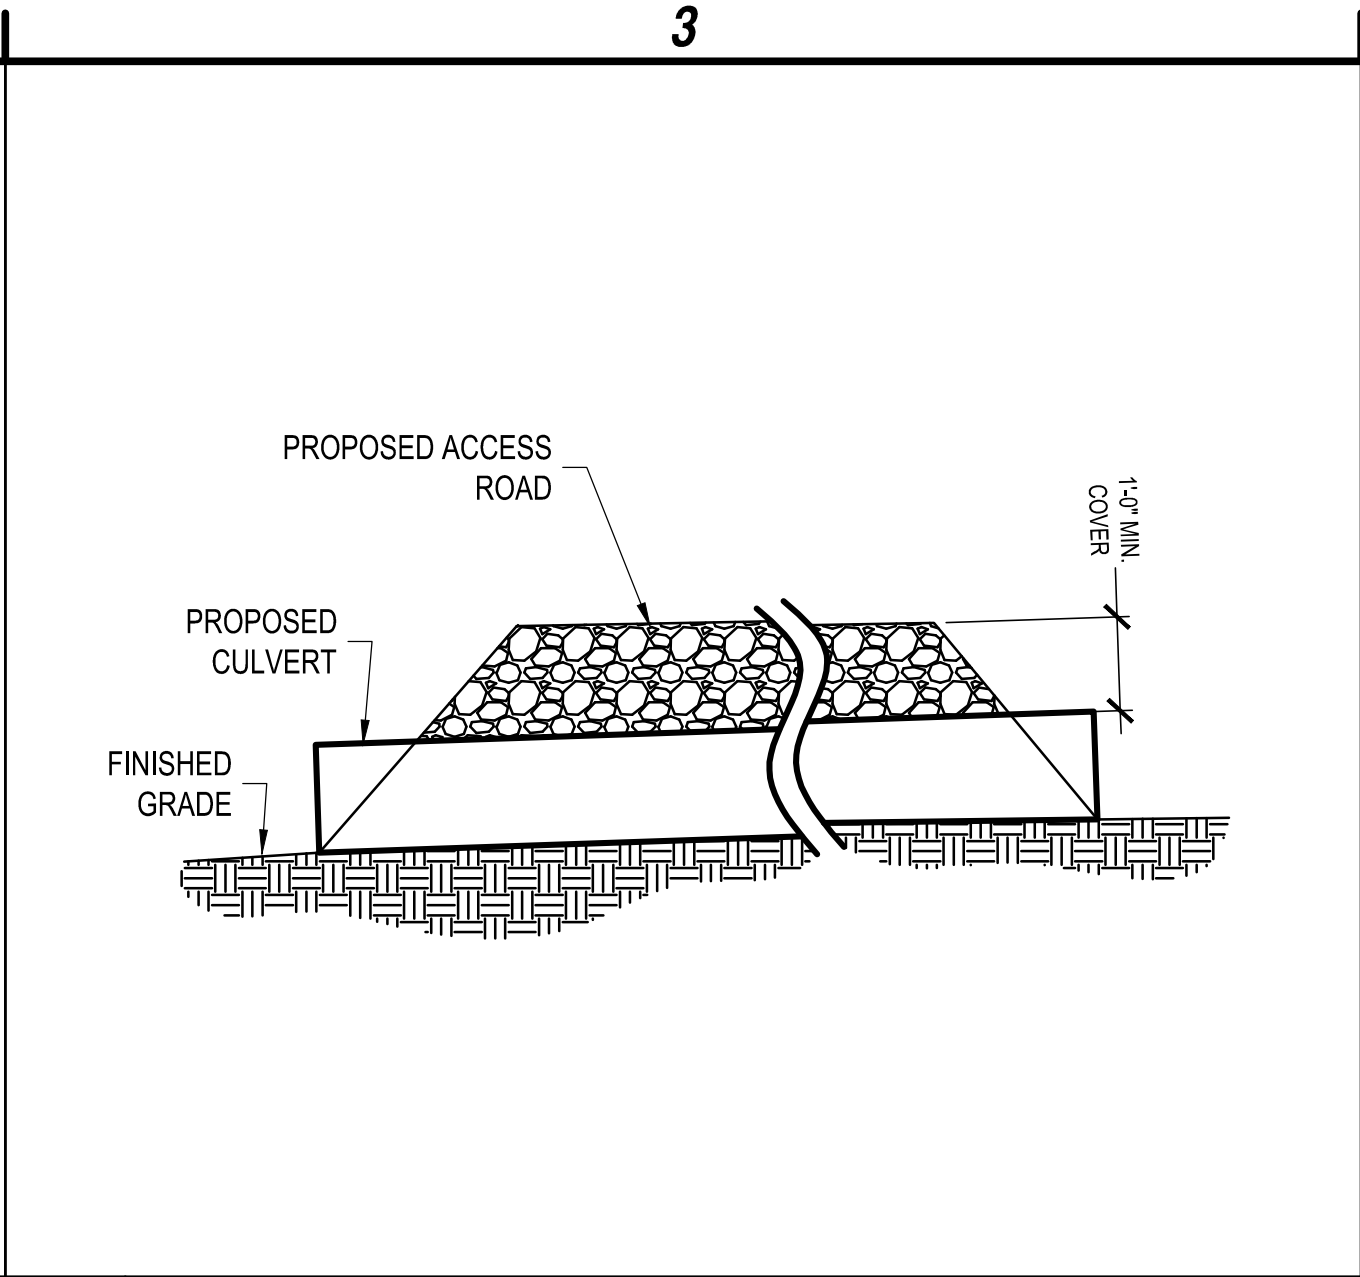


C3 TYPICAL CULVERT DETAIL
SCALE: NOT TO SCALE

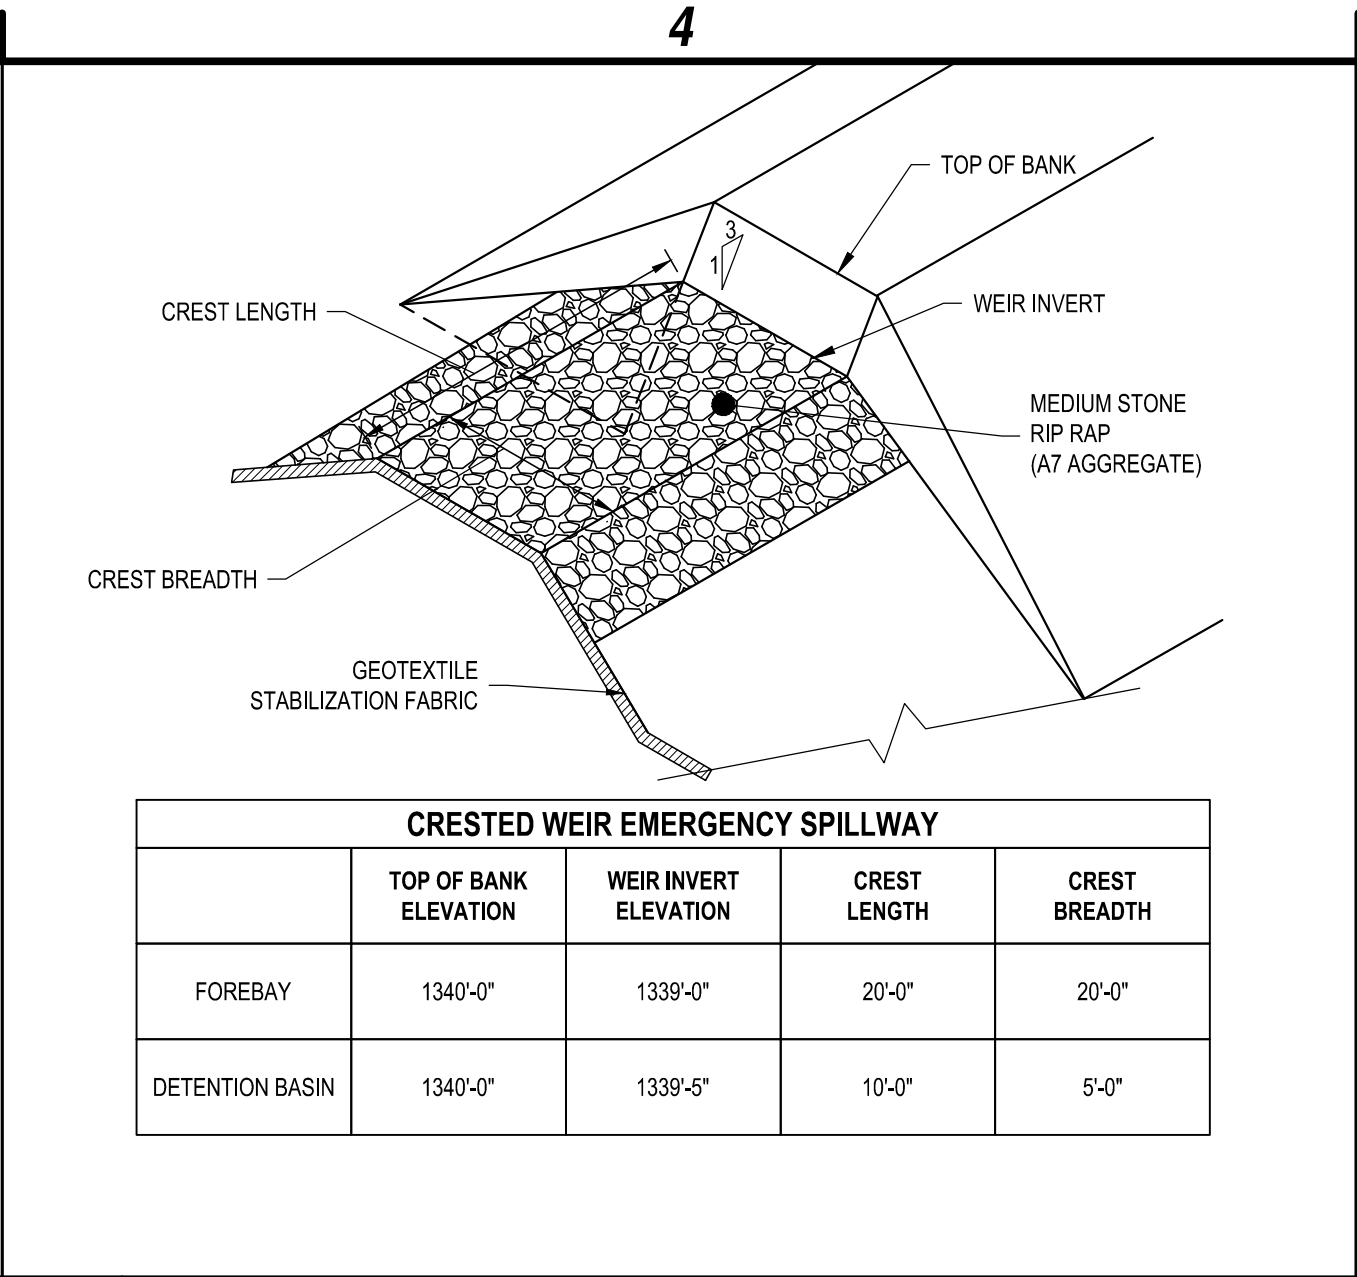


C4 CRESTED WEIR AND EMERGENCY SPILLWAY DETAIL
SCALE: NOT TO SCALE


- B**
- STABILIZED CONSTRUCTION ENTRANCE NOTES:
- STONE SIZE - USE 2" STONE, OR RECLAIMED OR RECYCLED CONCRETE EQUIVALENT.
 - LENGTH - NOT LESS THAN 50 FEET (EXCEPT ON A SINGLE RESIDENCE LOT WHERE A 30 FOOT MINIMUM LENGTH WOULD APPLY).
 - THICKNESS - NOT LESS THAN SIX (6) INCHES.
 - WIDTH - TWELVE (12) FOOT MINIMUM, BUT NOT LESS THAN THE FULL WIDTH AT POINTS WHERE INGRESS OR EGRESS OCCURS. TWENTY-FOUR (24) FOOT IF SINGLE ENTRANCE TO SITE.
 - FILTER FABRIC - WILL BE PLACED OVER THE ENTIRE AREA PRIOR TO PLACING OF STONE.
 - SURFACE WATER - ALL SURFACE WATER FLOWING OR DIVERTED TOWARD CONSTRUCTION ENTRANCES SHALL BE PIPED ACROSS THE ENTRANCE. IF PIPING IS IMPRACTICAL, A MOUNTABLE BERM WITH 5:1 SLOPES WILL BE PERMITTED.
 - MAINTENANCE - THE ENTRANCE SHALL BE MAINTAINED IN A CONDITION WHICH WILL PREVENT TRACKING OR FLOWING OF SEDIMENT ONTO PUBLIC RIGHTS-OF-WAY. ALL SEDIMENT SPILLED, DROPPED, WASHED OR TRACTED ONTO PUBLIC RIGHTS-OF-WAY MUST BE REMOVED IMMEDIATELY.
 - WHEN WASHING IS REQUIRED, IT SHALL BE DONE ON AN AREA STABILIZED WITH STONE AND WHICH DRAINS INTO AN APPROVED SEDIMENT TRAPPING DEVICE.
 - PERIODIC INSPECTION AND NEEDED MAINTENANCE SHALL BE PROVIDED AFTER EACH RAIN.

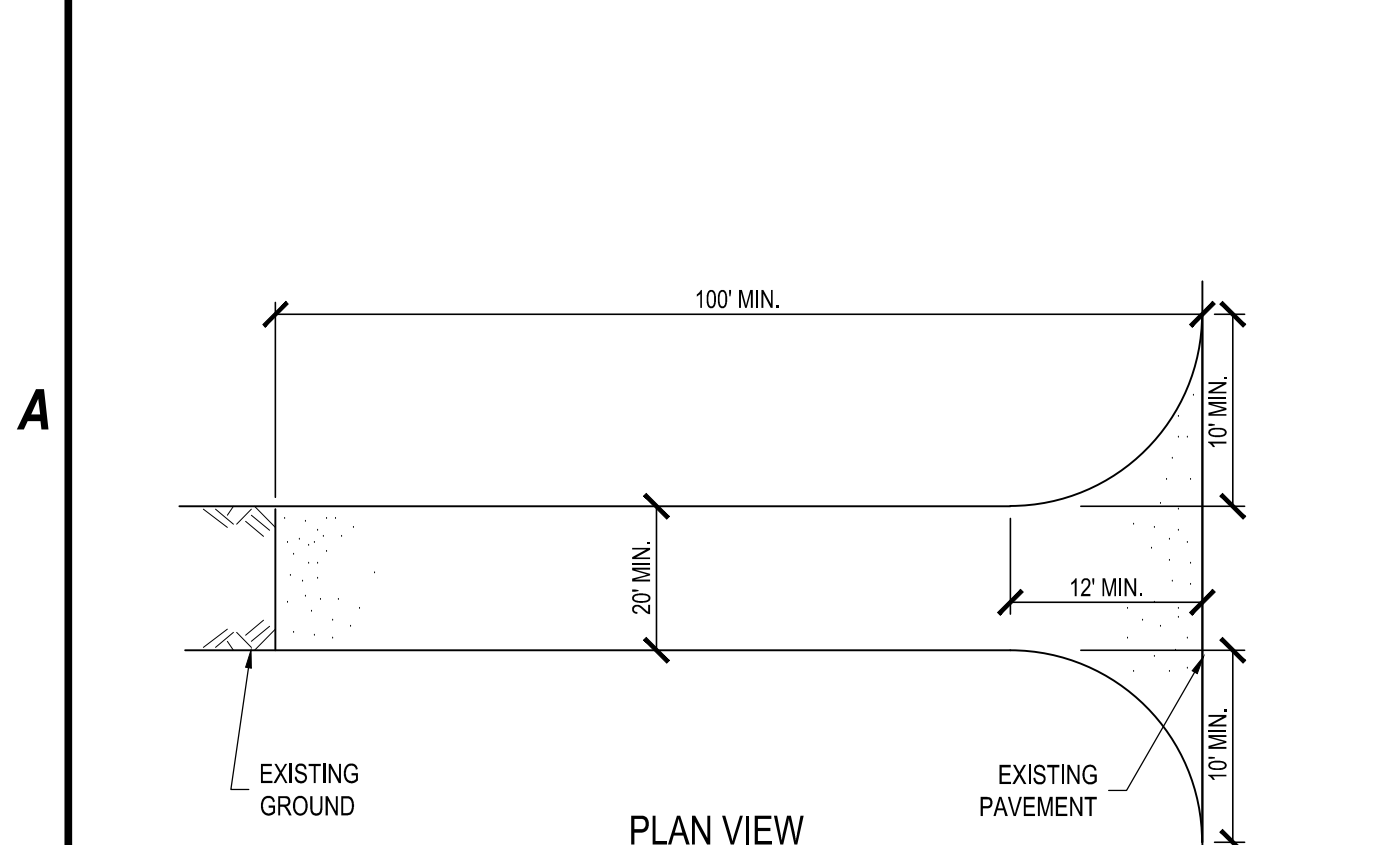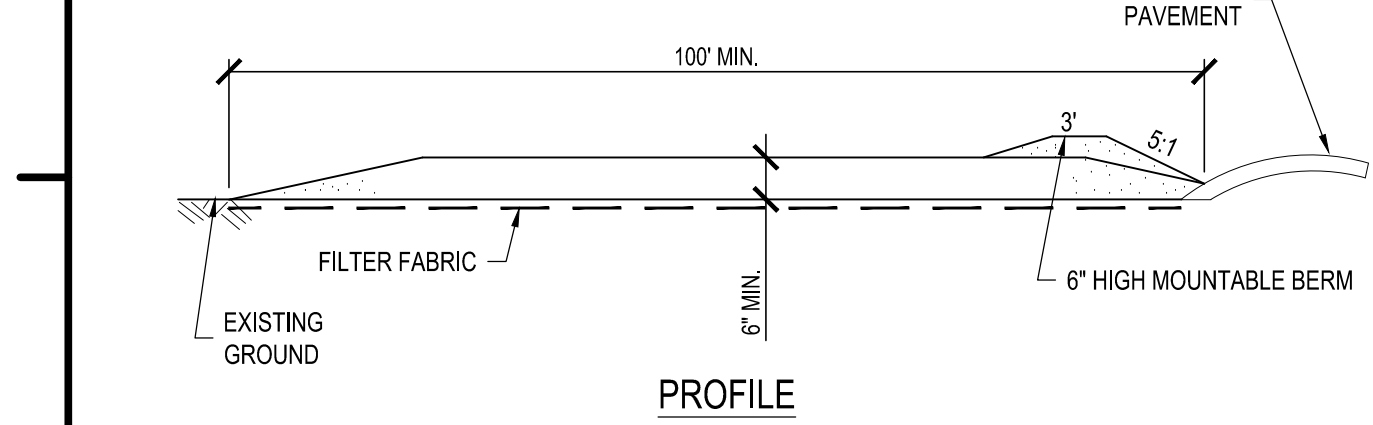

A1 STABILIZED CONSTRUCTION ENTRANCE DETAIL
SCALE: NOT TO SCALE

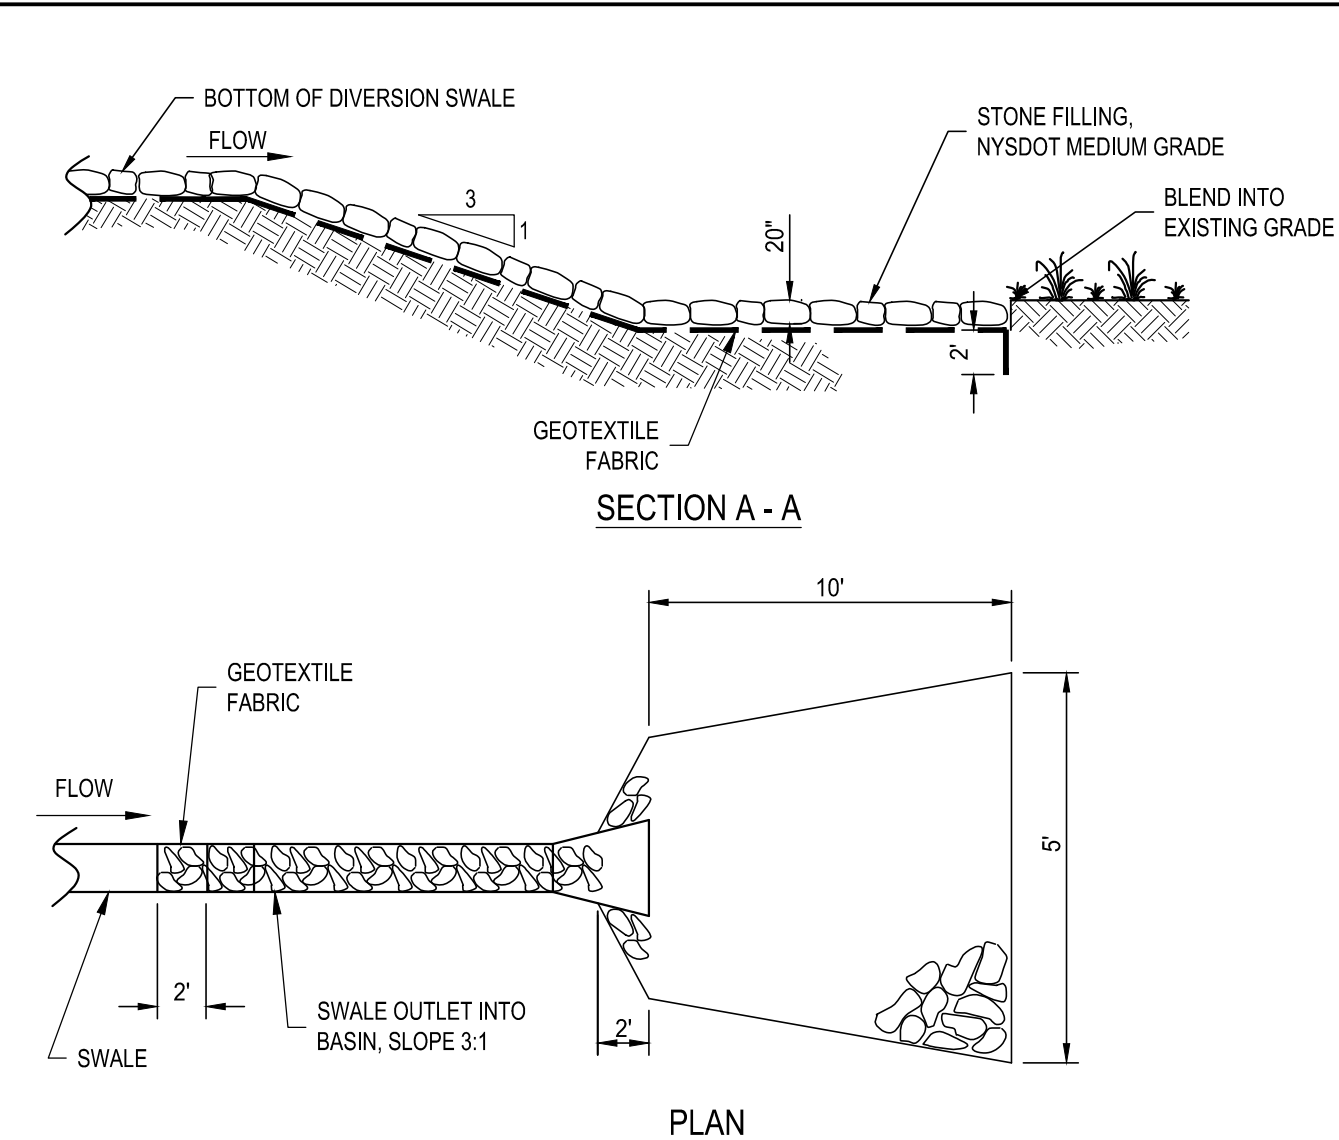


B2 ROCK OUTLET PROTECTION DETAIL
SCALE: NOT TO SCALE

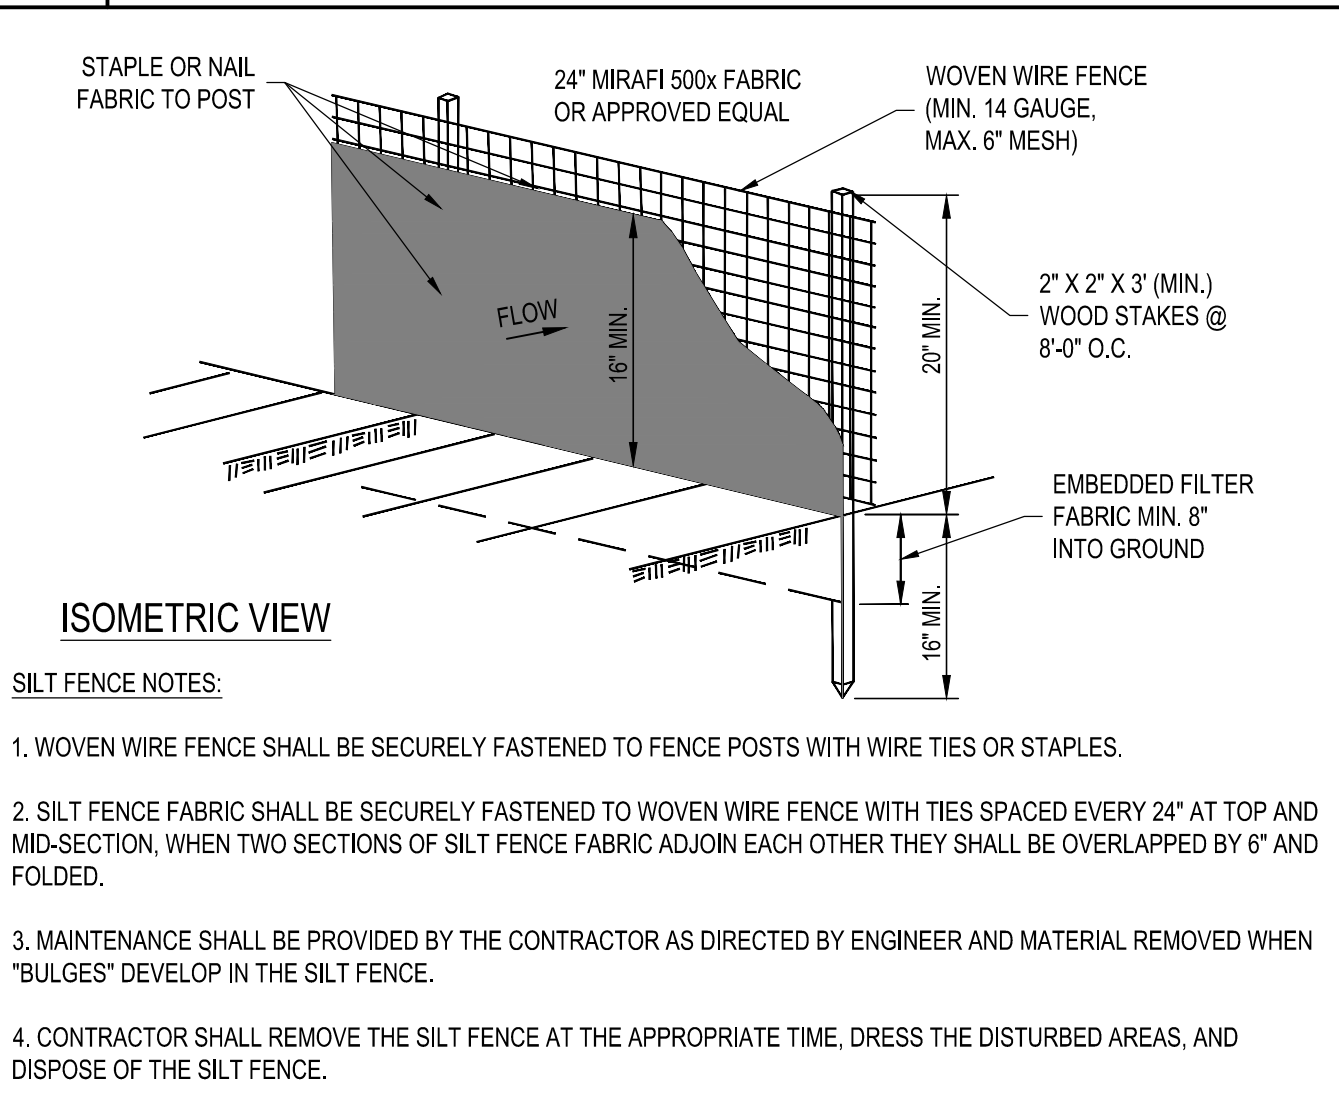


A2 SILT FENCE DETAIL
SCALE: NOT TO SCALE

- B3**
- CONSTRUCTION SEQUENCE
- SCALE: NOT TO SCALE
- SCHEDULE A PRE-CONSTRUCTION MEETING THAT SHALL BE ATTENDED BY THE QUALIFIED INSPECTOR, AND INVOLVED SUBCONTRACTORS TO DISCUSS RESPONSIBILITIES AS THEY RELATE TO THE IMPLEMENTATION OF THE SWPPP MEASURES TO AVOID AND MINIMIZE IMPACTS TO PROTECTED SPECIES DURING REMEDIATION, DEMOLITION AND CONSTRUCTION.
 - INSTALL THE STABILIZED CONSTRUCTION ENTRANCE FOR THE PROJECT AS SHOWN ON THE PLANS.
 - INSTALL ALL SILT / CONSTRUCTION FENCE FOR THE PROJECT AS SHOWN ON THE PLANS.
 - DELINEATE THE LIMITS OF DISTURBANCE FOR THE PROJECT.
 - ESTABLISH LOCATION FOR STAGING AREA AND SOIL STOCKPILE AS SHOWN ON THE PLANS. IF THESE AREAS ARE NOT CONDUCTIVE DUE TO ANY UNFORESEEN CONDITIONS, THE CONTRACTOR SHALL IDENTIFY A NEW LOCATION FOR REVIEW AND APPROVAL BY THE ENGINEER.
 - SELECTIVELY CLEAR ONLY THE AREAS REQUIRED FOR THE FOLLOWING: INSTALLATION OF THE STABILIZED FACILITY ENTRANCE, PLACEMENT OF THE CONSTRUCTION OFFICE TRAILER AND PARKING AREAS, PLACEMENT OF TEMPORARY SEDIMENT AND EROSION CONTROL MEASURES, CONSTRUCTION STAGING AREA, THE SOIL STOCKPILE, AND THE MINIMAL AREAS IDENTIFIED TO BE GRADED TO PROVIDE A MAXIMUM LAND SLOPE OF 20% WITHIN THE LIMITS OF DISTURBANCE.
 - CLEAR AND GRUB THE REMAINDER OF THE SITE.
 - FIRST TO BE GRADED/ EXCAVATED ARE THE BASINS/SWALES, FOLLOWED BY THE ACCESS ROADS AND REMAINDER OF SITE.
 - PROVIDE TEMPORARY SEEDING OF ANY DISTURBED AREAS LEFT UNTOUCHED FOR FOURTEEN DAYS, SEVEN DAYS FOR AREAS TOTALING GREATER THAN 5 ACRES OF DISTURBANCE AT ONE TIME.
 - CONTRACTOR TO INSTALL LEVEL SPREADERS AS SHOWN ON THE GRADING AND EROSION AND SEDIMENT CONTROL PLAN. COVERING THE LEVEL SPREADER WITH PLYWOOD OR MUD MATS IN LOCATIONS WHERE THEY MUST BE CROSSED DURING CONSTRUCTION.
 - INSTALL POSTS, BRACKETS, MOUNTING STRUCTURES, AND MODULES.
 - COMPLETE ON-SITE STABILIZATION.
 - CONTRACTOR TO RAKE OUT ANY AREAS OF LEVEL SPREADERS THAT ARE PACKED WITH MUD OR REMOVE AND REPLACE STONE IF NECESSARY.
 - REMOVE ALL ACCUMULATED SILT AND SEDIMENT FROM THE PRE- TREATMENT FOREBAY UPON FINAL SITE STABILIZATION. INSTALL FINAL INFILTRATION BASIN TO THE FINAL GRADES SHOWN ON THE PLANS. CONTRACTOR SHALL MINIMIZE USE OF HEAVY EQUIPMENT WITHIN THE INFILTRATION BASIN FOOTPRINT AND SHALL SCARIFY THE BASIN FOOTPRINT PRIOR TO PLACEMENT OF TOPSOIL.
 - REMOVE TEMPORARY SEDIMENT CONTROLS.
 - REMOVE SILT FENCING ONLY AFTER DISTURBED SURFACES ARE STABILIZED.
 - UPON FINAL STABILIZATION, AND CERTIFICATION BY THE NYSDEC AND THE QUALIFIED PROFESSIONAL RETAINED TO PERFORM THE REQUIRED SITE INSPECTIONS, THE OWNER SHALL FILE THE NOTICE OF TERMINATION (NOT) WITH THE NYSDEC.

B3 CONSTRUCTION SEQUENCE
SCALE: NOT TO SCALE

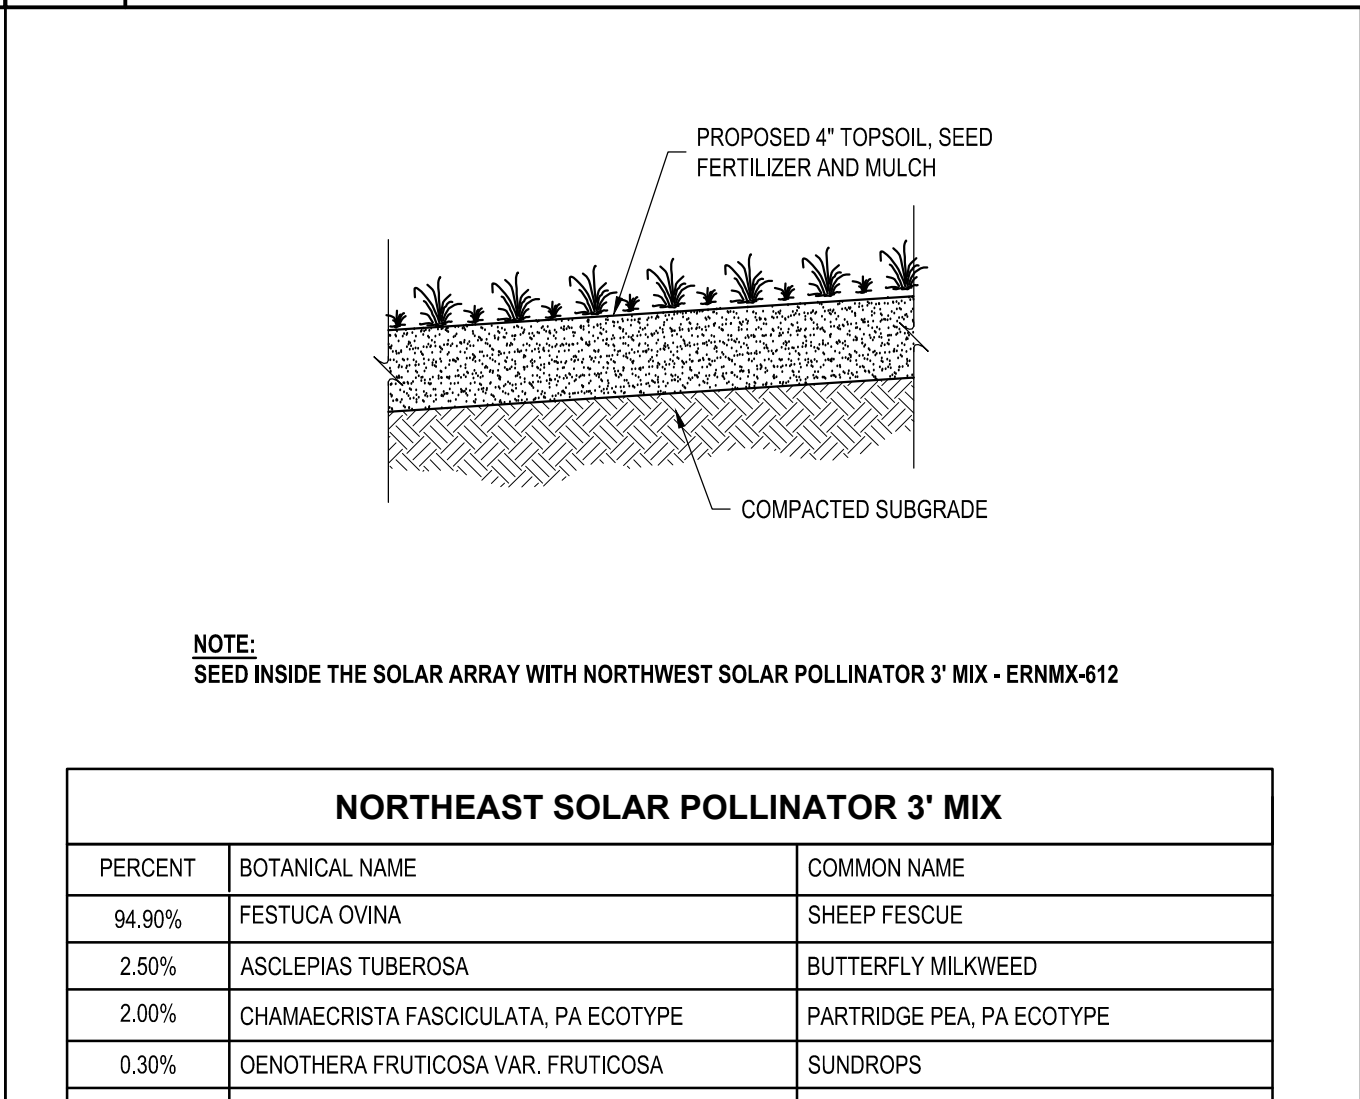


A3 GRASS RESTORATION DETAIL
SCALE: NOT TO SCALE

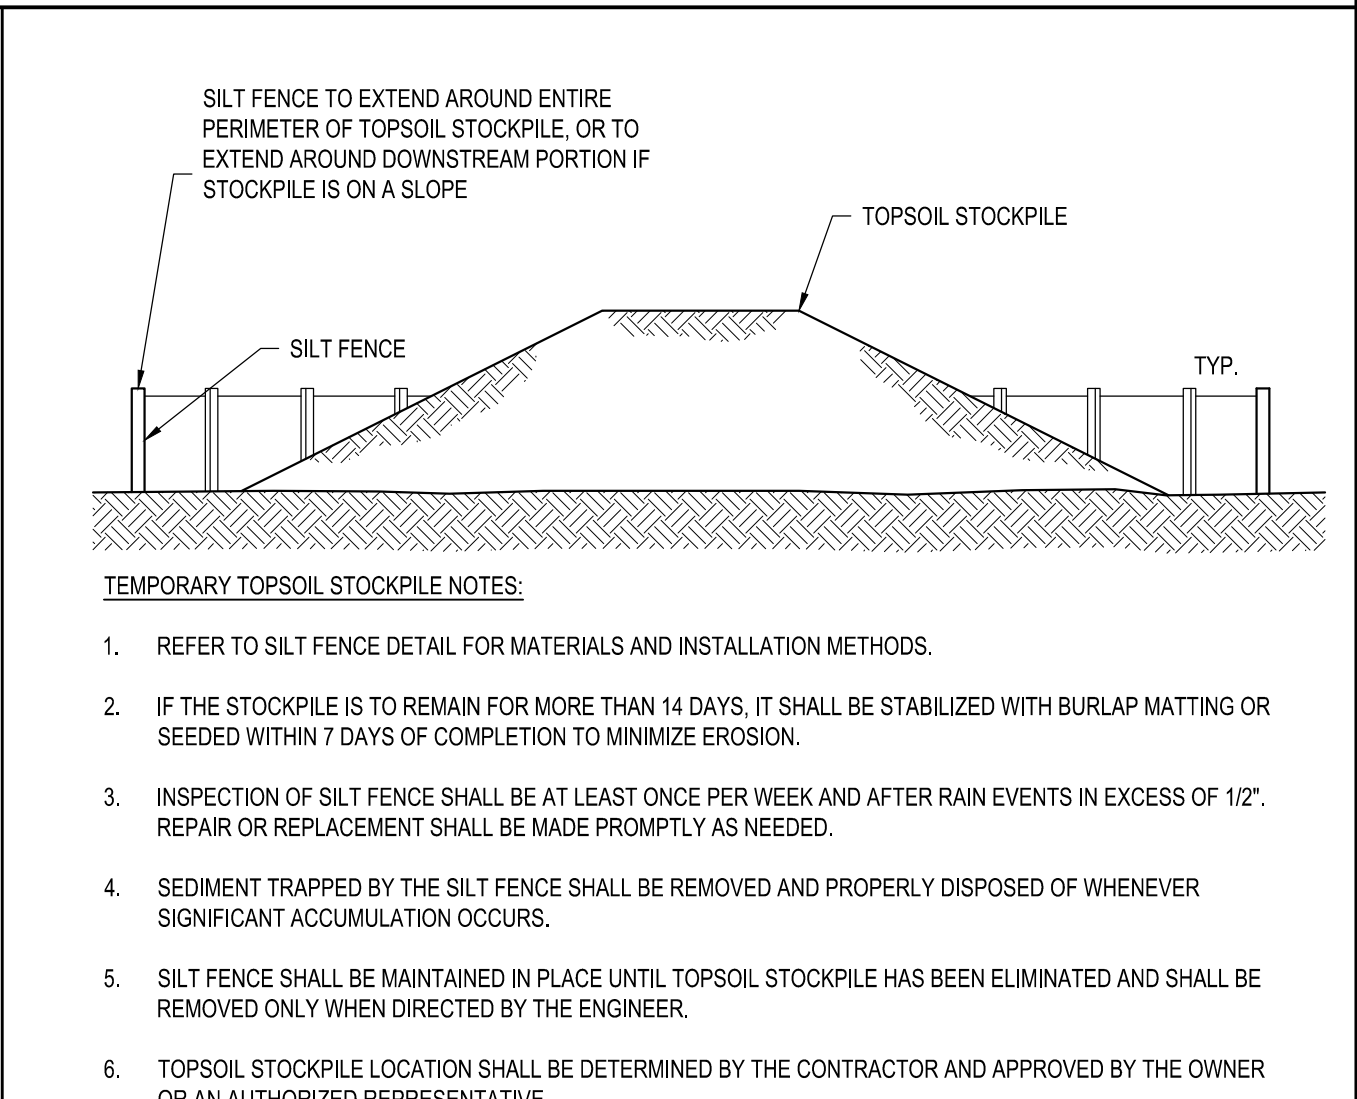

A4 TYPICAL TOPSOIL STOCKPILE DETAIL
SCALE: NOT TO SCALE

C&S COMPANIES

C&S Engineers, Inc.
499 Col. Eileen Collins Blvd.
Syracuse, New York 13212
Phone: 315-455-2000
Fax: 315-455-9667
www.cscos.com

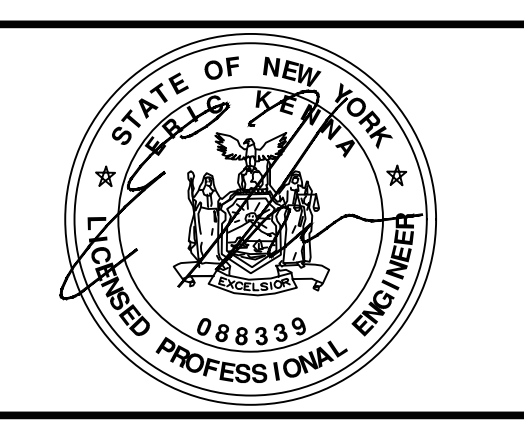

TJA-NY-COHOCTON SOLAR FARM, LLC
11190 NY 371
COHOCTON, NY
LAT: 42.54452 LONG: -77.46018

2	11-8-23	SITE LAYOUT
1	6-24-22	ISSUED FOR PERMITTING
MARK	DATE	DESCRIPTION
REVISIONS		
PROJECT NO: AB7.009.001		
DATE: JULY 2023		
DRAWN BY: A. CAMPANY		
DESIGNED BY: E.N. KENNA P.E.		
CHECKED BY:		
NO ALTERATION PERMITTED HEREON EXCEPT AS PROVIDED UNDER SECTION 7209 SUBDIVISION 2 OF THE NEW YORK EDUCATION LAW		

EROSION AND SEDIMENT CONTROL DETAILS

C-504

