


L:\Palmyra\dwg\2024 Closure\00 - cover sheet.dwg Layout=Layout1

OLD PALMYRA LANDFILL CLOSURE REMEDIATION PLAN

PALMYRA, NEW YORK

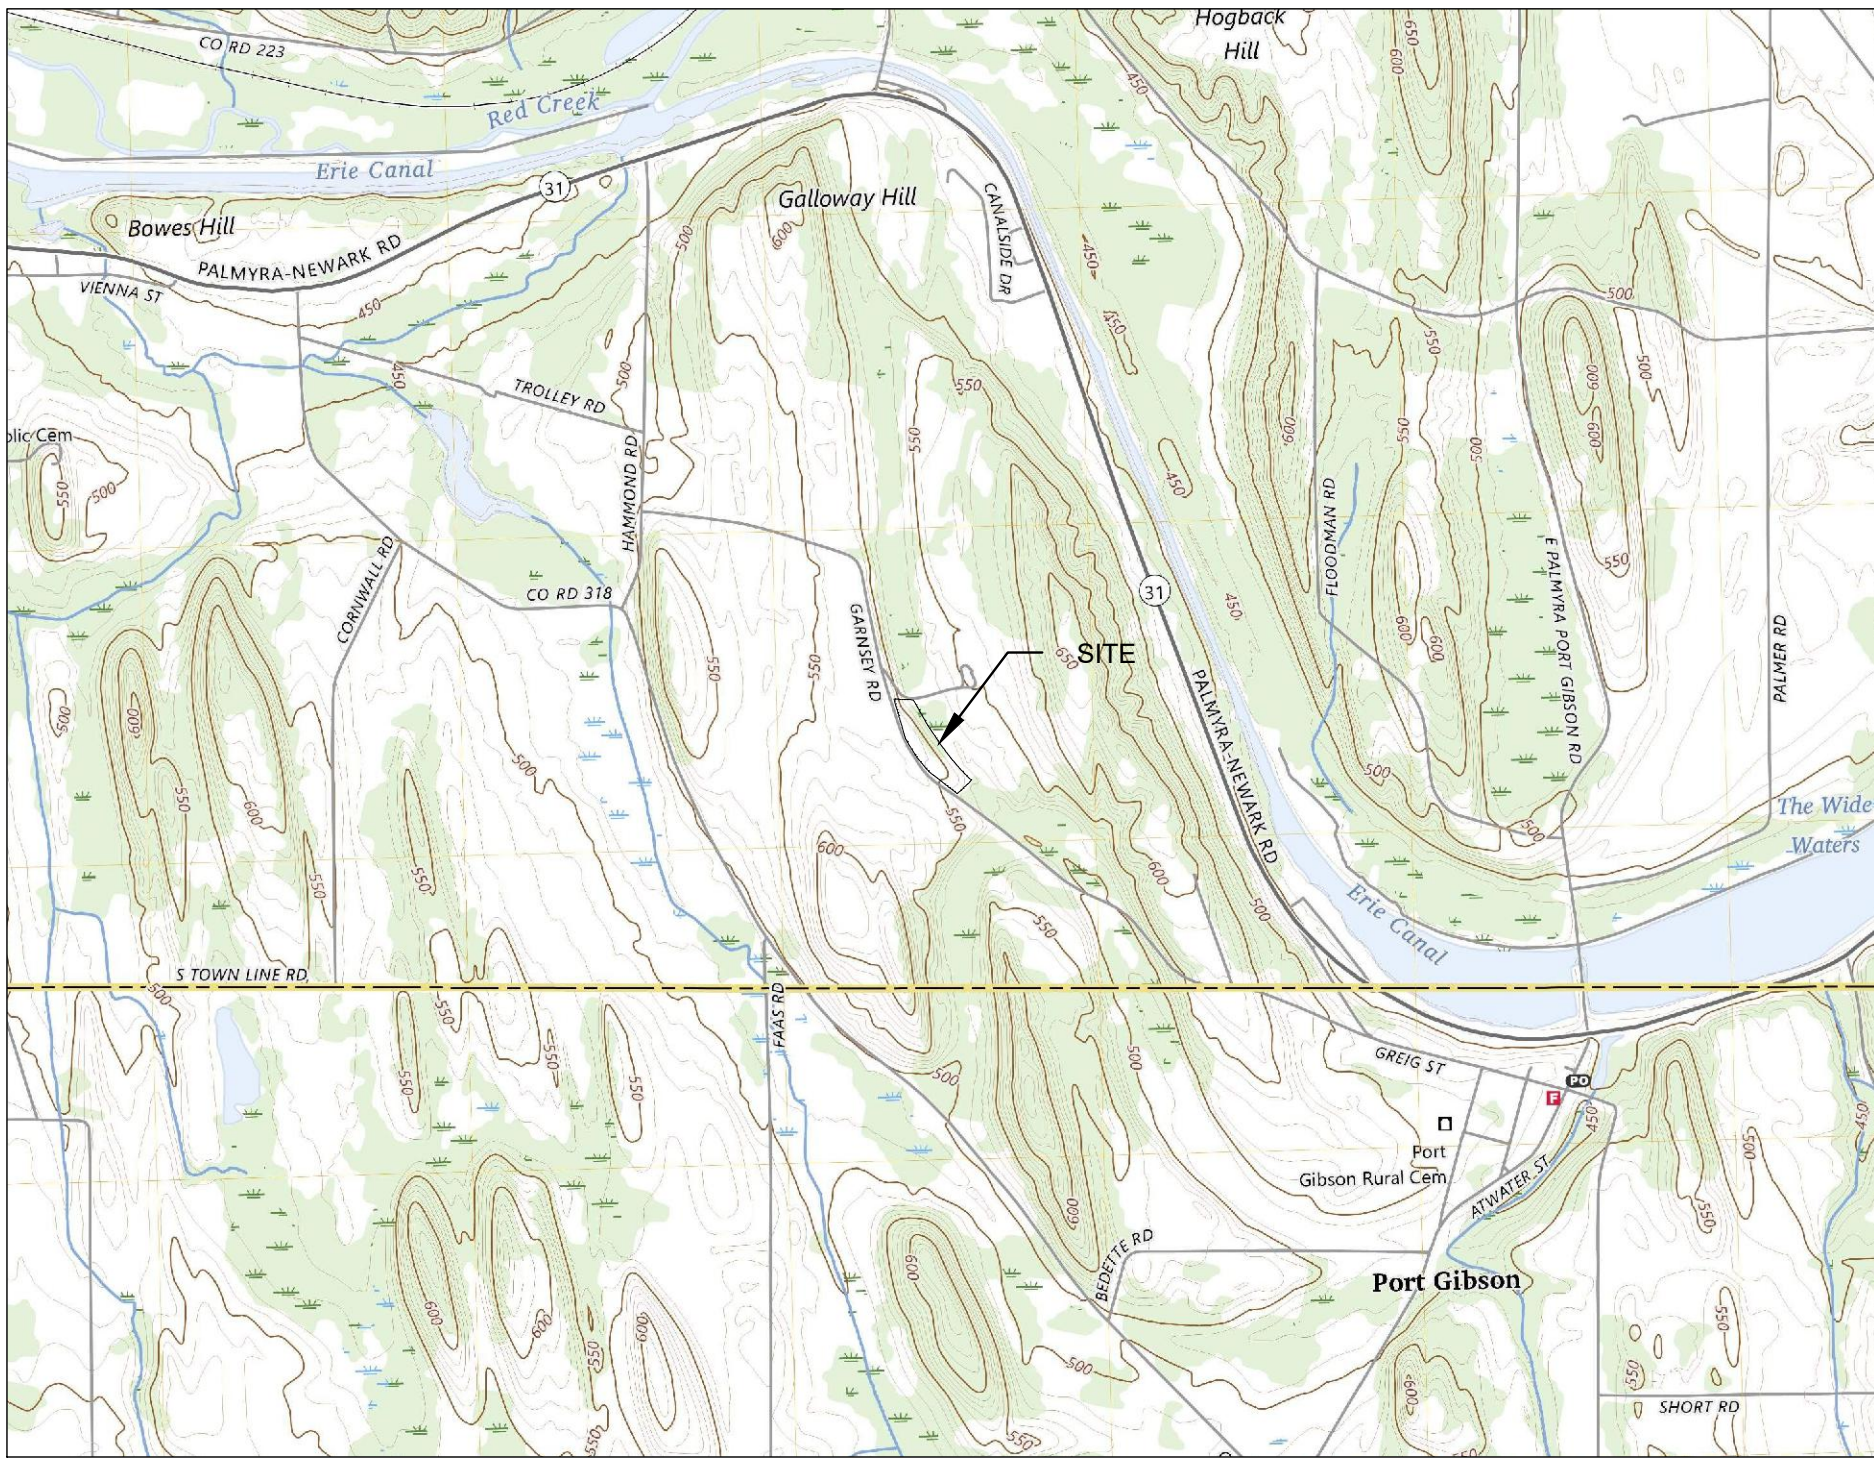

VICINITY MAP
SCALE: 1"=2000'

OWNER INFORMATION	
PREPARED FOR:	TOWN OF PALMYRA
ADDRESS:	1180 CANANDAIGUA ROAD PALMYRA, NEW YORK 14522
CONTACT:	TOWN SUPERVISOR, GARY ROSE
PROPERTY INFORMATION	
ADDRESS:	GARNSEY ROAD PALMYRA, NEW YORK 14522

AUGUST 27, 2024

DRAWING INDEX	
DRAWING NUMBER	DRAWING NAME
00	COVER SHEET
01	NOTES AND LEGEND
02	EXISTING CONDITIONS
03	BASE GRADING PLAN
04	FINAL GRADING PLAN
05	POST EROSION AND SEDIMENT CONTROL PLAN
06	E&S NOTES AND DETAILS
07	SITE DETAILS



It is a violation of New York Education Law Article 145 Sec.7209, for any person, unless acting under the direction of a licensed architect, professional engineer, or land surveyor, to alter an item in any way. If an item bearing the seal of an architect, engineer, or land surveyor is altered; the altering architect, engineer, or land surveyor shall affix to the item their seal and notation "altered by" followed by their signature and date of such alteration, and a specific description of the alteration.

© 2024 LaBella Associates

Town of Palmyra

1180 Canandaigua Road
Palmyra, New York



Landfill Closure Remediation

Project Address

NO:	DATE:	DESCRIPTION:
Revisions		

PROJECT NUMBER:	2242908
DRAWN BY:	IWW
REVIEWED BY:	DWT
ISSUED FOR:	CONSTRUCTION
DATE:	08/27/2024
DRAWING NAME:	

COVER SHEET

DRAWING NUMBER:

00

L:\Palmyra\dwg\2024 Closure\01 - note and legend.dwg Layout=Layout1

CONVENTIONAL SYMBOLS AND GENERAL NOTES

LINES

	EXISTING	PROPOSED
PROPERTY LINE / FACILITY BOUNDARY	---	---
EASEMENT	---	---
RIGHT OF WAY	--- RW ---	--- RW ---
FENCE LINE	- x - x - x -	- x - x - x -
SURFACE WATER	---	---
APPROXIMATE 100 YEAR FLOODPLAIN	---	---
OVERHEAD ELECTRIC	--- OHE ---	--- OHE ---
UNDERGROUND ELECTRIC	- - - UGE - - -	- - - UGE - - -
OVERHEAD TELEPHONE	--- OHT ---	--- OHT ---
UNDERGROUND TELEPHONE	- - - UGT - - -	- - - UGT - - -
FORCEMAIN	--- FM ---	--- FM ---
SANITARY SEWER	--- SS ---	--- SS ---
PROCESS SEWER	--- PS ---	--- PS ---
NATURAL GAS	--- G ---	--- UGG ---
POTABLE WATER	--- W ---	--- W ---
CULVERT (SIZE NOTED)	=====	=====
PAVED ROAD	=====	=====
GRAVEL/DIRT ROAD	=====	=====
TREE LINE	~~~~~	~~~~~
MAJOR TOPOGRAPHIC CONTOUR	--- 100 ---	--- 100 ---
MINOR TOPOGRAPHIC CONTOUR	---	---
LIMITS OF WASTE	=====	=====

PLAN-VIEW HATCHING

	EXISTING	PROPOSED
DEMOLITION		
ASPHALT PAVEMENT		
GRAVEL		
CONCRETE		
WETLANDS		

SYMBOLS

	EXISTING	PROPOSED
GROUNDWATER MONITORING WELL	● MW-X	○ MW-X
OBSERVATION WELL	● MW-OW-X	○ MW-OW-X
NES WELL	● NES-OW-X	○ NES-OW-X
PERFORMANCE WELL	● MW-PW-X	○ MW-PW-X
SENTINEL WELL	● MW-X	○ MW-X
EXTRACTION WELL	■ EW-X	□ EW-X
WETLANDS PIEZOMETER	● PZ-X	● PZ-X
PIEZOMETER	⊕ PZ-X	⊗ PZ-X
LANDFILL GAS PROBE	● GP-X	● GP-X
PASSIVE LFG VENT	▲ GV-X	▲ GV-X
LFG EXTRACTION WELL WITH PUMP	▼ GWP-X	▼ GWP-X
LFG EXTRACTION WELL	▲ GW-X	▲ GW-X
CONDENSATE TRAP WITH PUMP	● CT/P-1	● CT/P-1
CONDENSATE TRAP WITHOUT PUMP	● CT-1	● CT-1
SURFACE WATER MONITORING POINT	● SMP-X	● SMP-X
LEACHATE MONITORING POINT	■ LMP-X	■ LMP-X
BORE HOLE LOCATION	● B-X	○ BH-X
CORING LOCATION	⊗ C-X	⊗ C-X
SOIL SAMPLING LOCATION	● SS-X	● SS-X
TEST PIT LOCATION	⊕ TP-X	⊕ TP-X
WELL LOCATION	⊕ W	⊕ W
SPRINGHEAD LOCATION	○ S-X	○ S-X
BENCHMARK	● BM	● BM
CONTROL POINT	△ CP	△ CP
UTILITY POLE	⊕	⊕
SIGN	⊕	⊕
HYDRANT	⊕	⊕
WATER METER	⊕ WM	⊕ WM
VALVE	⊕	⊕
PIPE FITTINGS	⊕	⊕
LIGHT POLE	⊕	⊕
TANK (SIZE VARIES)	○	○
TRANSFORMER	⊕	⊕
MANHOLE	⊕	⊕
CLEANOUT	○ CO	○ CO
VALVE LOCATION & IDENTIFICATION	⊕ V-3	⊕ V-3
STORMWATER PIPE OUTLET PROTECTION	⊕	⊕
SPOT ELEVATION	× 14.70	× 14.70

SURVEY NOTES:

- TOPOGRAPHIC CONTOUR INTERVAL = 2 FEET, UNLESS INDICATED OTHERWISE.
- ON-SITE TOPOGRAPHY PROVIDED BY LABELLA ASSOCIATES, 300 STATE STREET, SUITE 201, ROCHESTER, NY 14614, (585)-454-6110, THE SITE WAS SURVEYED ON ON DECEMBER 1 2023
- VERTICAL DATUM NAD 88
- HORIZONTAL DATUM IS NAD 83 NEW YORK CENTRAL ZONE US FOOT.

CONTROL POINTS


POINT	NORTHING	EASTING	ELEVATION
10	1,110,343.88	660,822.00	558.38
1 OPUS	1,110,716.04	660,577.12	567.70
20	1,110,781.93	660,548.18	567.44
30	1,111,120.30	660,435.94	567.85



It is a violation of New York Education Law Article 145 Sec.7209, for any person, unless acting under the direction of a licensed architect, professional engineer, or land surveyor, to alter an item in any way. If an item bearing the seal of an architect, engineer, or land surveyor is altered; the altering architect, engineer, or land surveyor shall affix to the item their seal and notation "altered by" followed by their signature and date of such alteration, and a specific description of the alteration.

Town of Palmyra

1180 Canandaigua Road
Palmyra, New York

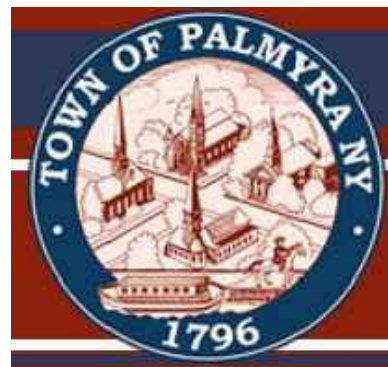

Landfill Closure Remediation


944 Garnsey Road
Palmyra, New York

NO:	DATE:	DESCRIPTION:
Revisions		

PROJECT NUMBER:	2242908
DRAWN BY:	IWW
REVIEWED BY:	DWT
ISSUED FOR:	CONSTRUCTION
DATE:	08/27/2024
DRAWING NAME:	

NOTES AND LEGEND SHEET

L:\Palmyra\dwg\2024 Closure\02 - existing conditions.dwg Layout=Layout1

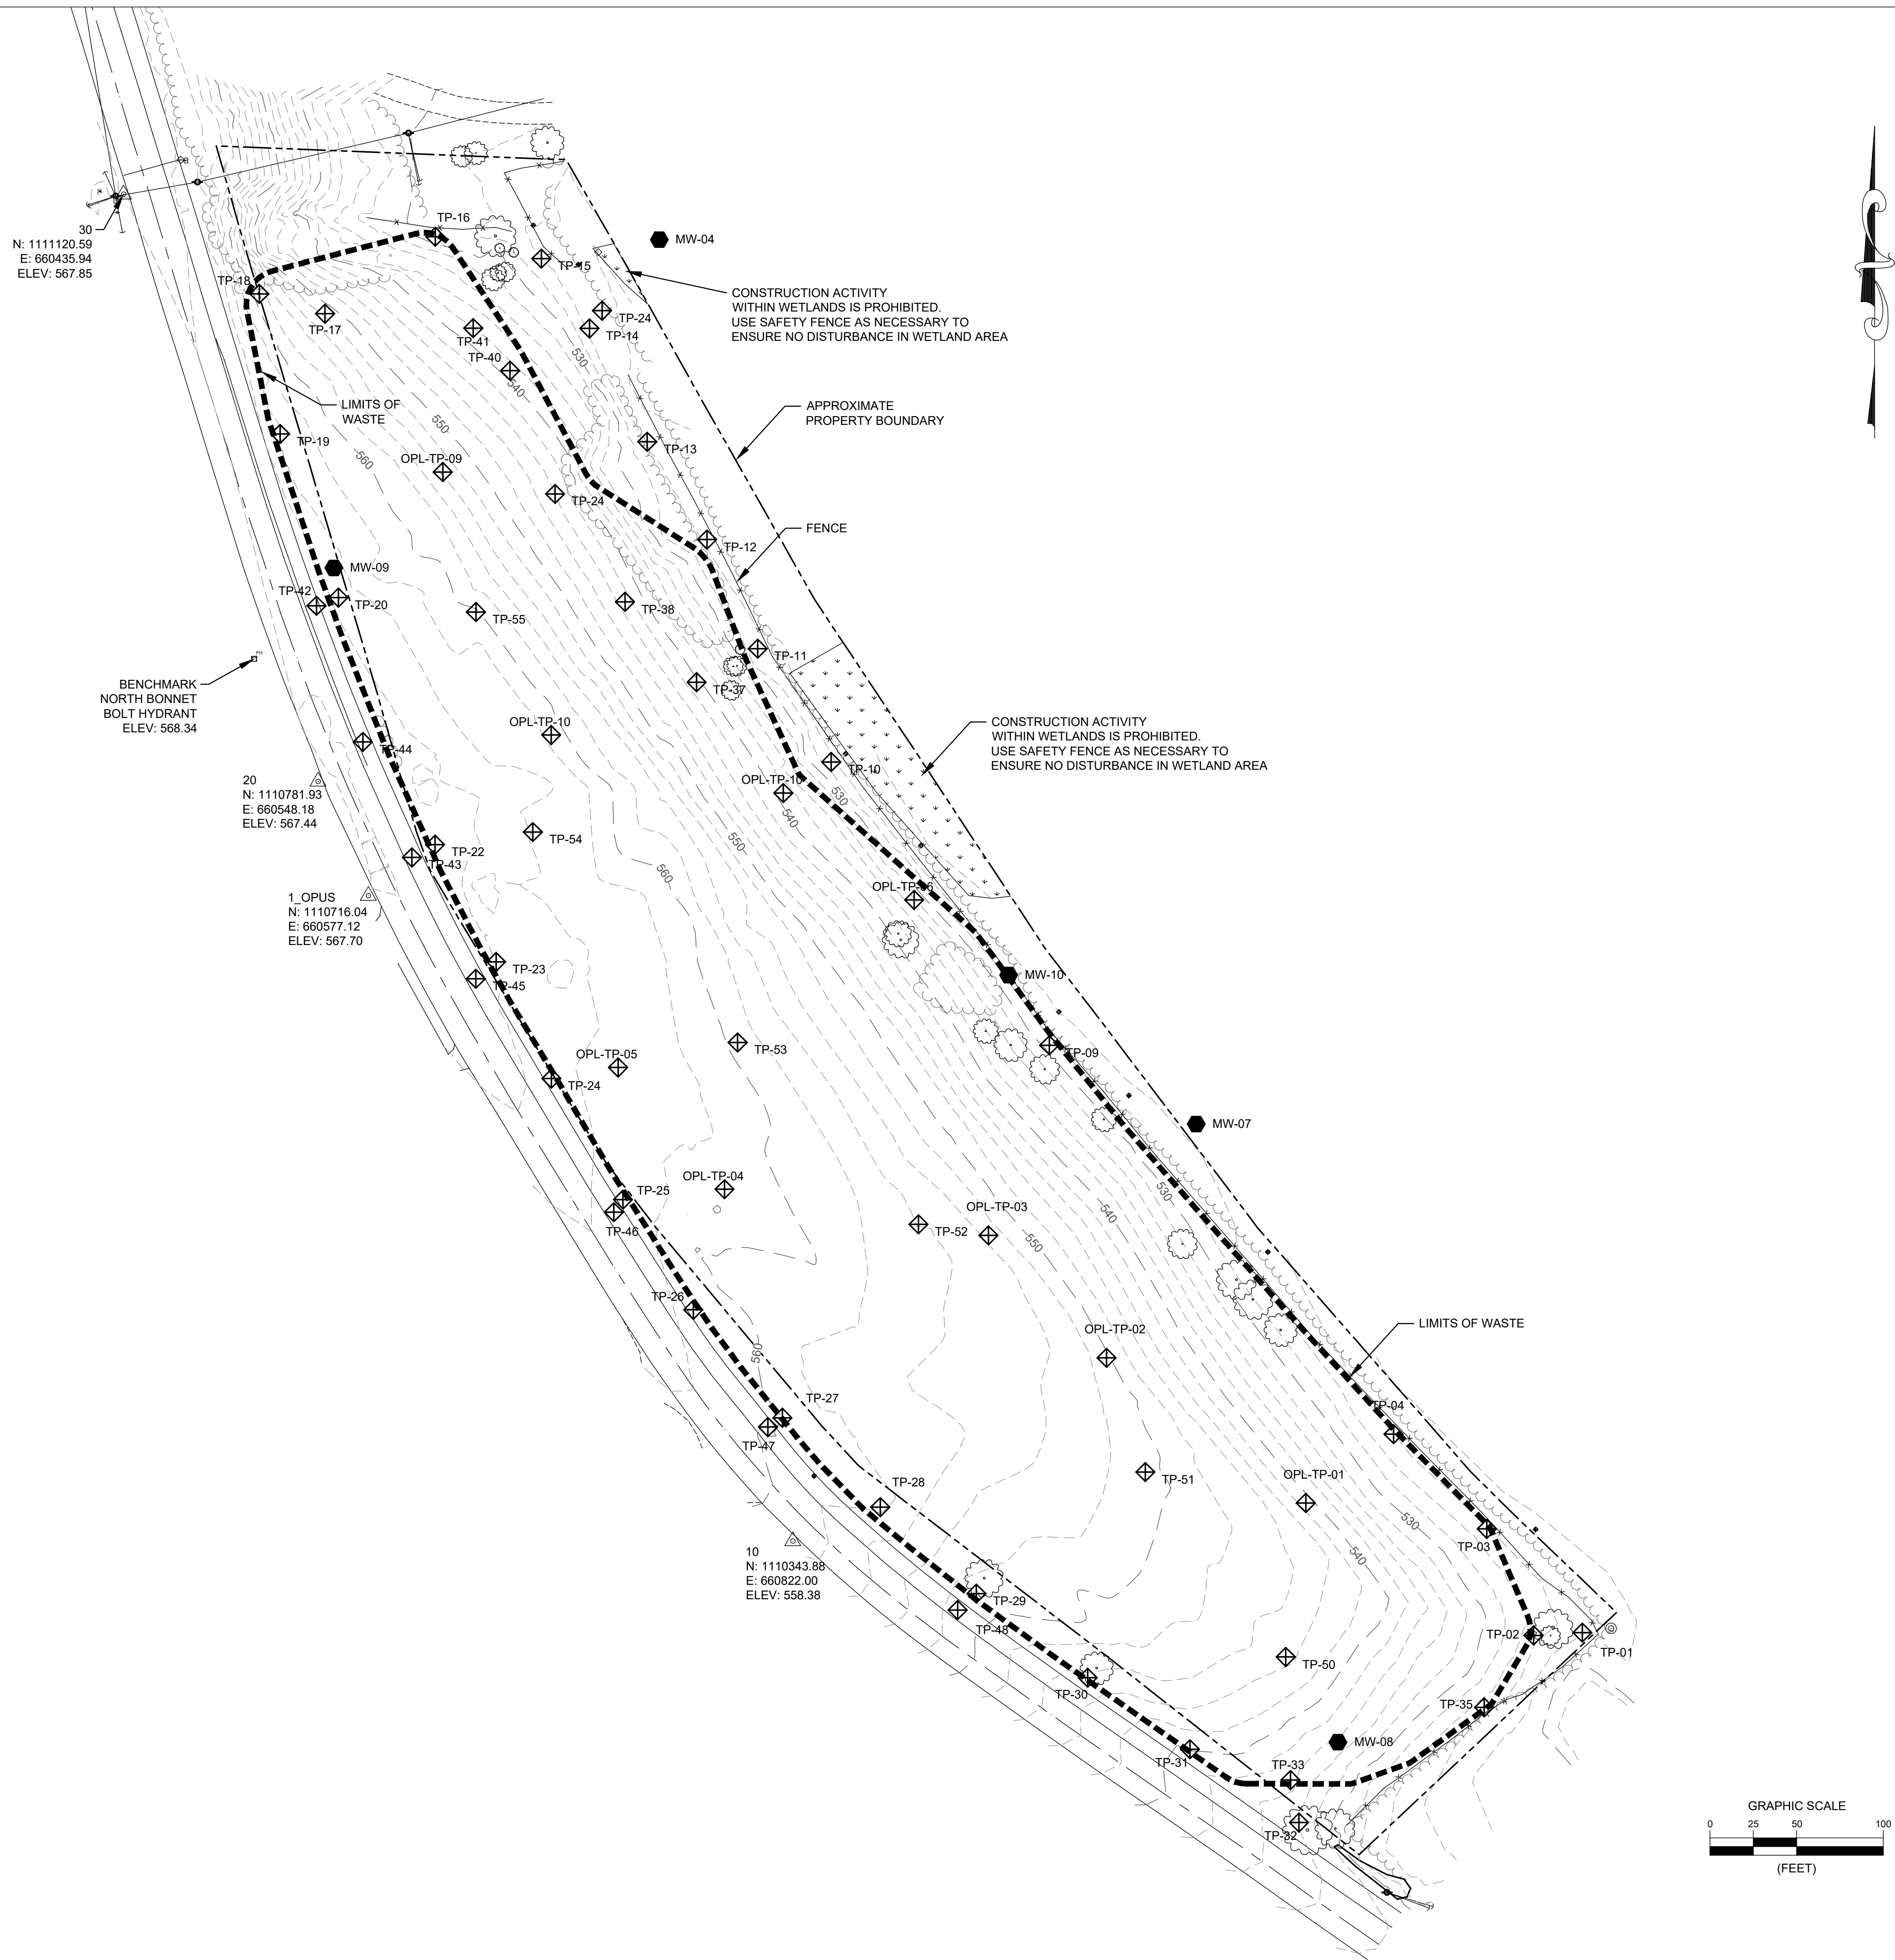

It is a violation of New York Education Law Article 145 Sec.7209, for any person, unless acting under the direction of a licensed architect, professional engineer, or land surveyor, to alter an item in any way. If an item bearing the seal of an architect, engineer, or land surveyor is altered; the altering architect, engineer, or land surveyor shall affix to the item their seal and notation "altered by" followed by their signature and date of such alteration, and a specific description of the alteration.

© 2024 LaBella Associates

Town of Palmyra

1180 Canandaigua Road
Palmyra, New York



Landfill Closure Remediation

944 Gamsey Road
Palmyra, New York


NO.	DATE:	DESCRIPTION:
Revisions		

PROJECT NUMBER:	2242908
DRAWN BY:	IWW
REVIEWED BY:	DWT
ISSUED FOR:	CONSTRUCTION
DATE:	08/27/2024
DRAWING NAME:	

EXISTING CONDITIONS

DRAWING NUMBER:

L:\Palmyra\dwg\2024 Closure\03 - base grading plan.dwg Layout=Layout1

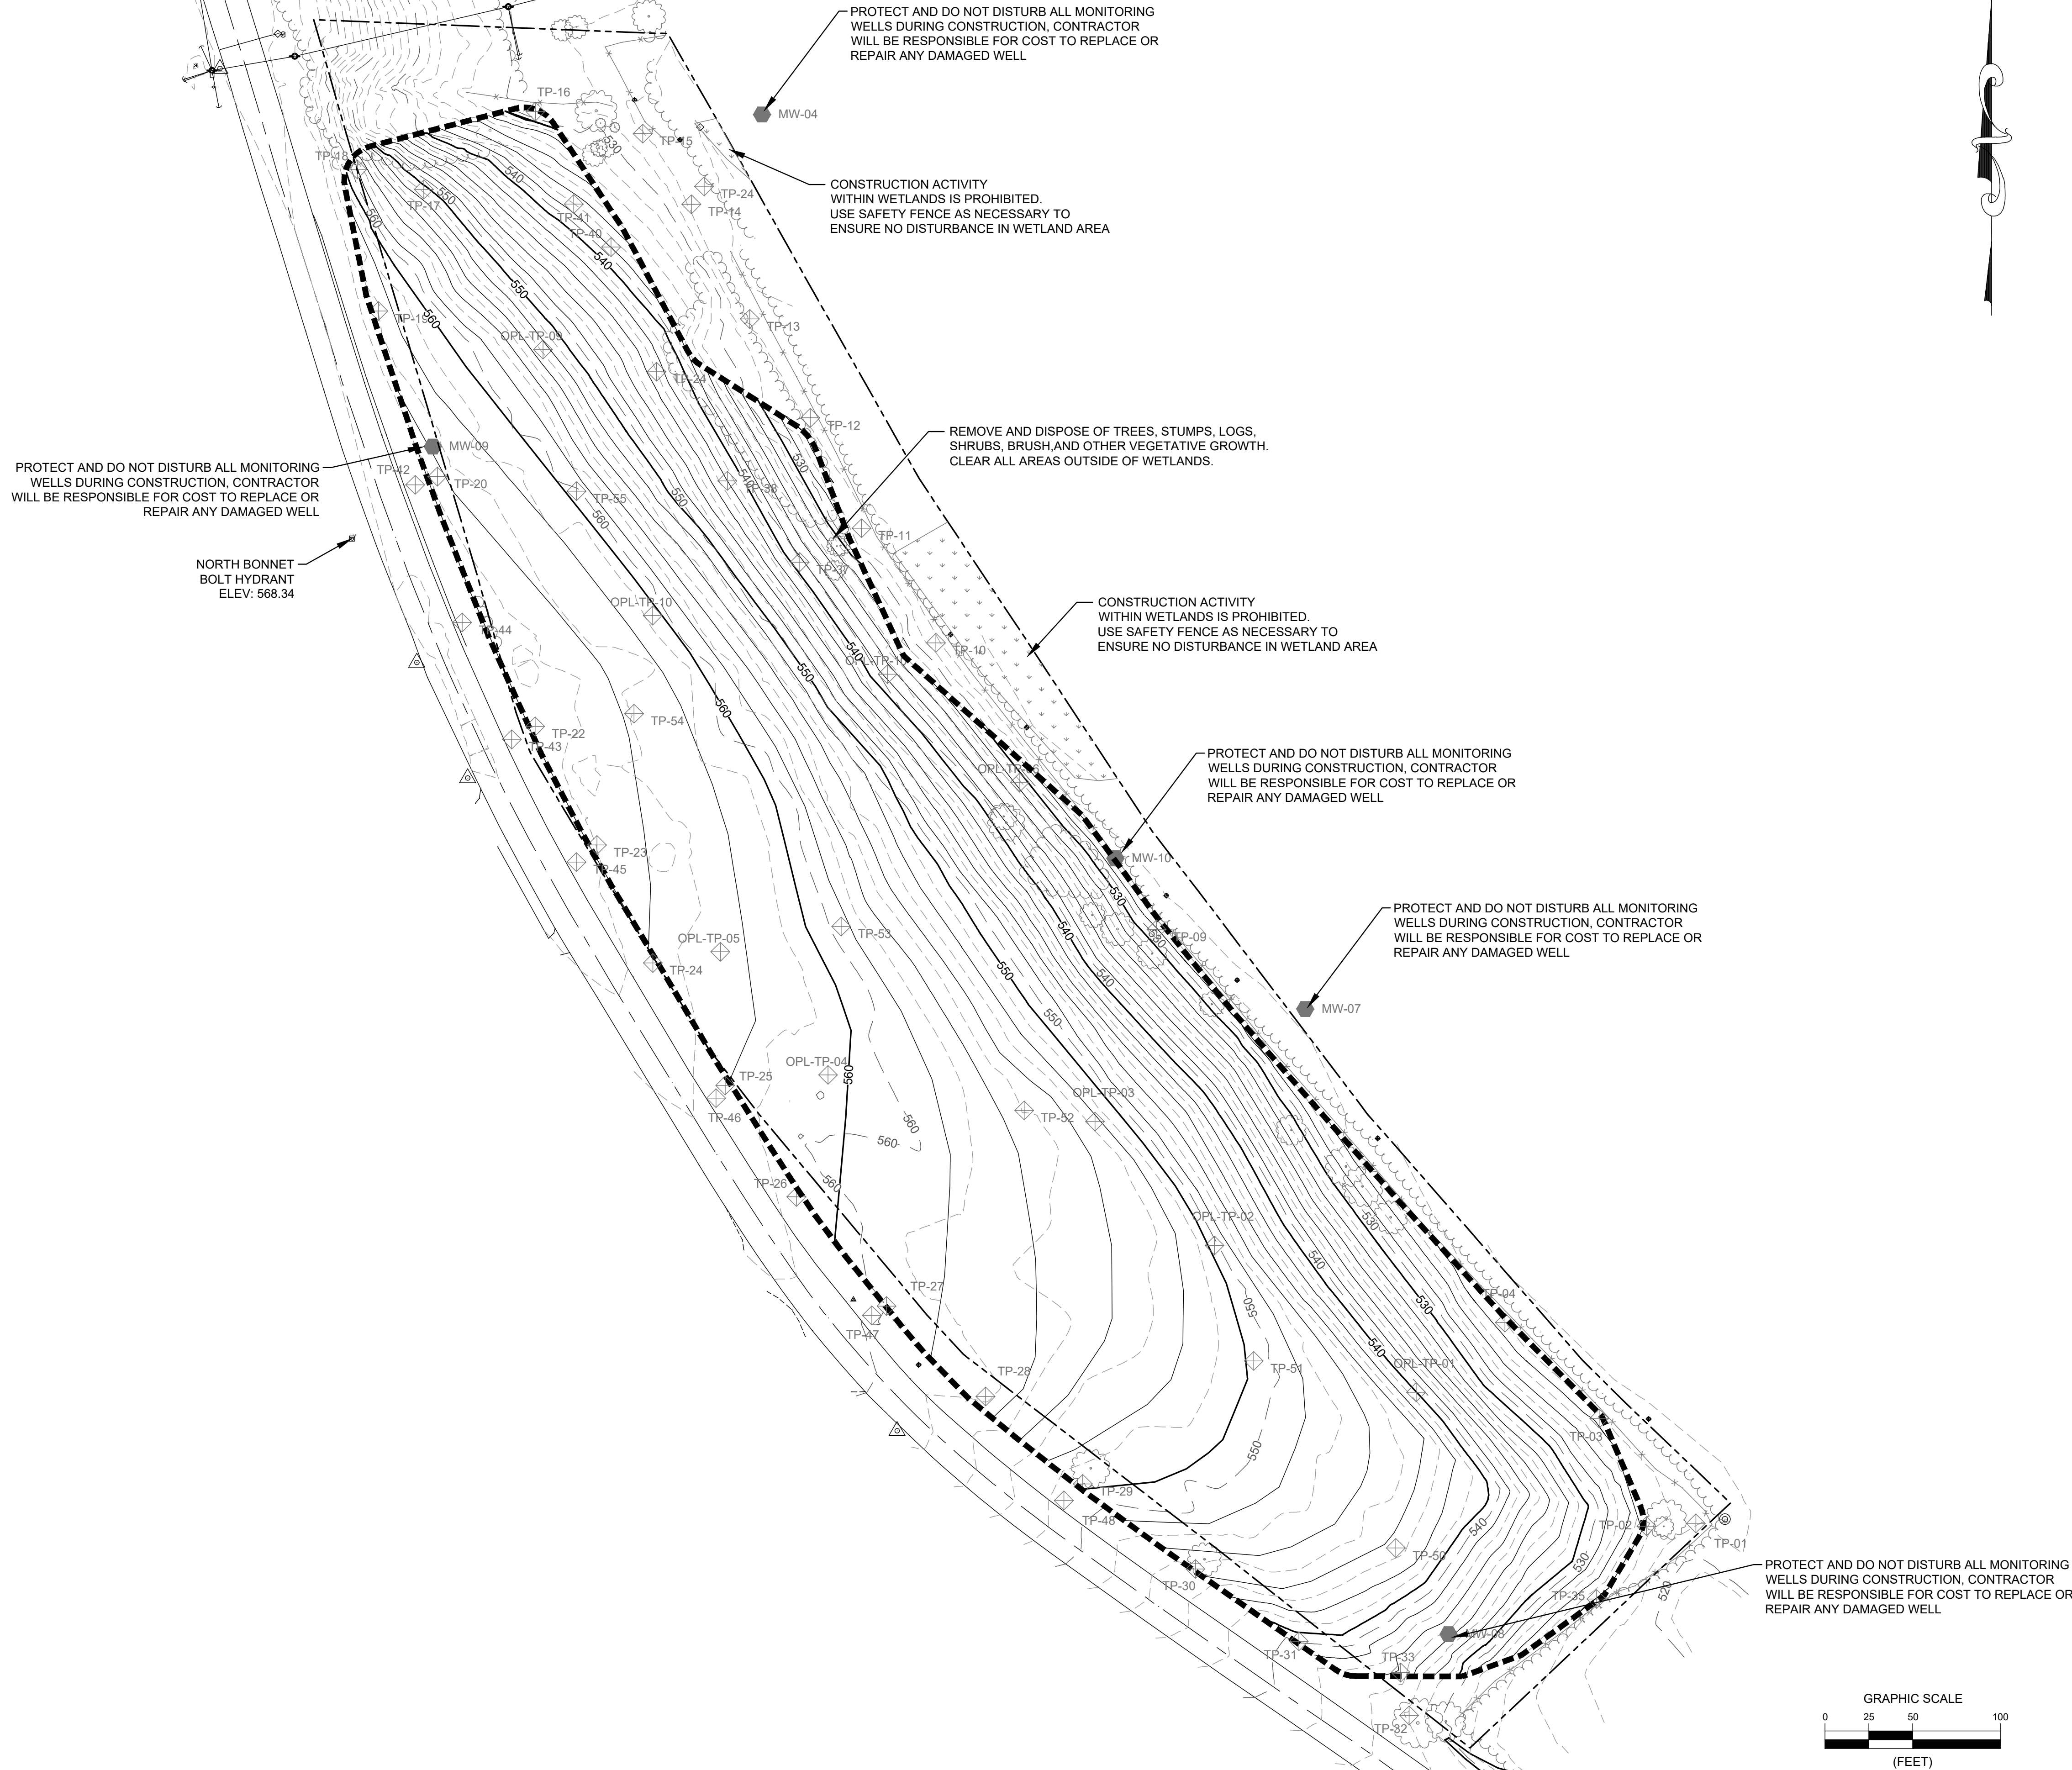

It is a violation of New York Education Law Article 145 Sec.7209, for any person, unless acting under the direction of a licensed architect, professional engineer, or land surveyor, to alter an item in any way. If an item bearing the seal of an architect, engineer, or land surveyor is altered; the altering architect, engineer, or land surveyor shall affix to the item their seal and notation "altered by" followed by their signature and date of such alteration, and a specific description of the alteration.

© 2024 LaBella Associates

Town of Palmyra

1180 Canandaigua Road
Palmyra, New York



Landfill Closure Remediation

944 Garnsey Road
Palmyra, New York

NO:	DATE:	DESCRIPTION:

Revisions

PROJECT NUMBER: 2242908

DRAWN BY: IWW

REVIEWED BY: DWT

ISSUED FOR: CONSTRUCTION


DATE: 08/27/2024

DRAWING NAME:

BASE GRADING PLAN

DRAWING NUMBER:

I:\csh\lab\Legacy\RICCADD\LANDZ PROJECTS\Palmyra\dwg\2024 Closure\04 - final grading plan.dwg Layout/Layout1

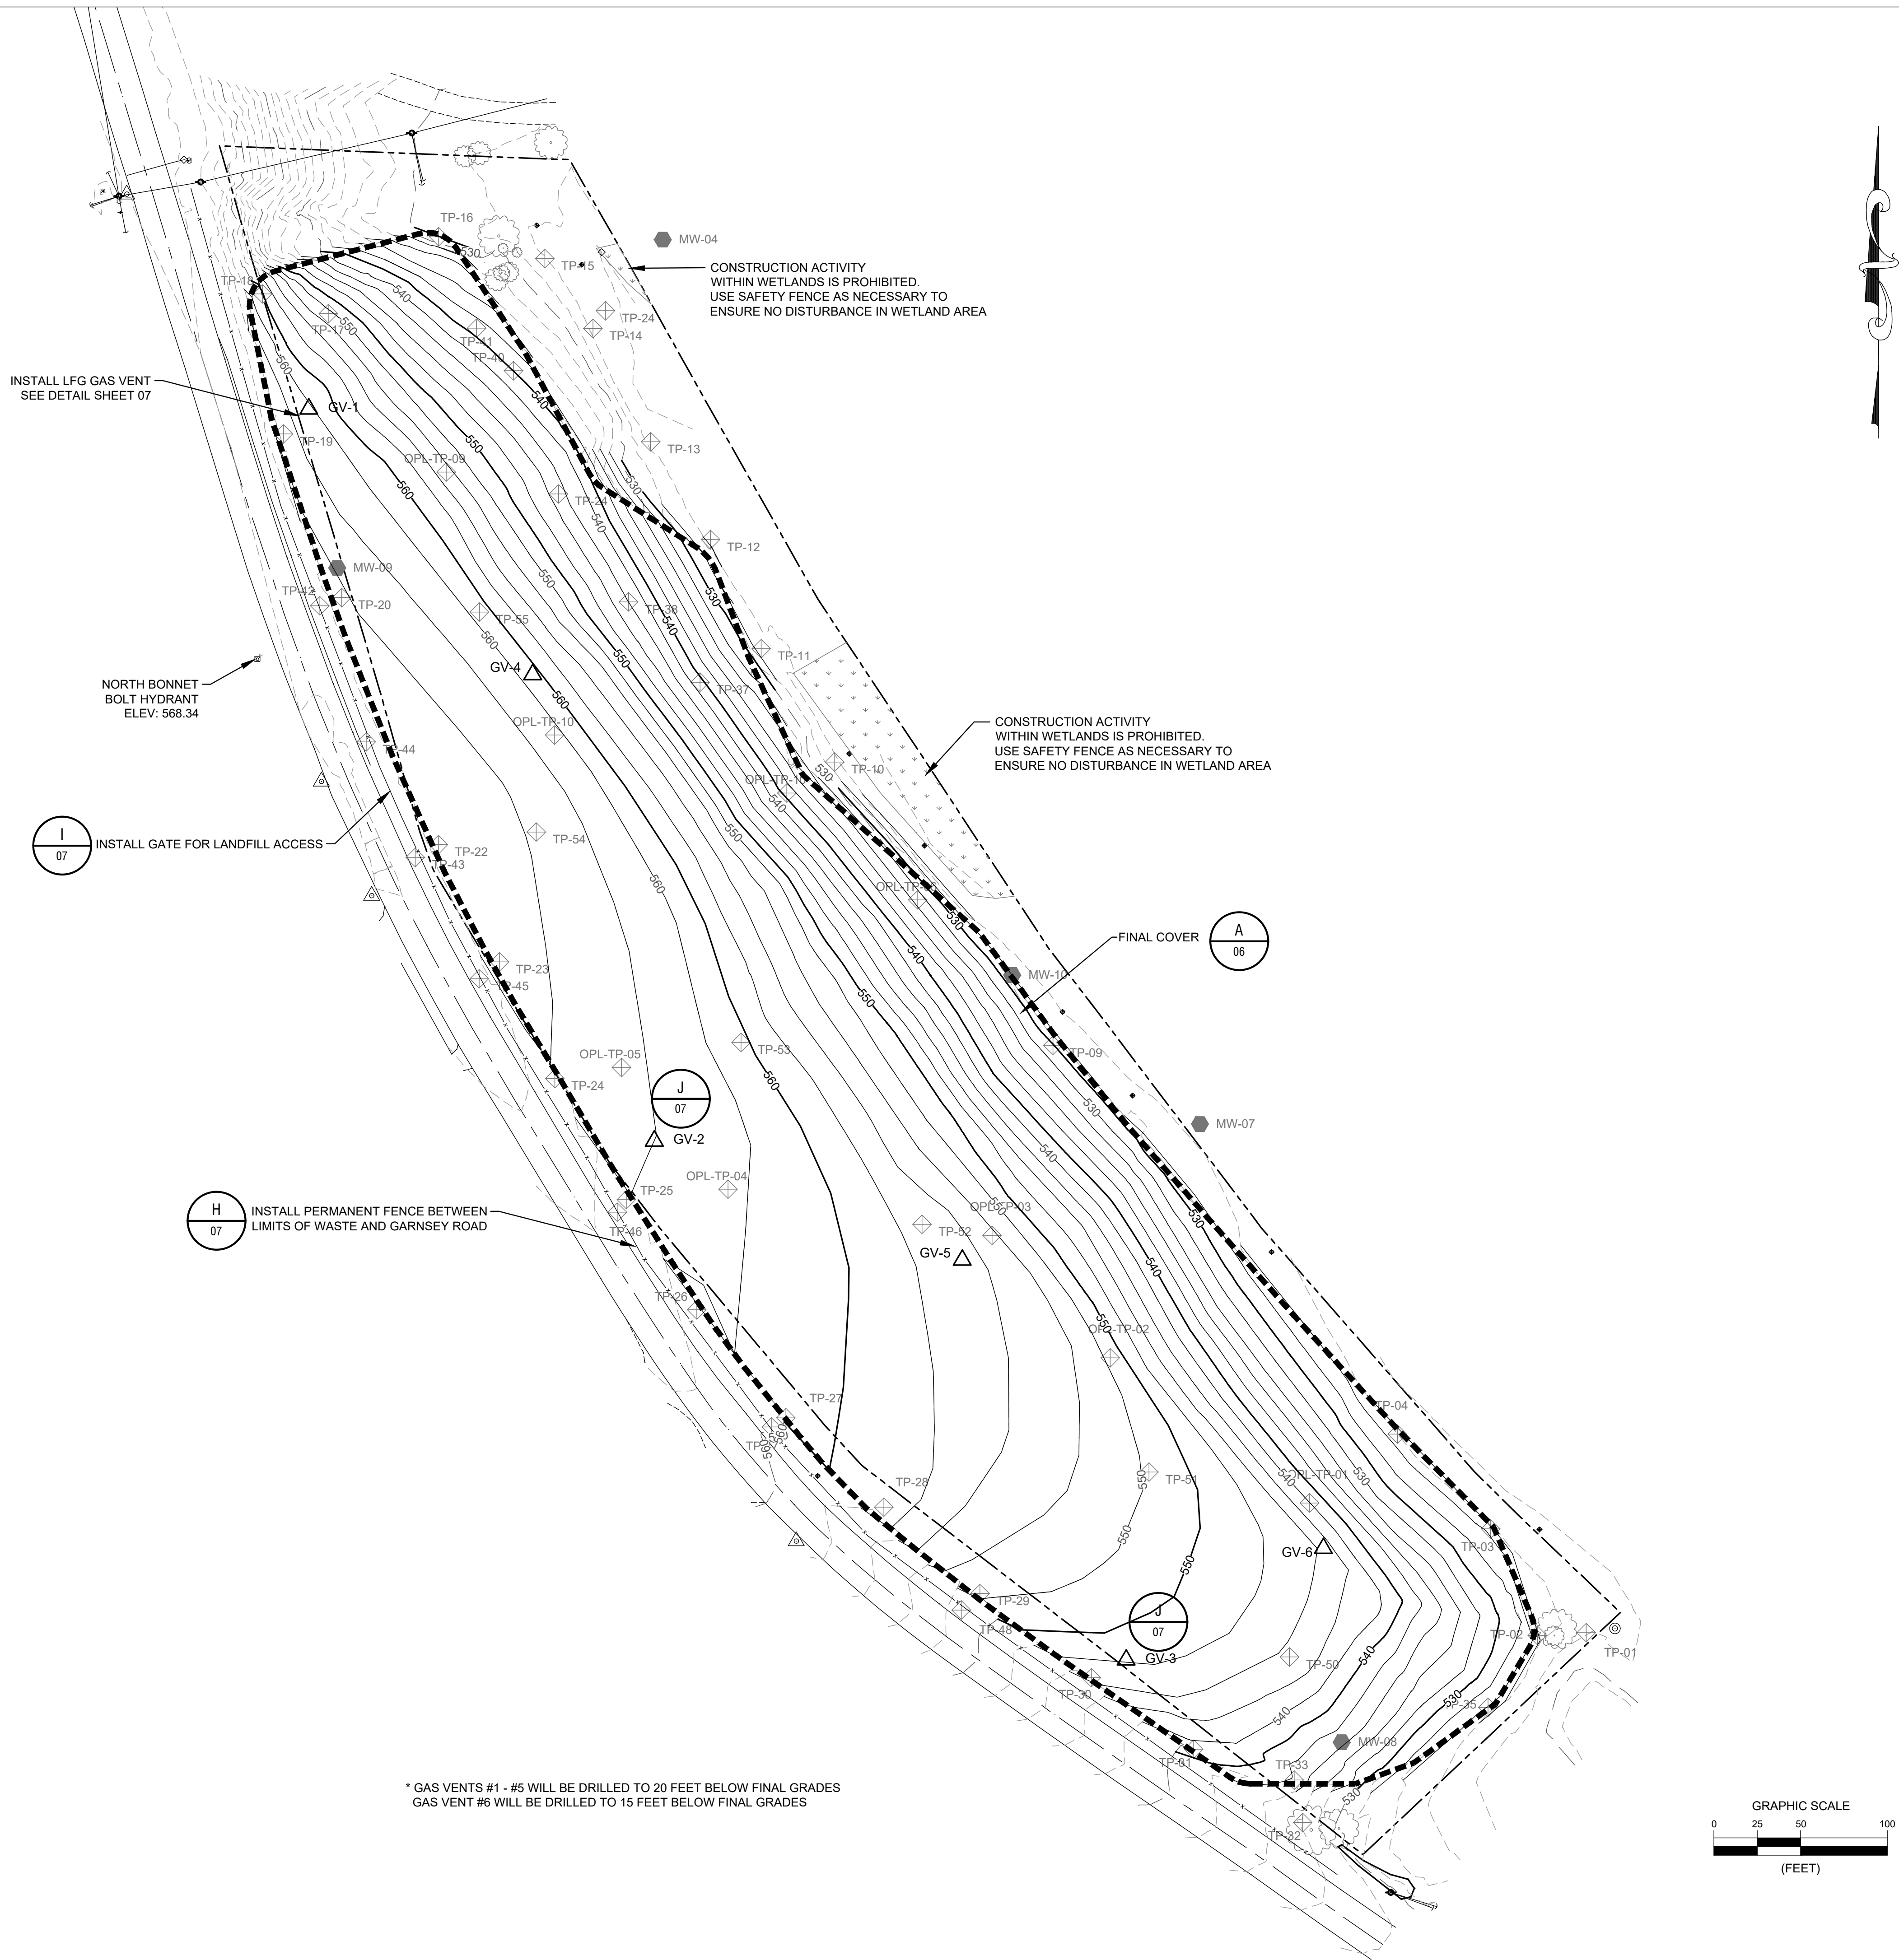

It is a violation of New York Education Law Article 145 Sec.7209, for any person, unless acting under the direction of a licensed architect, professional engineer, or land surveyor, to alter an item in any way. If an item bearing the seal of an architect, engineer, or land surveyor is altered; the altering architect, engineer, or land surveyor shall affix to the item their seal and notation "altered by" followed by their signature and date of such alteration, and a specific description of the alteration.

© 2024 LaBella Associates

Town of Palmyra

1180 Canandaigua Road
Palmyra, New York



Landfill Closure Remediation

944 Garnsey Road
Palmyra, New York

NO.	DATE:	DESCRIPTION:
Revisions		

PROJECT NUMBER: 2242908

DRAWN BY: --

REVIEWED BY: --

ISSUED FOR:


DATE: 08/09/2024

DRAWING NAME:

FINAL GRADING PLAN

DRAWING NUMBER:

\\ash.lab\Legacy\RICCADD\LAND2 PROJECTS\Palmyra\dwg\2024 Closure\05 - post erosion and sediment control plan.dwg Layout/Layout1

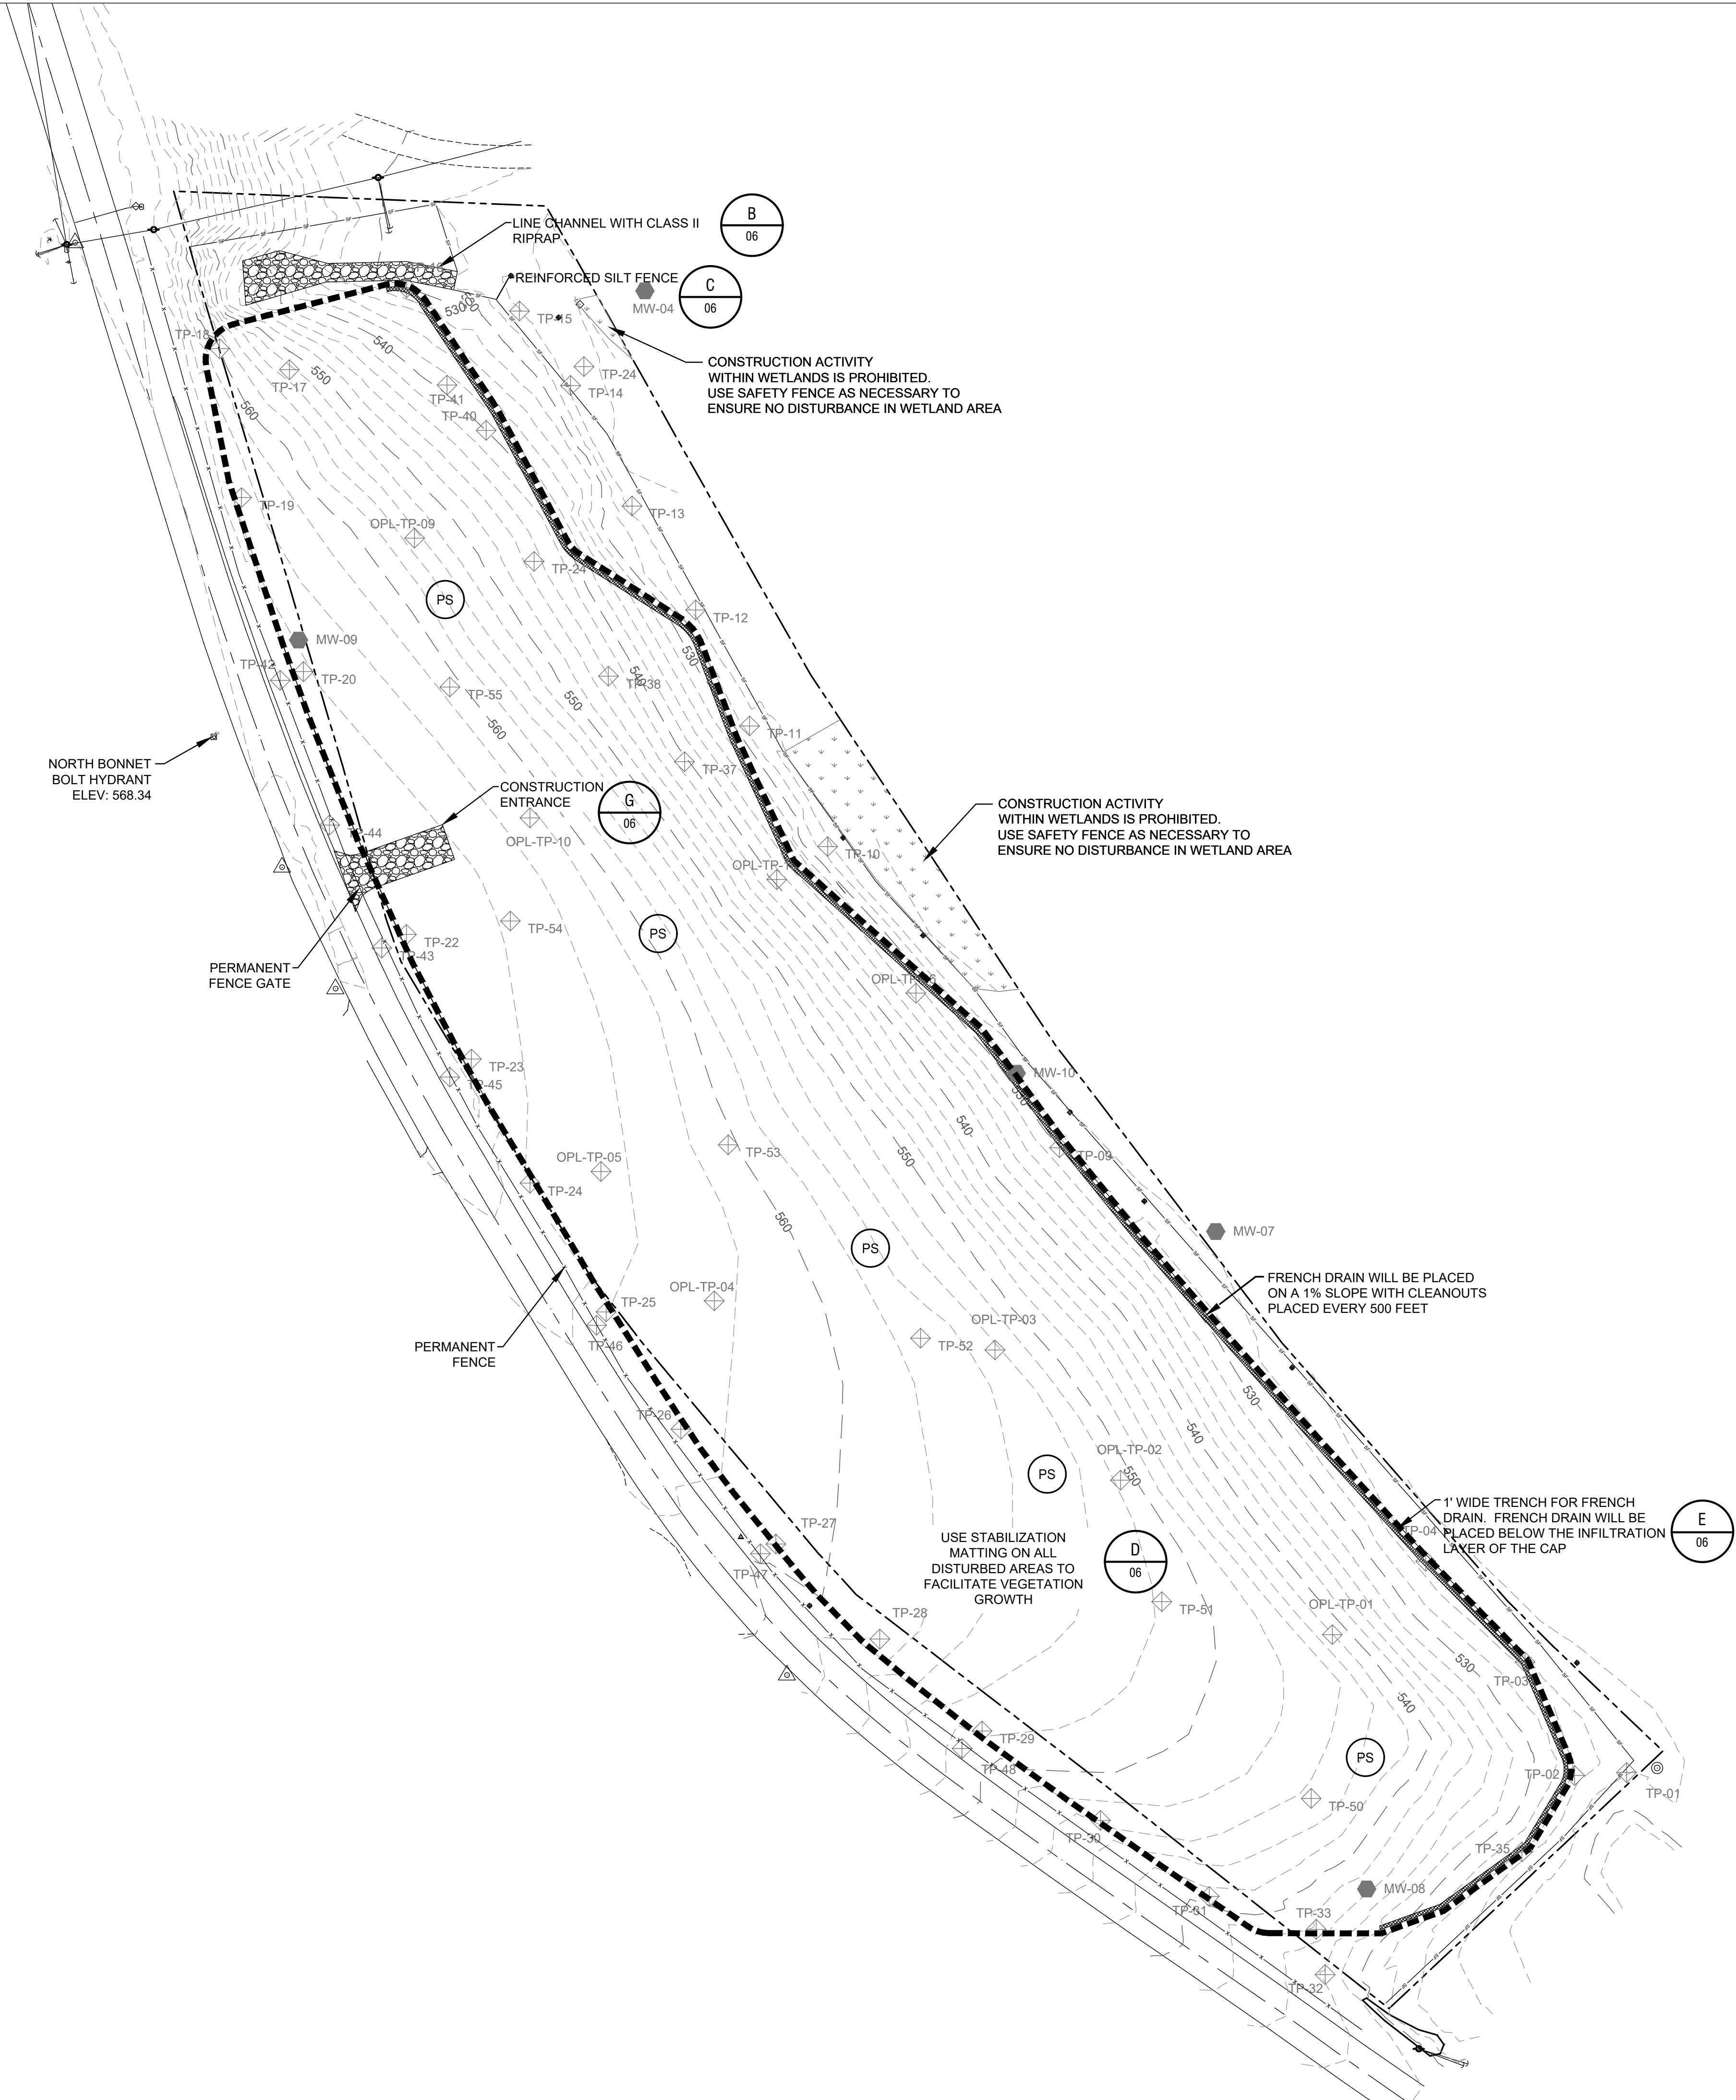

It is a violation of New York Education Law Article 145 Sec.7209, for any person, unless acting under the direction of a licensed architect, professional engineer, or land surveyor, to alter an item in any way. If an item bearing the seal of an architect, engineer, or land surveyor is altered; the altering architect, engineer, or land surveyor shall affix to the item their seal and notation "altered by" followed by their signature and date of such alteration, and a specific description of the alteration.

© 2024 LaBella Associates

Town of Palmyra

1189 Canandaigua Road
Palmyra, New York



Landfill Closure Remediation

944 Garnsey Road
Palmyra, New York

NO.	DATE:	DESCRIPTION:
Revisions		

PROJECT NUMBER:	2242908
DRAWN BY:	--
REVIEWED BY:	--
ISSUED FOR:	
DATE:	08/09/2024
DRAWING NAME:	

**POST EROSION AND
SEDIMENT CONTROL PLAN**

DRAWING NUMBER:

\\cassh.lab\l\Legacy\R\C\ADD\LAND2 PROJECTS\Palmyra\dwg\2024 Closure\06 - details.dwg Layout/Layout1


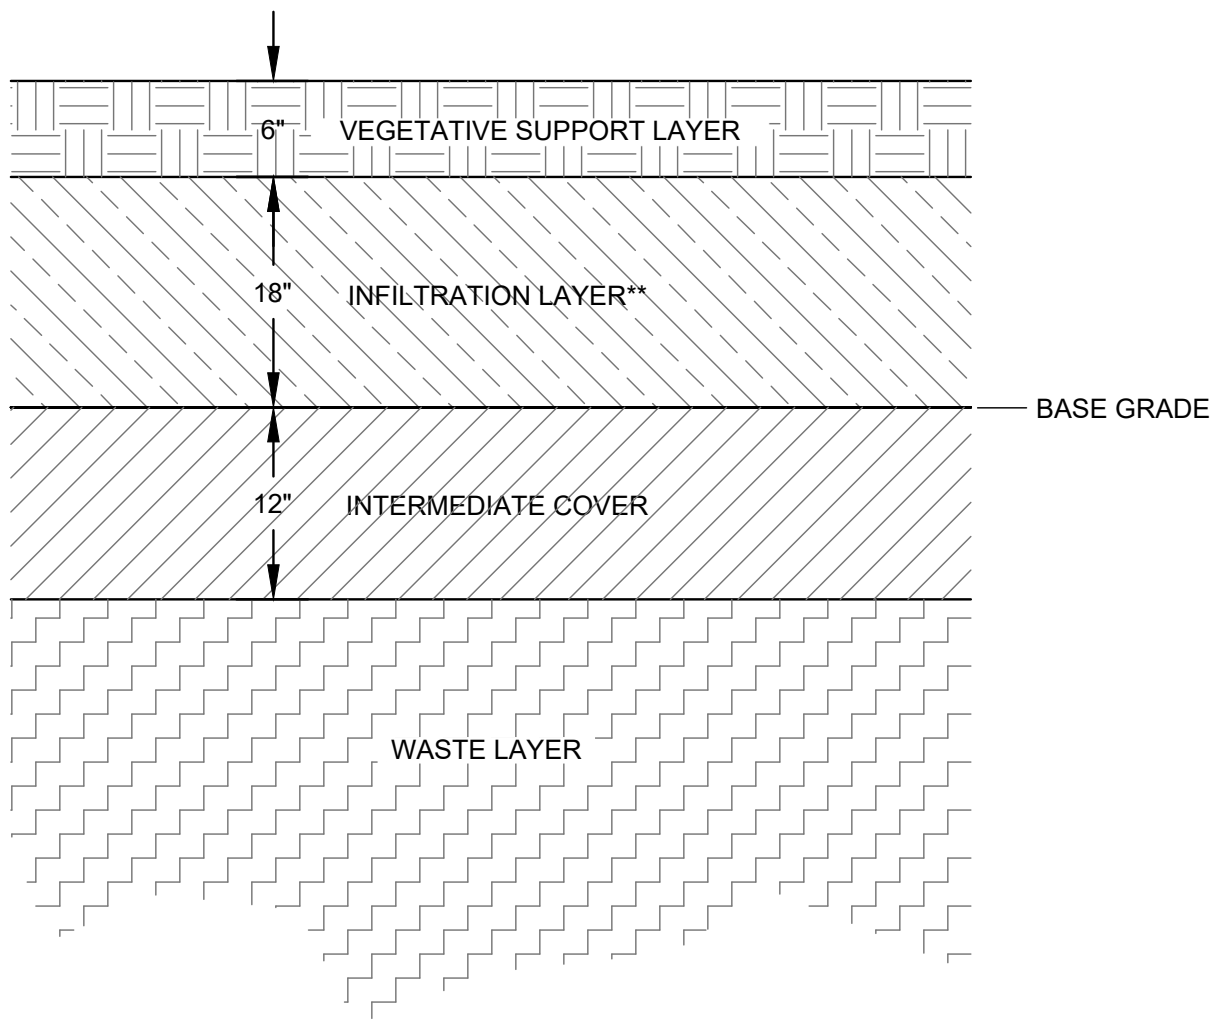


Figure 4.2
Typical Riprap Slope Protection Detail

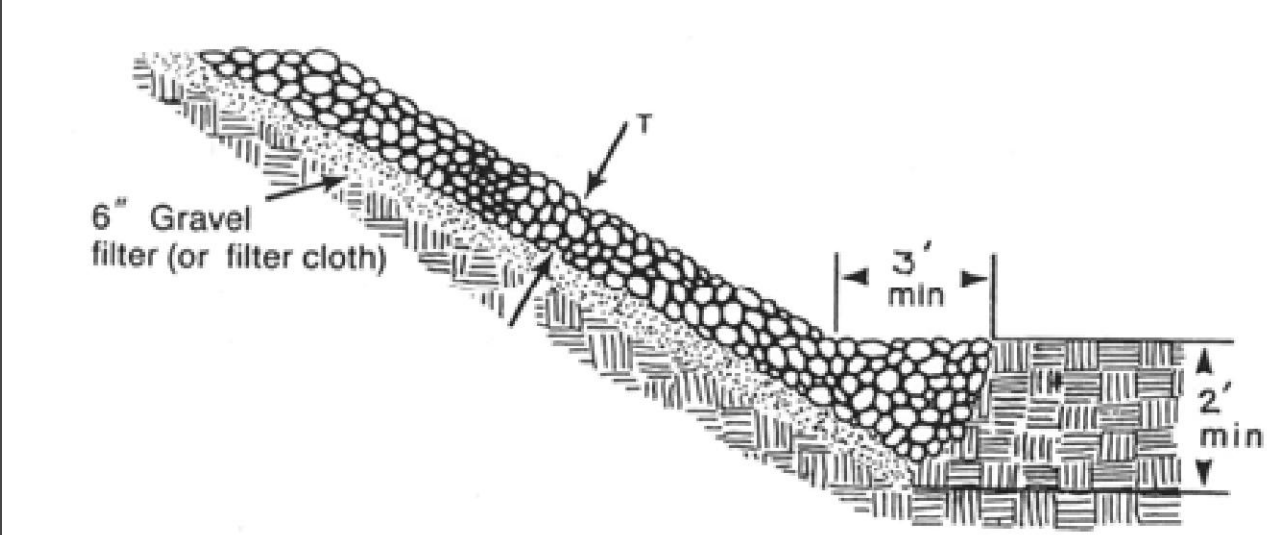

New York State Standards and Specifications
or Erosion and Sediment Control

Page 4.9

November 2016

CONSTRUCTION SPECIFICATIONS

1. SLOPE SHALL BE GRADED TO 2:1 OR FLATTER PRIOR TO PLACING FILTER, FILTER FABRIC, OR RIPRAP.
2. RIPRAP SHALL BE PLACED TO MAINTAIN A UNIFORM GRADATION. LARGER STONE SHALL BE PLACED AT THE TOE.
3. ENDS OF THE RIPRAP SHALL BE KEYED INTO A STABLE BANK. WHEN TYING INTO OTHER STRUCTURES, LARGER RIPRAP CAN BE LAID IN STEPS OR STACKED AS NEEDED TO FIT. STONES LARGER THAN THOSE DESIGNED FOR FLOW SHALL BE USED FOR THIS PURPOSE.
4. REMAINING DISTURBED AREAS SHALL BE GRADED AND PERMANENTLY SEEDED AND MULCHED.

ADAPTED FROM DETAILS PROVIDED BY: USDA - NRCS,
NEW YORK STATE DEPARTMENT OF TRANSPORTATION,
NEW YORK STATE DEPARTMENT OF ENVIRONMENTAL CONSERVATION,
NEW YORK STATE SOIL & WATER CONSERVATION COMMITTEE

RIPRAP
CHANNEL
STABILIZATION


Table 4.1 - Riprap Gradations for Channel Stabilization

Class	Layer Thickness (in.)	Max. Velocity (ft/s)	Wave Height (ft)	PERCENT FINER BY WEIGHT											
				D ₁₀			D ₅₀			D ₈₅			D ₁₀₀		
				Wt. (lbs.)	d _s (in.)	d ₁₀ (in.)	Wt. (lbs.)	d _s (in.)	d ₁₀ (in.)	Wt. (lbs.)	d _s (in.)	d ₁₀ (in.)	Wt. (lbs.)	d _s (in.)	d ₁₀ (in.)
I	18	8.5	-	5	5	4	50	10	8	100	13	10	150	15	12
II	18	10	-	17	7	6	170	15	12	340	19	15	500	22	18
III	24	12	2	46	10	8	460	21	17	920	26	21	1400	30	24
IV	36	14	3	150	15	12	1500	30	25	3000	39	32	4500	47	36
V	48	17	4.8	370	20	16	3700	42	34	7400	53	43	11,000	60	49


d_s = gravel material d₁₀ = angular rock riprap
Wt = weight in pounds

** INFILTRATION LAYER NEEDS TO BE A CLAYEY SOIL WITH A PERMEABILITY <= THAN 1X10⁻⁷ CM/S

A
06
FINAL COVER DETAIL
N.T.S.

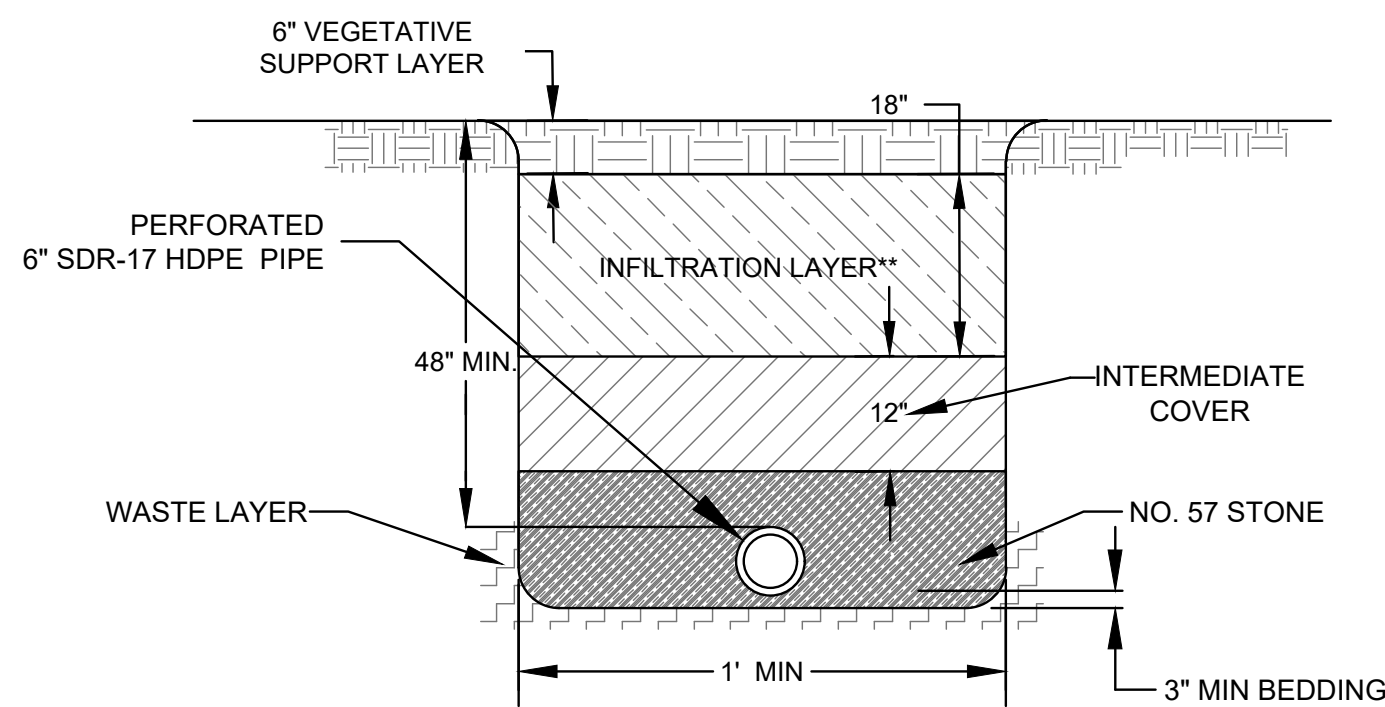


E
06
FRENCH DRAIN DETAIL (TYPICAL)
N.T.S.

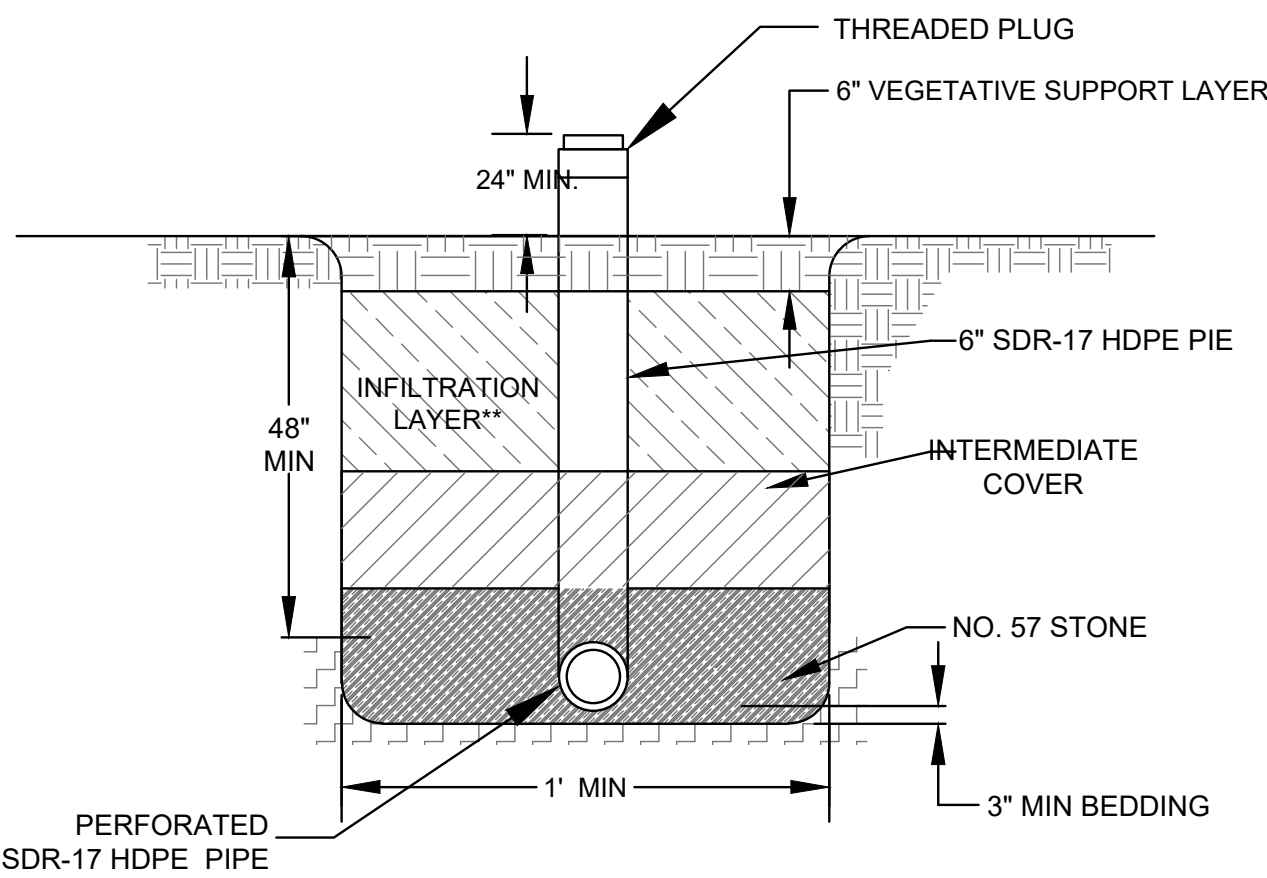

F
06
FRENCH DRAIN CLEANOUT DETAIL (TYPICAL)
N.T.S.

Figure 5.30
Reinforced Silt Fence

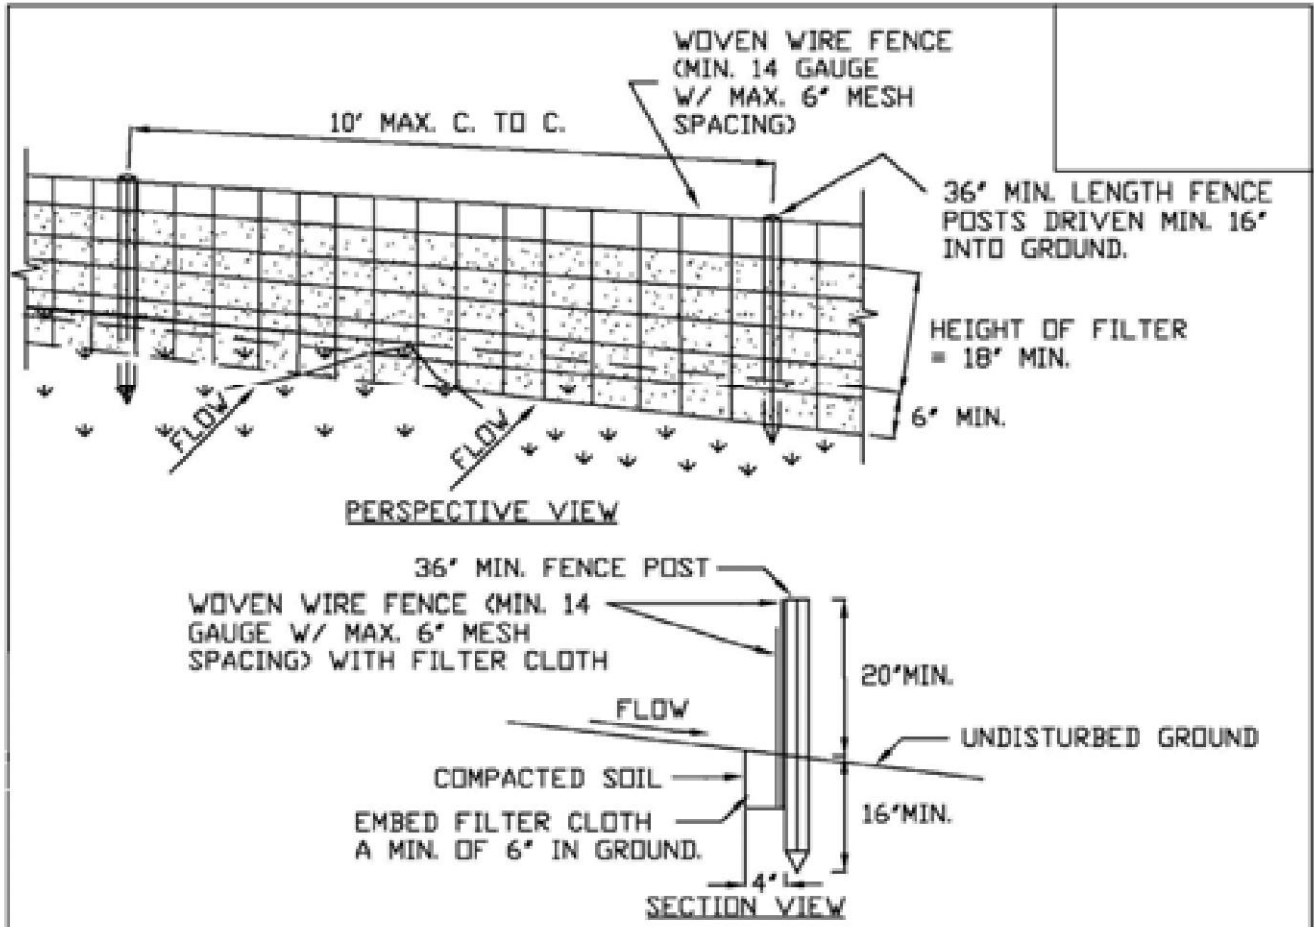

1. WOVEN WIRE FENCE TO BE FASTENED SECURELY TO FENCE POSTS WITH WIRE TIES OR STAPLES. POSTS SHALL BE STEEL EITHER 1" OR 1/2" TYPE OR HARDWOOD.
2. FILTER CLOTH TO BE FASTENED SECURELY TO WOVEN WIRE FENCE WITH TIES SPACED EVERY 24" AT TOP AND MID SECTION. FENCE SHALL BE WOVEN WIRE, 6" MAXIMUM MESH OPENING.
3. WHEN TWO SECTIONS OF FILTER CLOTH ADJOIN EACH OTHER THEY SHALL BE OVERLAPPED BY SIX INCHES AND FOLDED. FILTER CLOTH SHALL BE EITHER FILTER X, MIRAFI 100X, STABILINKA 1140N, OR APPROVED EQUIVALENT.
4. PREFABRICATED UNITS SHALL MEET THE MINIMUM REQUIREMENTS SHOWN.
5. MAINTENANCE SHALL BE PERFORMED AS NEEDED AND MATERIAL REMOVED WHEN "BULGES" DEVELOP IN THE SILT FENCE.

ADAPTED FROM DETAILS PROVIDED BY: USDA - NRCS,
NEW YORK STATE DEPARTMENT OF TRANSPORTATION,
NEW YORK STATE DEPARTMENT OF ENVIRONMENTAL CONSERVATION,
NEW YORK STATE SOIL & WATER CONSERVATION COMMITTEE

REINFORCED
SILT FENCE

November 2016


Page 5.56

New York State Standards and Specifications
For Erosion and Sediment Control

C
06
SILT FENCE DETAIL
N.T.S.

EROSION AND SEDIMENT CONTROL NOTES

1. ALL EROSION CONTROL MEASURES SHALL BE IN ACCORDANCE WITH NEW YORK STANDARDS AND SPECIFICATIONS FOR EROSION AND SEDIMENT CONTROL, AND LOCAL GOVERNING SOIL AND WATER CONSERVATION AGENCY RECOMMENDATIONS AND STANDARDS. CONTRACTOR SHALL SUBMIT PROPOSED EROSION CONTROL PLAN INCLUDING SEQUENCING OF WORK TO THE ENGINEER FOR REVIEW PRIOR TO START OF WORK.
2. UTILIZE CONSTRUCTION METHODS/TECHNIQUES, WHICH WILL LIMIT THE EXPOSED EARTHEN AREAS AND MINIMIZE THE EFFECT OF EARTH DISTURBANCE ACTIVITIES ON SOIL EROSION. THE AREA OF DISTURBANCE SHALL BE LIMITED TO A MAXIMUM OF 5 ACRES UNLESS OTHERWISE APPROVED BY THE ENGINEER.
3. ALL SEDIMENTATION BARRIERS AND OTHER TEMPORARY OR PERMANENT MEASURES SHALL BE IN PLACE PRIOR TO THE START OF CONSTRUCTION. PLANS SHOW THE SUGGESTED MINIMUM MEASURES REQUIRED.
4. REMOVAL OF ALL TEMPORARY EROSION AND SEDIMENTATION CONTROL MEASURES SHALL BE COMPLETED AT THE APPROVAL OF THE OWNER AND ENGINEER. THE COST OF REMOVING THESE MEASURES SHALL ALSO BE INCLUDED IN THE BID PRICE.
5. FOR THE DURATION OF THE PROJECT, THE CONTRACTOR SHALL PROTECT ALL ON-SITE, ADJACENT AND/OR DOWNSTREAM STORM/SANITARY SEWERS, AND/OR OTHER WATER COURSES FROM CONTAMINATION BY WATER BORNE SILTS, SEDIMENTS, FUELS, SOLVENTS, LUBRICANTS OR OTHER POLLUTANTS ORIGINATING FROM ANY WORK DONE ON, OR IN SUPPORT OF THIS PROJECT.
6. DURING CONSTRUCTION NO WET OR FRESH CONCRETE OR LEACHATE SHALL BE ALLOWED TO ESCAPE INTO STORM/SANITARY SEWERS, DITCHES OR OTHER WATERS OF NEW YORK STATE. NOR SHALL WASHINGS FROM CONCRETE TRUCKS, MIXERS OR OTHER DEVICES BE ALLOWED TO ENTER ANY STORM/SANITARY SEWERS, DITCHES, RIVERS, OR WATER COURSES.
7. ALL EXCAVATED OR IMPORTED EARTHEN STOCKPILES SHALL BE SUITABLY STABILIZED AND PROTECTED BY SILT FENCE SO THAT IT CANNOT REASONABLY ENTER ANY WATER BODY, OR STORM OR SANITARY SEWER.
8. ALL METHODS AND EQUIPMENT PROPOSED BY THE CONTRACTOR TO ACCOMPLISH THE WORK FOR EROSION AND POLLUTION CONTROL SHALL BE SUBJECT TO APPROVAL OF THE ENGINEER.
9. THE CONTRACTOR SHALL BE REQUIRED TO TREAT TRAVELED AREAS TO CONTROL DUST AND KEEP GARNSEY ROAD CLEAR OF CONSTRUCTION DEBRIS AND SEDIMENT. WATER SHALL BE APPLIED TO SUCH TRAVELED AREAS AS THE ARCHITECT/ENGINEER OR OWNER'S DESIGNATED REPRESENTATIVE MAY DESIGNATE. THE NUMBER OF APPLICATIONS AND THE AMOUNT OF WATER SHALL BE BASED UPON FIELD AND WEATHER CONDITIONS.
10. ALL AREAS OF SOIL DISTURBANCE RESULTING FROM THIS PROJECT WHICH WILL NOT BE SUBJECT TO FURTHER EARTHWORK OR CONSTRUCTION ACTIVITIES SHALL BE PERMANENTLY SEEDED TO ESTABLISH GRASS, AND MULCHED WITH HAY OR STRAW WITHIN ONE WEEK OF FINAL DISTURBANCE. MULCH SHALL BE MAINTAINED UNTIL A SUITABLE VEGETATIVE COVER IS ESTABLISHED.
11. CONTRACTOR STAGING AREAS AND CONSTRUCTION ENTRANCE LOCATIONS SHALL BE COORDINATED WITH THE OWNER PRIOR TO START OF CONSTRUCTION. STABILIZED CONSTRUCTION ENTRANCE(S), AS SHOWN ON THE PLANS SHALL BE PROVIDED. ALL DISTURBED AREAS SHALL BE RESTORED.
12. CONTRACTOR SHALL NOT DISTURB OR PERFORM ANY CONSTRUCTION ACTIVITY IN WETLAND AREA.
13. TILL ALL COMPACTED SOILS LOCATED IN LAWN AREAS TO RESTORE THE ORIGINAL PROPERTIES OF THE SOIL PRIOR TO SEEDING.

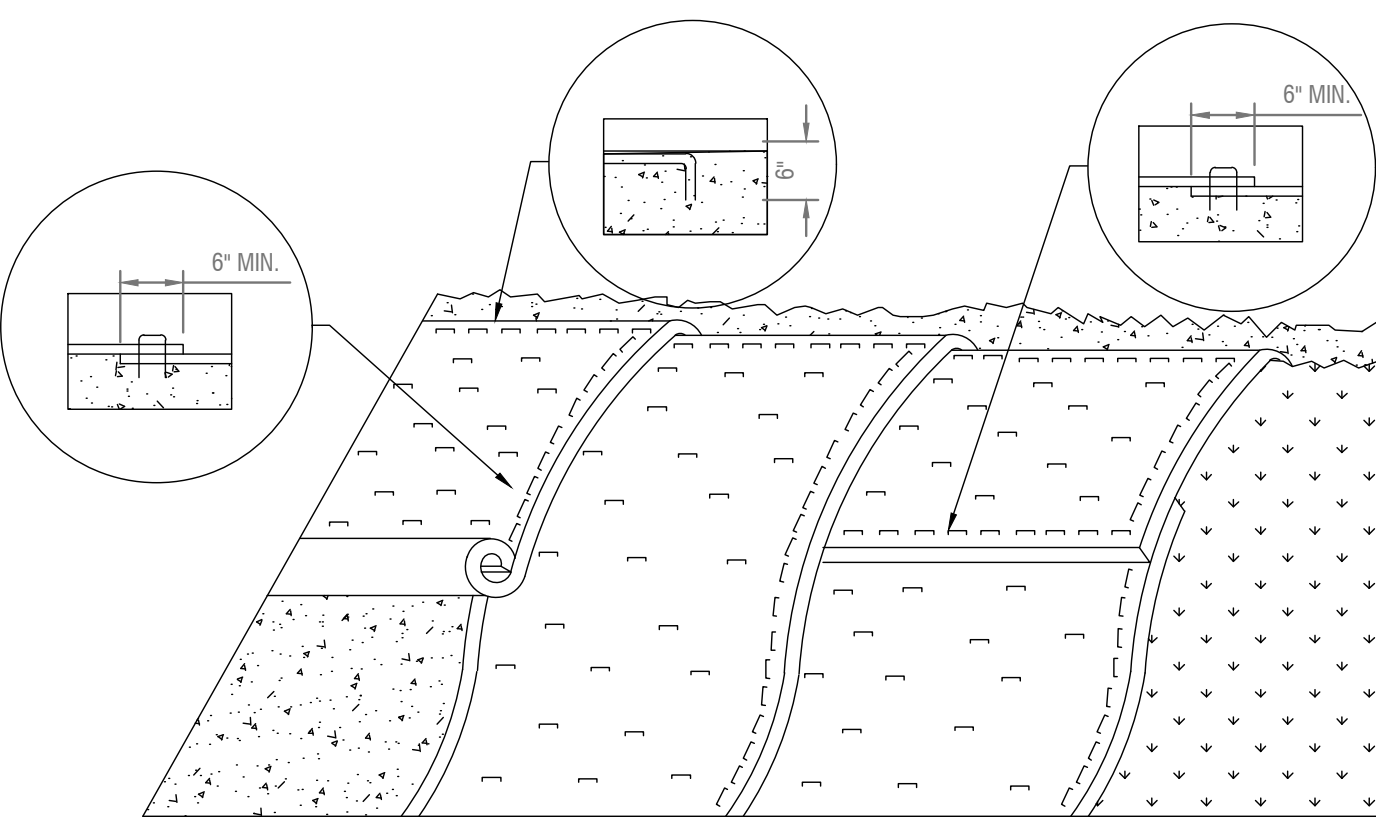

APPLICATION NOTES:


- A. THE PURPOSE OF EROSION MATTING ON SLOPES IS TO REDUCE EROSION AND AID THE ESTABLISHMENT OF VEGETATION
- B. EROSION CONTROL MATTING SHALL BE USED FOR THE FOLLOWING REASONS:
 - * SLOPES GREATER THAN 5:1 V OR WHERE ORDERED BY ENGINEER
 - * AREAS WHERE SEED AND MULCH WILL NOT STAY IN PLACE ALONE
 - * WHERE SEEDING IS OUTSIDE THE GROWING SEASON.

GENERAL NOTES:

1. GRADE AND SMOOTH THE SLOPE TO PROVIDE GOOD MATTING TO SOIL SURFACE CONTACT.
2. APPLY FERTILIZER, LIME, AND SEED PRIOR TO PLACING MATTING.
3. ANCHOR MATTING AS SHOWN, UTILIZING ANCHOR STAPLES. STAPLE PLACEMENT SHALL BE DETERMINED BY THE MANUFACTURERS INSTALLATION INSTRUCTIONS.
4. UNROLL EROSION MATTING VERTICALLY DOWN SLOPE IN THE DIRECTION OF WATER FLOW.
5. OVERLAP UPPER MATTING OVER LOWER MATTING AS SHOWN, AND AS DIRECTED BY MANUFACTURER.
6. OVERLAP ADJACENT MATTING AS SHOWN, AND AS DIRECTED BY MANUFACTURER.
7. CUT EXCESS MATTING AT END OF SLOPE AND ANCHOR THE END.
8. EROSION MATTING SHALL BE INSPECTED EVERY SEVEN (7) CALENDAR DAYS AND WITHIN 24 HOURS OF A STORM EVENT OF 1/2" OR GREATER.
9. EROSION MATTING SHALL BE REPAIRED AND RESTAPLED AS NECESSARY TO ENSURE PROPER FUNCTION.

D
06
ROLLED EROSION CONTROL PRODUCT
N.T.S.

Figure 2.1
Stabilized Construction Access

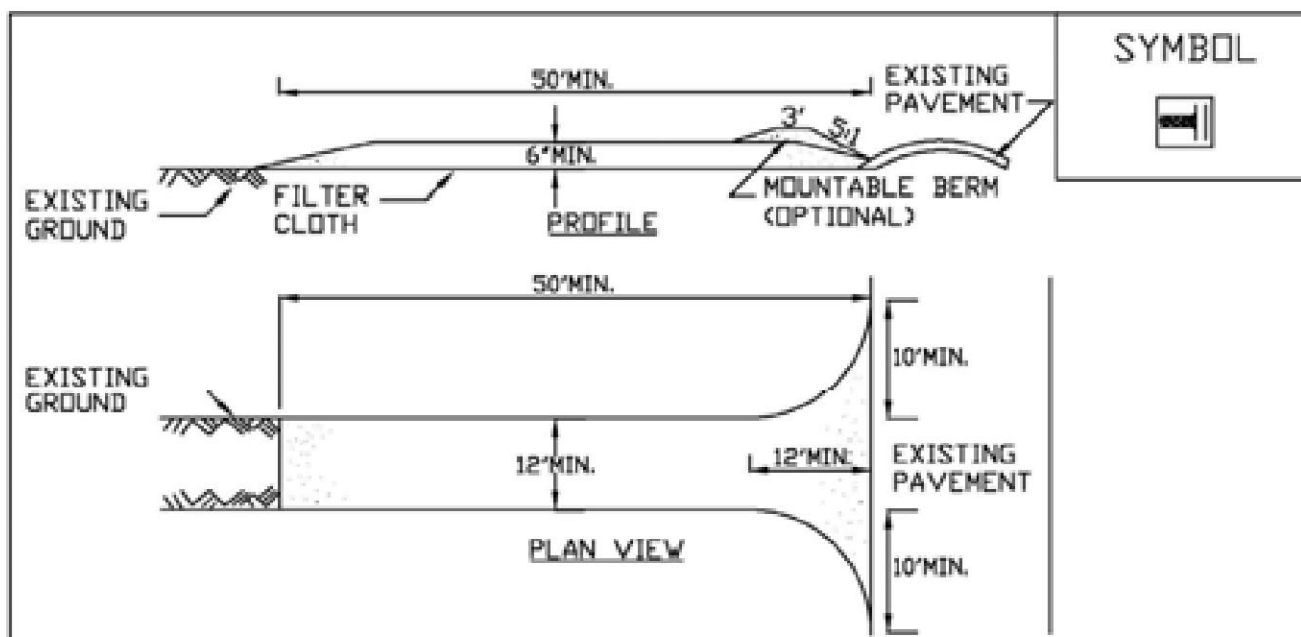

CONSTRUCTION SPECIFICATIONS

1. STONE SIZE - USE 1-4 INCH STONE, OR RECLAIMED OR RECYCLED CONCRETE EQUIVALENT.
2. LENGTH - NOT LESS THAN 50 FEET (EXCEPT ON A SINGLE RESIDENCE LOT WHERE A 30 FOOT MINIMUM LENGTH WOULD APPLY).
3. THICKNESS - NOT LESS THAN SIX (6) INCHES.
4. WIDTH - TWELVE (12) FOOT MINIMUM, BUT NOT LESS THAN THE FULL WIDTH AT POINTS WHERE INGRESS OR EGRESS OCCURS. TWENTY-FOUR (24) FOOT IF SINGLE ENTRANCE TO SITE.
5. GEOTEXTILE - WILL BE PLACED OVER THE ENTIRE AREA PRIOR TO PLACING OF STONE.
6. SURFACE WATER - ALL SURFACE WATER FLOWING OR DIVERTED TOWARD CONSTRUCTION ACCESS SHALL BE PIPED BENEATH THE ENTRANCE. IF PIPING IS IMPRACTICAL, A MOUNTABLE BERM WITH 5:1 SLOPES WILL BE PERMITTED.
7. MAINTENANCE - THE ENTRANCE SHALL BE MAINTAINED IN A CONDITION WHICH WILL PREVENT TRACKING OR FLOWING OF SEDIMENT ONTO PUBLIC RIGHTS-OF-WAY, ALL SEDIMENT SPILLED, DROPPED, WASHED OR TRACKED ONTO PUBLIC RIGHTS-OF-WAY MUST BE REMOVED IMMEDIATELY.
8. WHEN WASHING IS REQUIRED, IT SHALL BE DONE ON A AREA STABILIZED WITH STONE AND WHICH DRAINS INTO AN APPROVED SEDIMENT TRAPPING DEVICE.
9. PERIODIC INSPECTION AND NEEDED MAINTENANCE SHALL BE PROVIDED AFTER EACH RAIN.

ADAPTED FROM DETAILS PROVIDED BY: USDA - NRCS,
NEW YORK STATE DEPARTMENT OF TRANSPORTATION,
NEW YORK STATE DEPARTMENT OF ENVIRONMENTAL CONSERVATION,
NEW YORK STATE SOIL & WATER CONSERVATION COMMITTEE

STABILIZED
CONSTRUCTION
ACCESS

New York State Standards and Specifications
For Erosion and Sediment Control

Page 2.31

November 2016


G
06
STABILIZED CONSTRUCTION ACCESS DETAIL
N.T.S.



It is a violation of New York Education Law Article 145 Sec. 7209, for any person, unless acting under the direction of a licensed architect, professional engineer, or land surveyor, to alter an item in any way. If an item bearing the seal of an architect, engineer, or land surveyor is altered; the altering architect, engineer, or land surveyor shall affix to the item their seal and notation "altered by" followed by their signature and date of such alteration, and a specific description of the alteration.

Town of Palmyra

1180 Canandaigua Road
Palmyra, New York

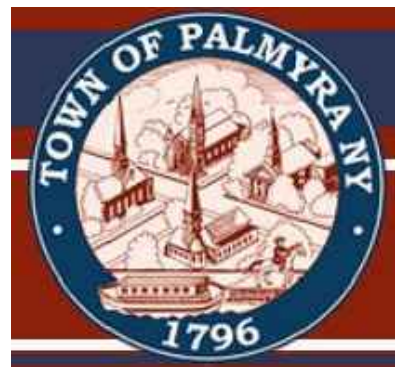

Landfill Closure Remediation

944 Garnsey Road
Palmyra, New York

NO:	DATE:	DESCRIPTION:

Revisions

PROJECT NUMBER: 2242908

DRAWN BY: --

REVIEWED BY: --

ISSUED FOR:


DATE: 08/09/2024

DRAWING NAME:


E&S NOTES AND DETAILS

DRAWING NUMBER:


L:\Palmyra\dwg\2024 Closure\06 - details.dwg Layout-Layout 2

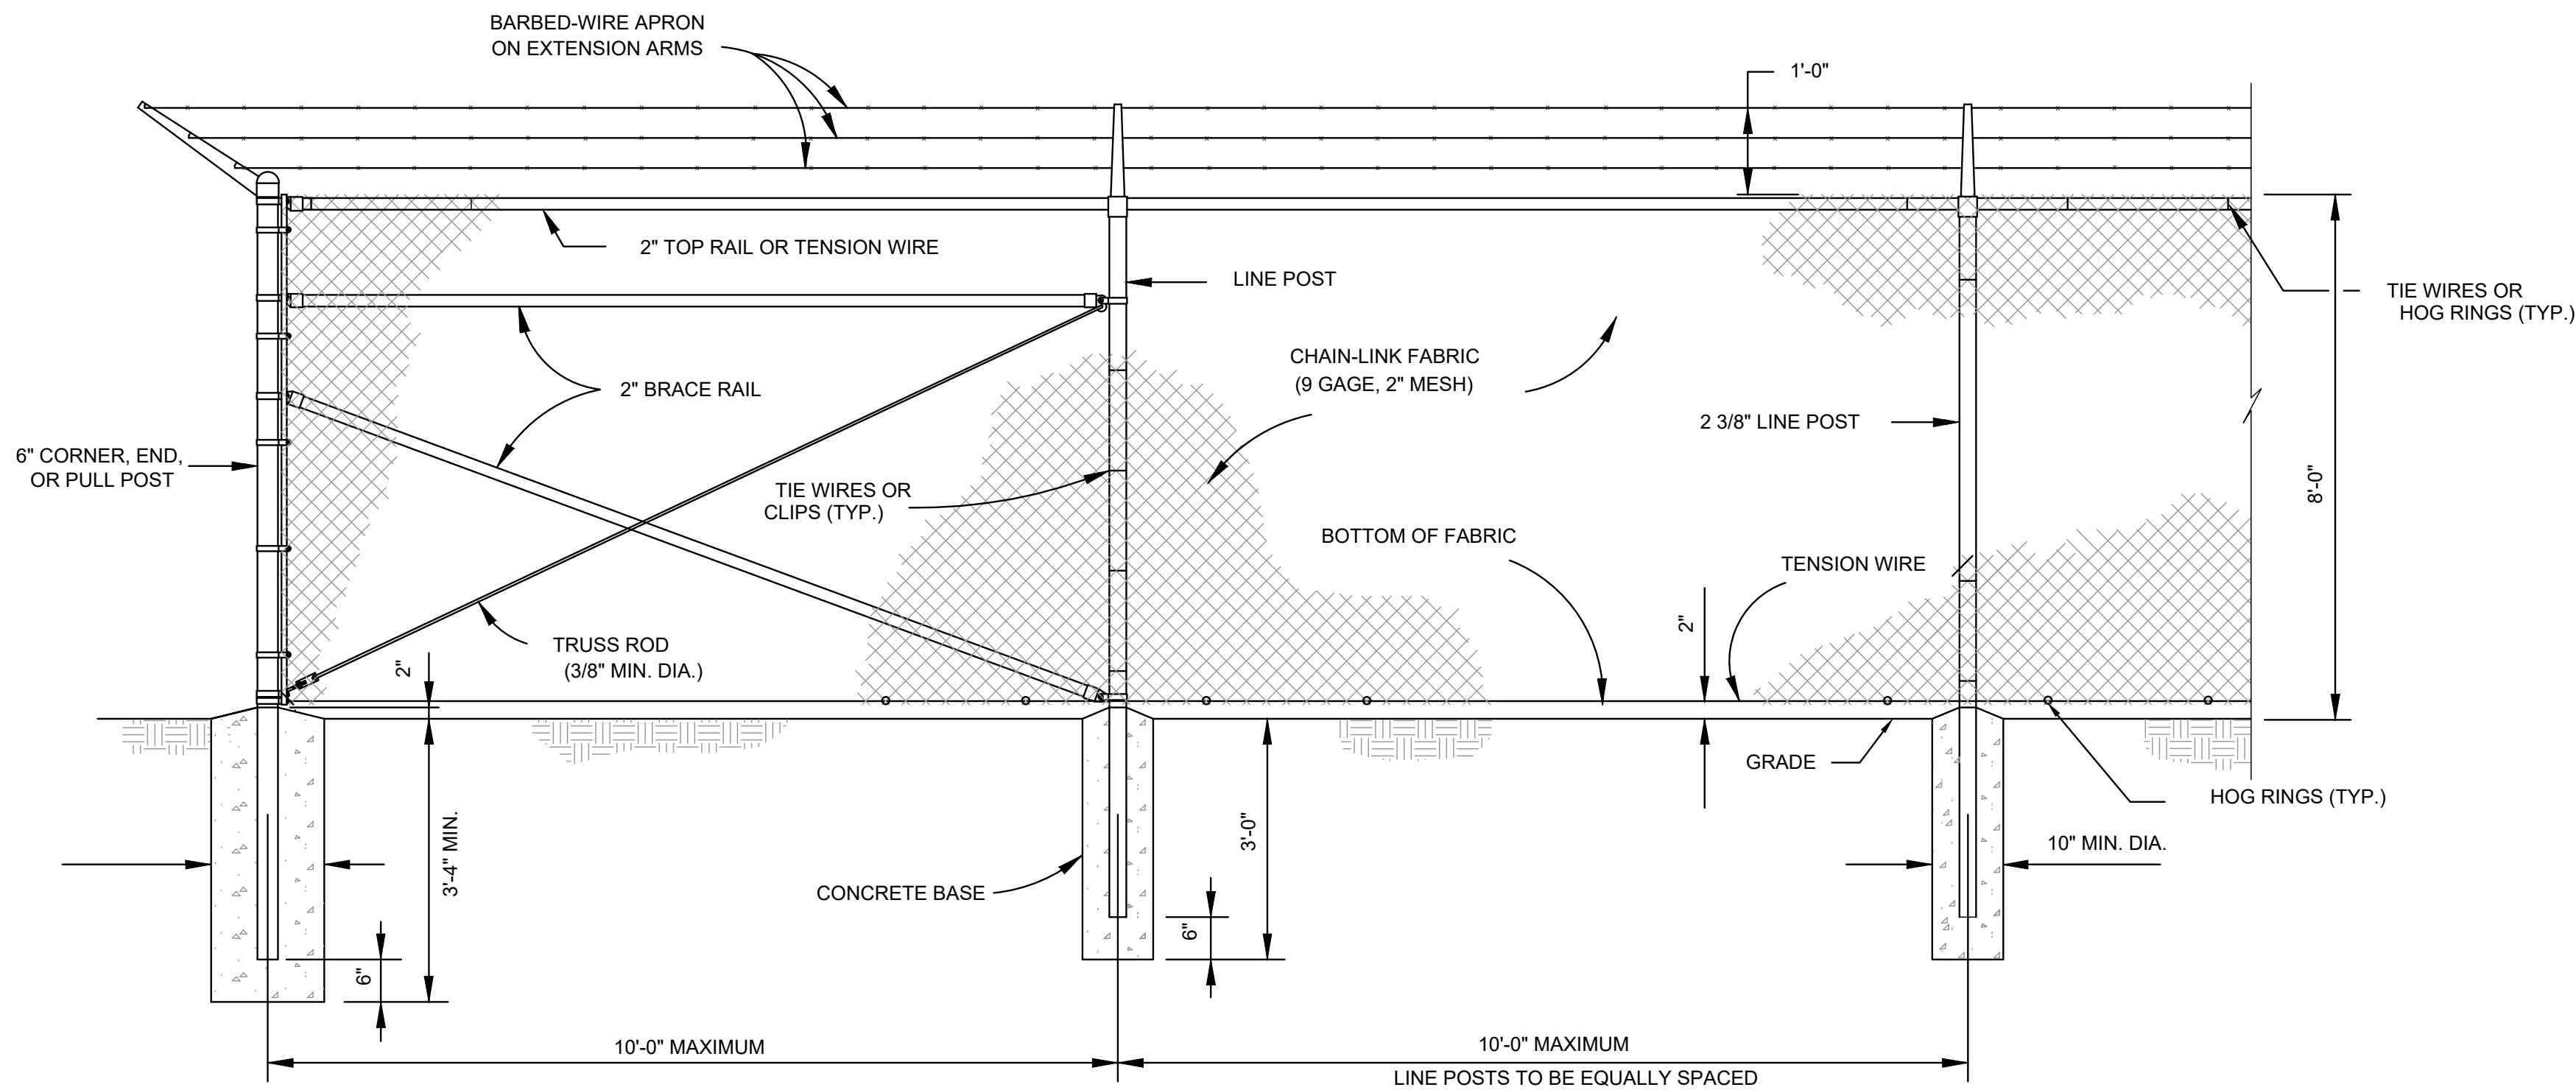

CHAIN-LINK SAFETY FENCE (H)
N.T.S.

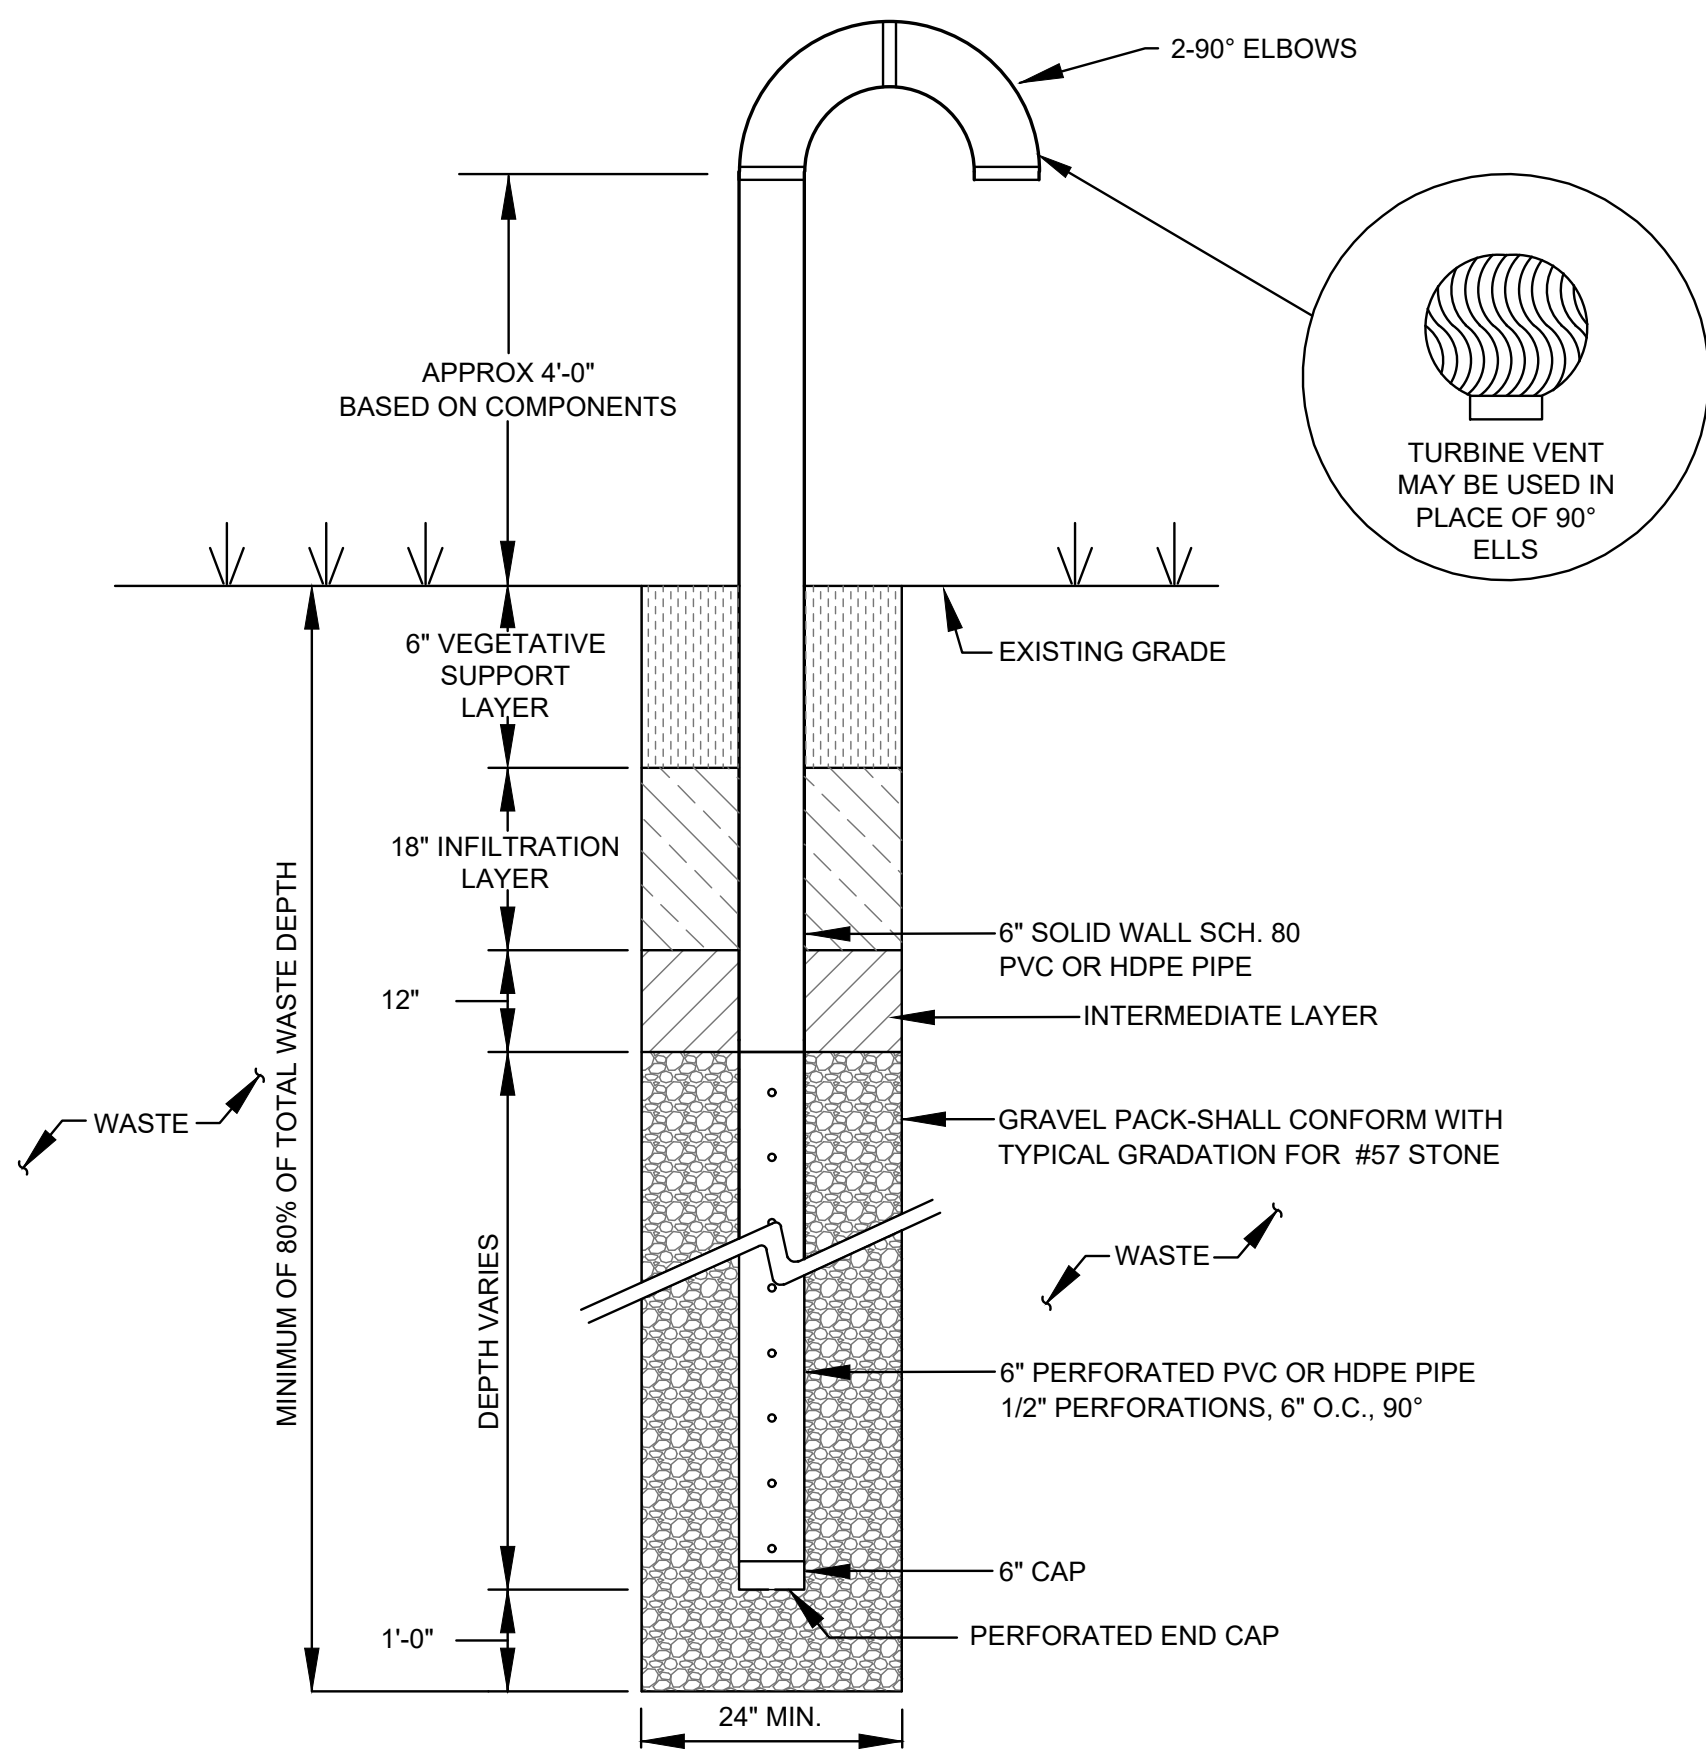

LFG PASSIVE VENT IN WASTE (J)
N.T.S.

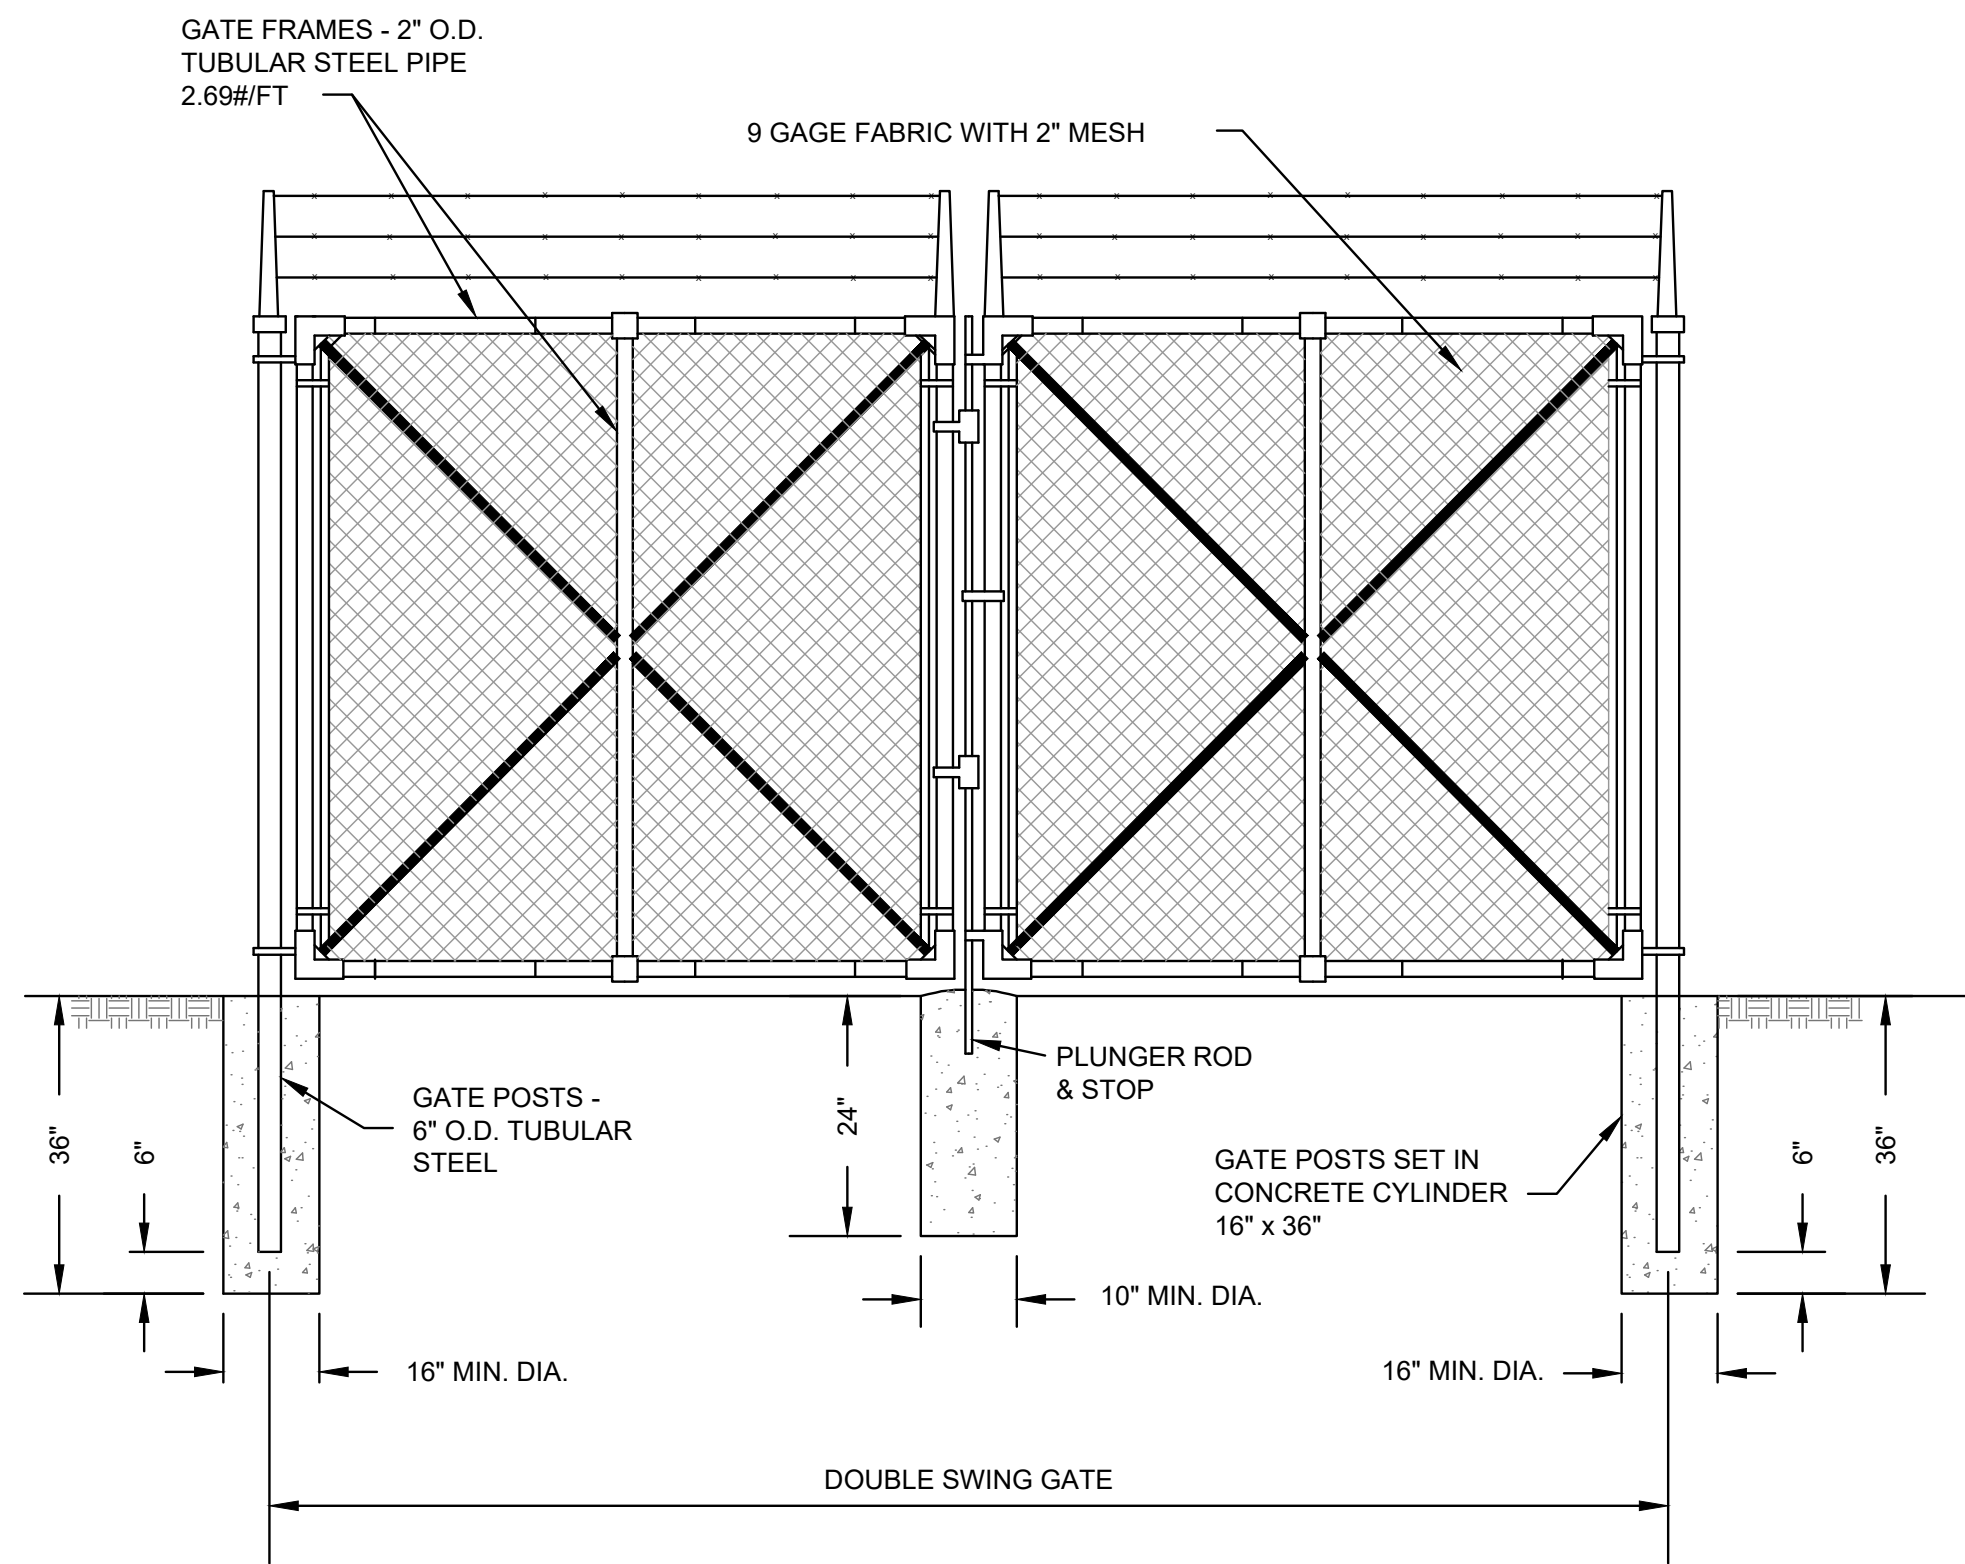

CHAIN-LINK FENCE DOUBLE GATE (I)
N.T.S.



It is a violation of New York Education Law Article 145 Sec.7209, for any person, unless acting under the direction of a licensed architect, professional engineer, or land surveyor, to alter an item in any way. If an item bearing the seal of an architect, engineer, or land surveyor is altered; the altering architect, engineer, or land surveyor shall affix to the item their seal and notation "altered by" followed by their signature and date of such alteration, and a specific description of the alteration.

© 2024 LaBella Associates

Town of Palmyra

1180 Canandaigua Road
Palmyra, New York



Landfill Closure Remediation

944 Garnsey Road
Palmyra, New York

NO.	DATE:	DESCRIPTION:

Revisions

PROJECT NUMBER: 2242908

DRAWN BY: IWW

REVIEWED BY: DWT

ISSUED FOR: CONSTRUCTION

DATE: 08/27/2024

DRAWING NAME:

SITE DETAILS

DRAWING NUMBER: